LUXURIA MALDIVES

11D- CB04-01- ROOM BLOCK 04 - POOL BAR

LUXURIA HOTELS & RESORTS MALDIVES

ARCHITECTURAL DRAWINGS

The contents of these drawings remai

LIST OF DRAWINGS

SHEET NUMBER	SHEET NAME	SHEET ISSUE DATE	CURRENT REVISION	CURRENT REVISION DATE
00-GENERAL				
00-000-000-01	COVER PAGE	-	00	
00-000-000-02	LIST OF DRAWINGS	-	00	
00-000-000-03	LOCATION PLAN	-	00	
05 - AREAS				
05-100-L00-01	AREA PLAN & SCHEDULE - GROUND FLOOR	-	00	
05-100-L01-01	AREA PLAN & SCHEDULE - FIRST FLOOR	-	00	
05-100-L02-01	AREA PLAN & SCHEDULE - SECOND FLOOR	-	00	
05-100-R01-01	AREA PLAN & SCHEDULE - ROOF	-	00	
05-100-R02-01	AREA PLAN & SCHEDULE - STAIR ROOF	-	00	
10 - GENERAL ARRANGEMENT				
10-100-L00-01	GROUND FLOOR PLAN	-	00	
10-100-L01-01	FIRST FLOOR PLAN	-	00	
10-100-L02-01	SECOND FLOOR PLAN	-	00	
10-100-R01-01	ROOF PLAN	-	00	
10-100-R02-01	STAIR ROOF PLAN	-	00	
10-200-000-01	SECTIONS	-	00	
10-300-000-01	ELEVATIONS	-	00	
10-300-000-02	ELEVATIONS	-	00	
10-500-000-01	3D VIEWS	-	00	
19 - DOORS				
19-400-000-01	DOOR SCHEDULE & DETAILS	-	00	
19-400-000-02	DOOR SCHEDULE & DETAILS	-	00	
20 -WINDOWS				
20-400-000-01	WINDOW SCHEDULE & DETAILS	-	00	
21 - CEILING				
21-100-L00-01	REFLECTED CEILING PLAN - GROUND FLOOR	-	00	
21-100-L01-01	REFLECTED CEILING PLAN - FIRST FLOOR	-	00	
21-100-L02-01	REFLECTED CEILING PLAN - SECOND FLOOR	-	00	
24 - TYPICAL DETAILS				
24-600-000-01	TYPICAL DETAILS	-	00	

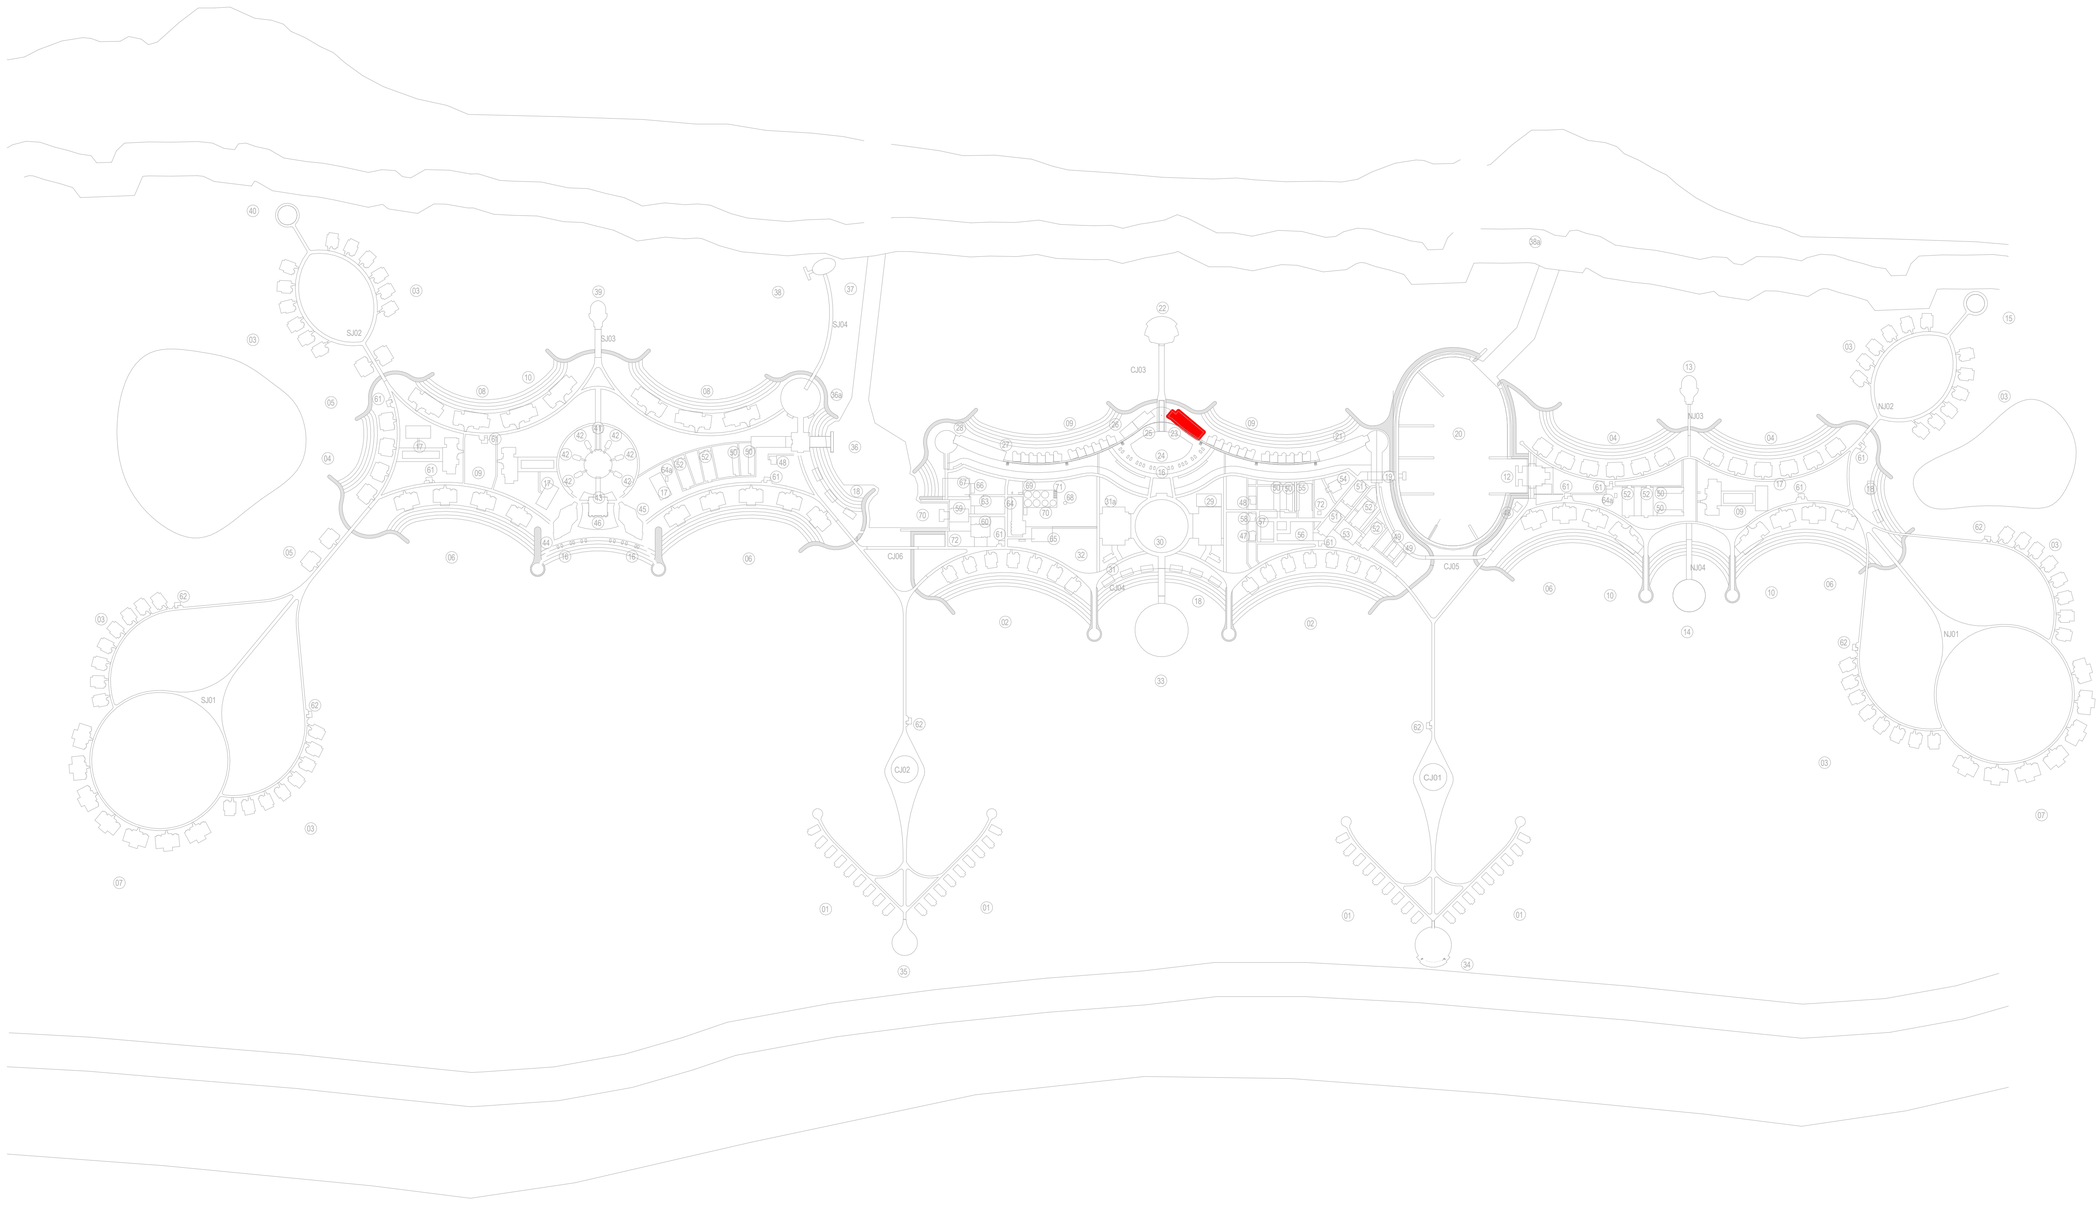

LOCATION PLAN

1 : 4500

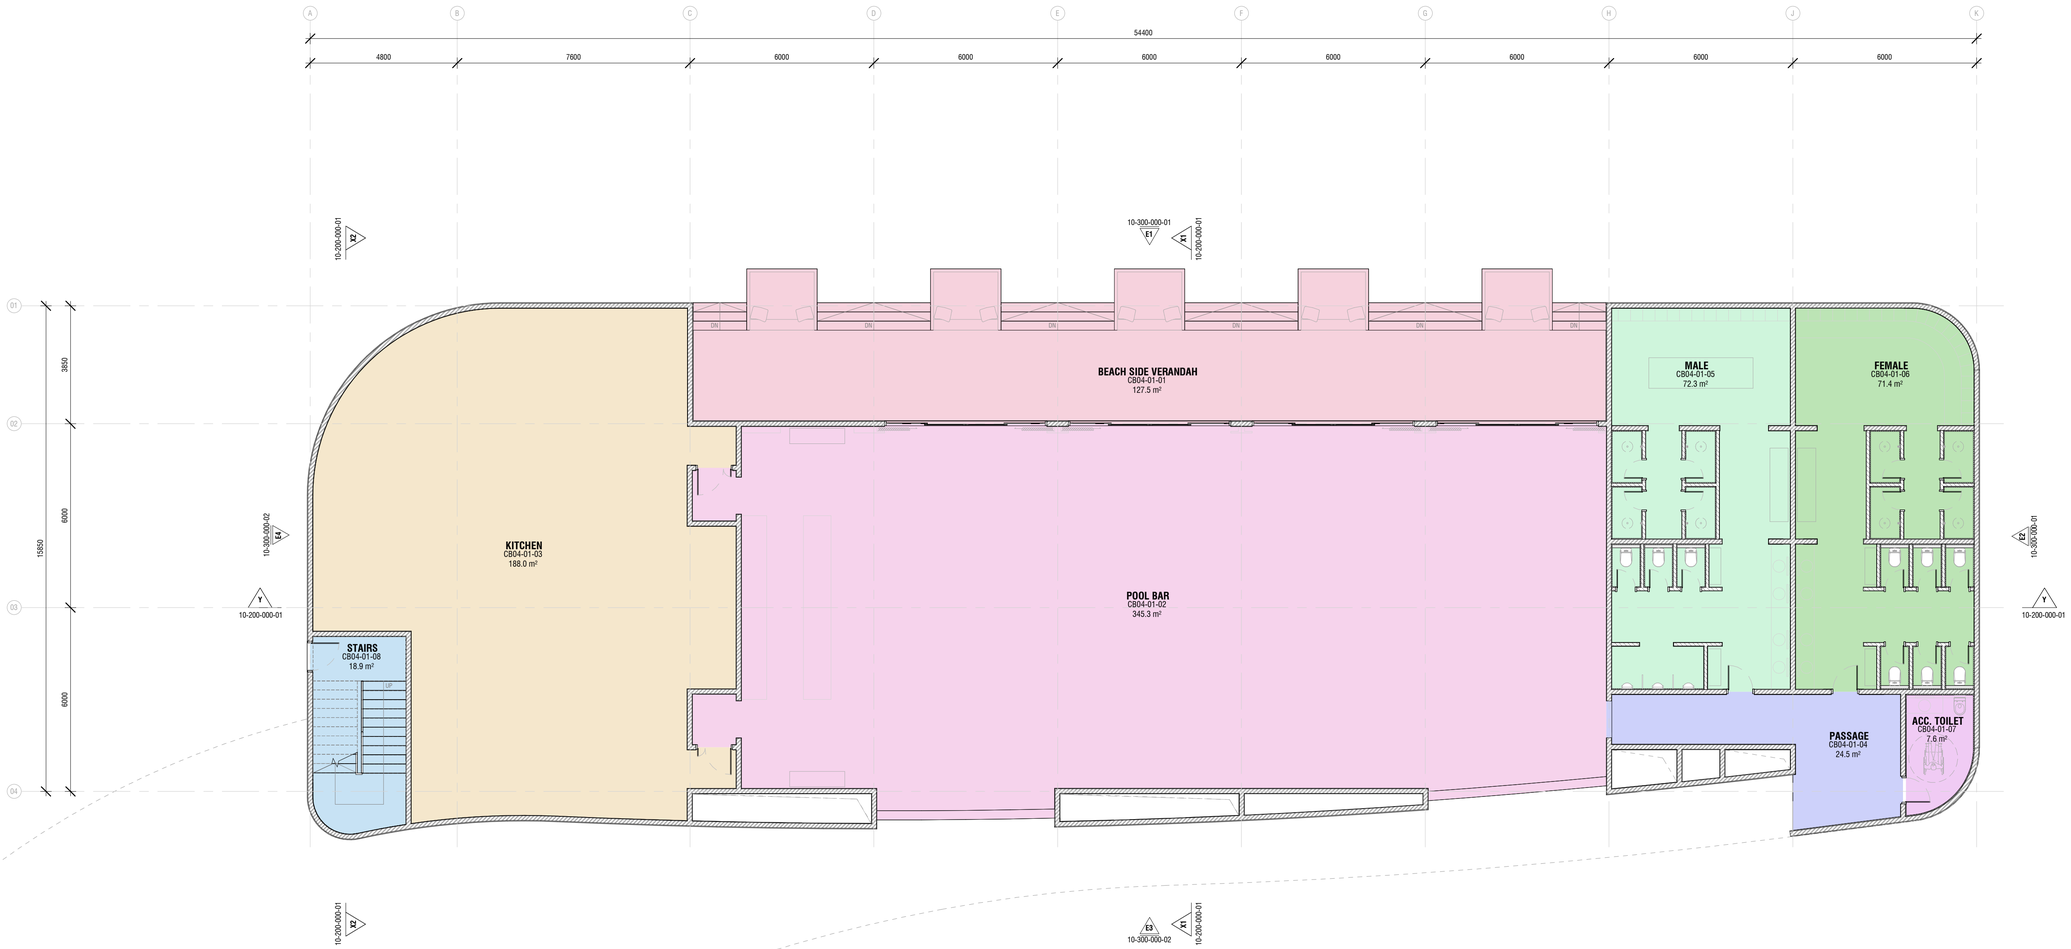

AREA PLAN & SCHEDULE - GROUND FLOOR

1 : 100

11D - CB04 - ROOM BLOCK 04 - POOL BAR					
NO. OF UNITS	COVERED / MOT AREA PER UNIT (SQM)	OPEN AREA PER UNIT (SQM)	TOTAL BUA PER UNIT (SQM) (COVERED + OPEN AREA)	TOTAL BUA (NO. OF UNITS x TOTAL BUA PER UNIT)	TOTAL MOT AREA (SQM) (NO. OF UNITS x COVERED / MOT AREA PER UNIT)
1	793.4 m²	430.7 m²	1224.1 m²	1224.1 m²	793.4 m²

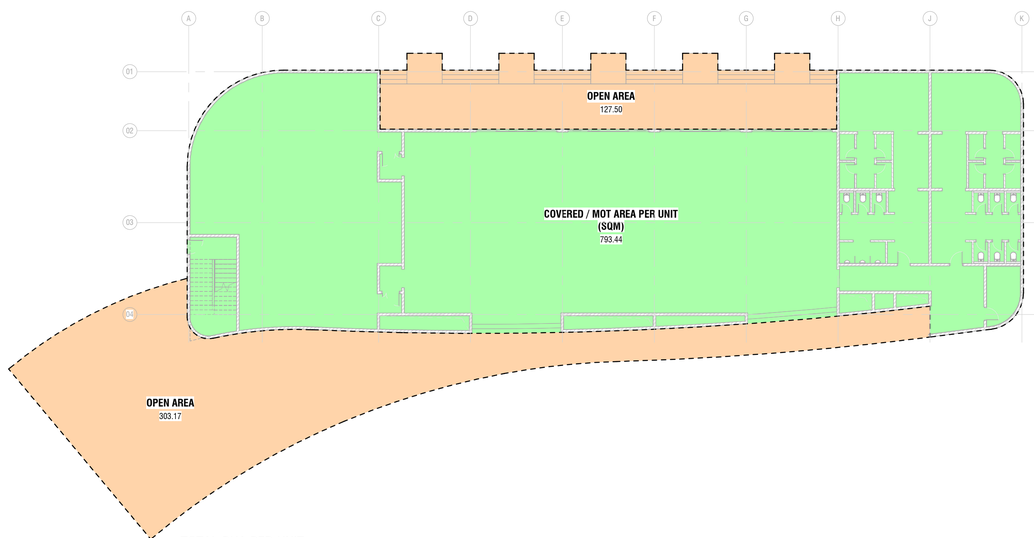

TOTAL BUA PER UNIT

1 : 200

AREA SCHEDULE - GROUND FLOOR		
NAME	NUMBER	AREA
GROUND FLOOR LVL		
BEACH SIDE VERANDAH	CB04-01-01	127.5 m²
POOL BAR	CB04-01-02	345.3 m²
KITCHEN	CB04-01-03	188.0 m²
PASSAGE	CB04-01-04	24.5 m²
MALE	CB04-01-05	72.3 m²
FEMALE	CB04-01-06	71.4 m²
ACC. TOILET	CB04-01-07	7.6 m²
STAIRS	CB04-01-08	18.9 m²
TOTAL USABLE AREA		855.6 m²

	TOTAL BUA PER UNIT	NO. OF UNITS	TOTAL BUA
GROUND FLOOR	1224.10 m²	01	4488.48 m²
FIRST FLOOR	1155.31 m²		
SECOND FLOOR	1211.49 m²		
ROOF SLAB	874.48 m²		
STAIR ROOF	23.1 m²		
TOTAL	4488.48 m²		

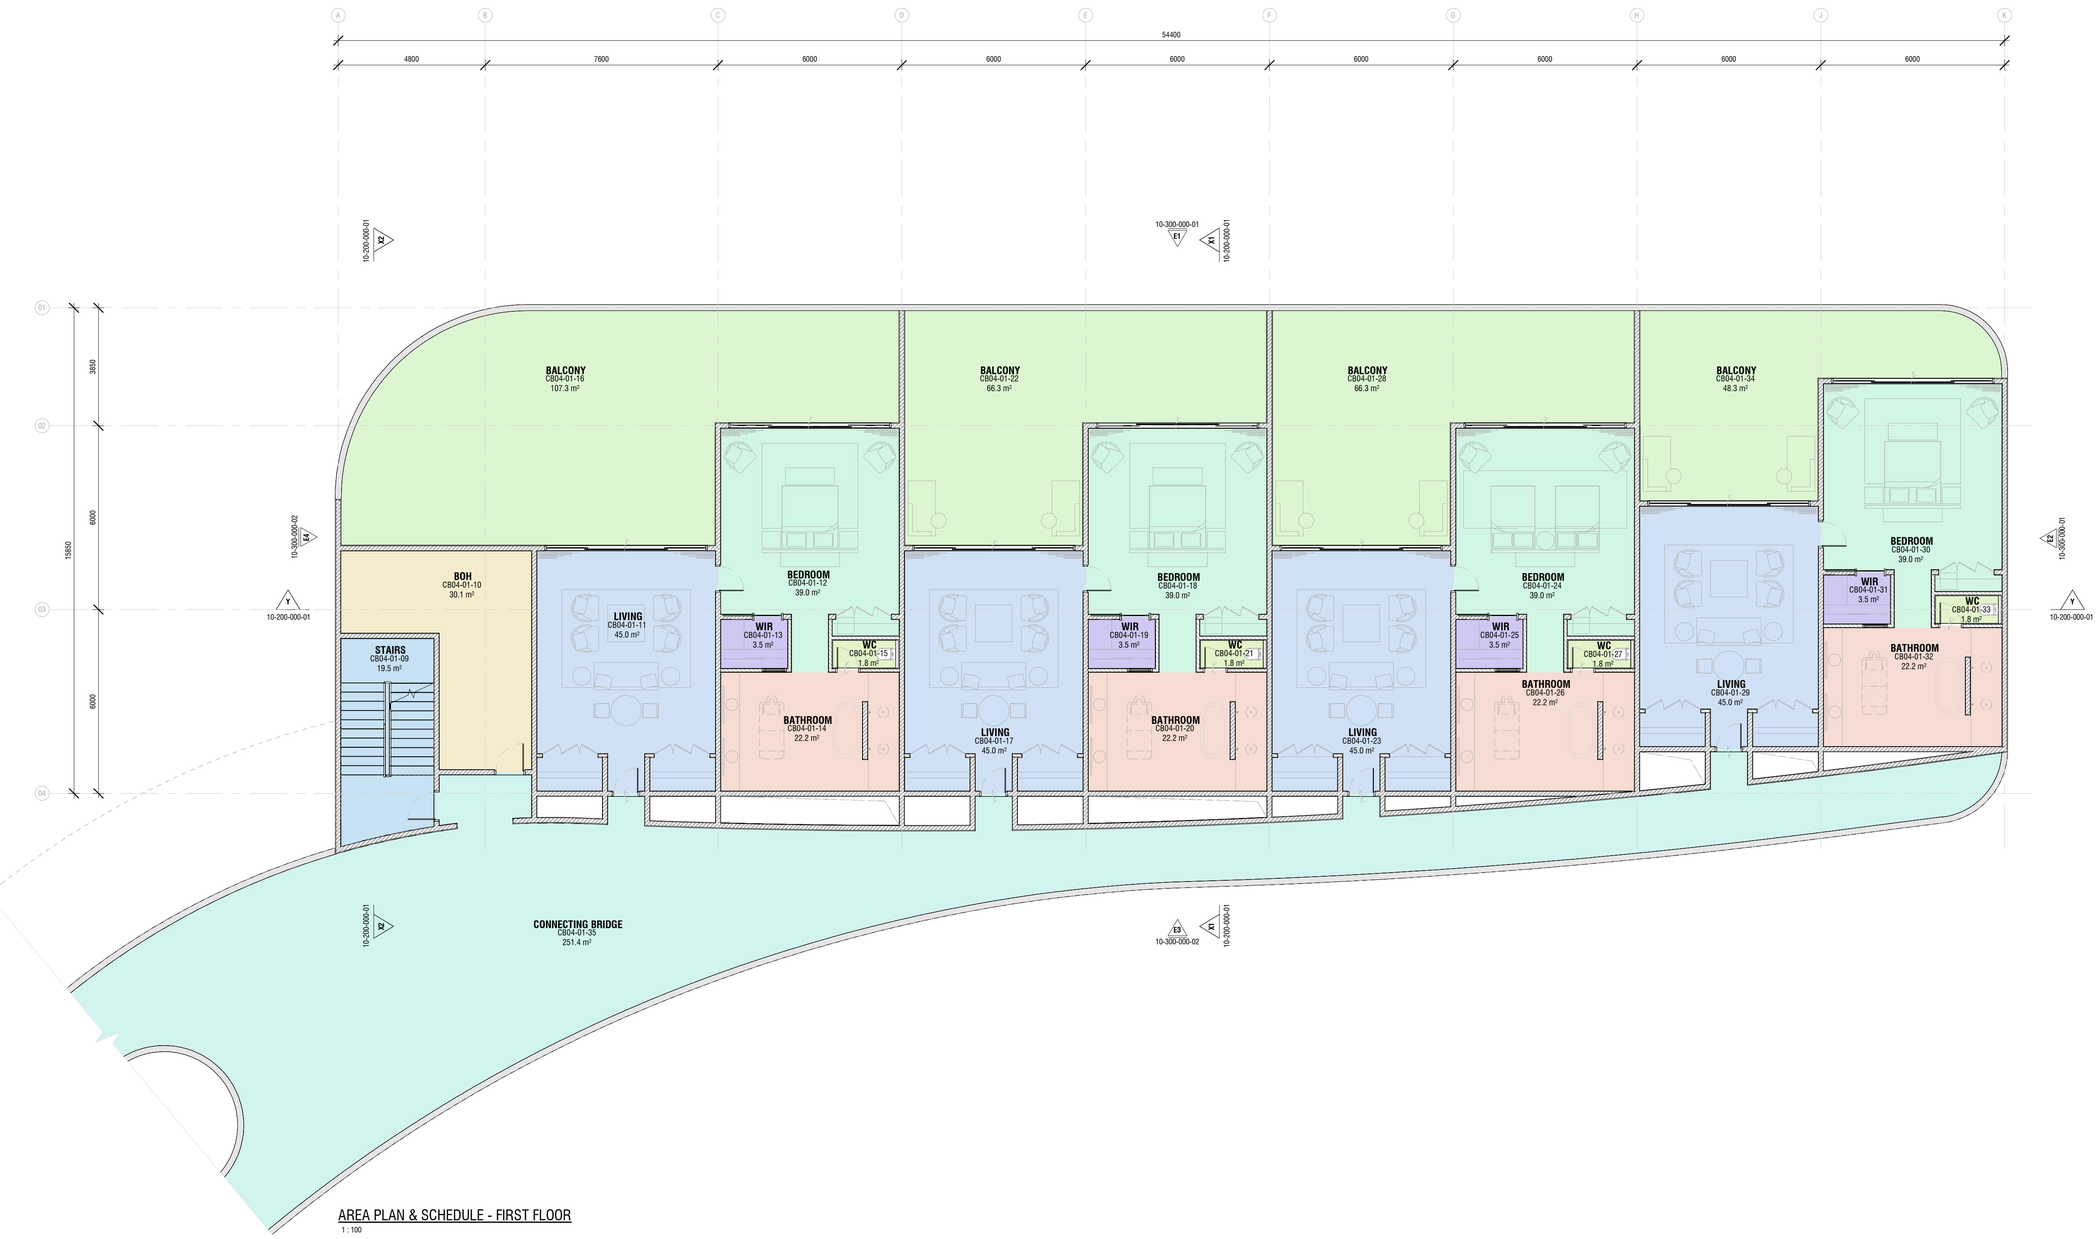

AREA PLAN & SCHEDULE - FIRST FLOOR

1 : 100

AREA SCHEDULE - FIRST FLOOR

NAME	NUMBER	AREA
FIRST FLOOR LVL		
STAIRS	CB04-01-09	19.5 m²
BOH	CB04-01-10	30.1 m²
LIVING	CB04-01-11	45.0 m²
BEDROOM	CB04-01-12	39.0 m²
WIR	CB04-01-13	3.5 m²
BATHROOM	CB04-01-14	22.2 m²
WC	CB04-01-15	1.8 m²
BALCONY	CB04-01-16	107.3 m²
LIVING	CB04-01-17	45.0 m²
BEDROOM	CB04-01-18	39.0 m²
WIR	CB04-01-19	3.5 m²
BATHROOM	CB04-01-20	22.2 m²
WC	CB04-01-21	1.8 m²
BALCONY	CB04-01-22	66.3 m²
LIVING	CB04-01-23	45.0 m²
BEDROOM	CB04-01-24	39.0 m²
WIR	CB04-01-25	3.5 m²
BATHROOM	CB04-01-26	22.2 m²
WC	CB04-01-27	1.8 m²
BALCONY	CB04-01-28	66.3 m²
LIVING	CB04-01-29	45.0 m²
BEDROOM	CB04-01-30	39.0 m²
WIR	CB04-01-31	3.5 m²
BATHROOM	CB04-01-32	22.2 m²
WC	CB04-01-33	1.8 m²
BALCONY	CB04-01-34	48.3 m²
CONNECTING BRIDGE	CB04-01-35	251.4 m²
TOTAL USABLE AREA		1035.5 m²

	TOTAL BUA PER UNIT	NO. OF UNITS	TOTAL BUA
GROUND FLOOR	1224.10 m²	01	4488.48 m²
FIRST FLOOR	1155.31 m²		
SECOND FLOOR	1211.49 m²		
ROOF SLAB	874.48 m²		
STAIR ROOF	23.1 m²		
TOTAL	4488.48 m²		

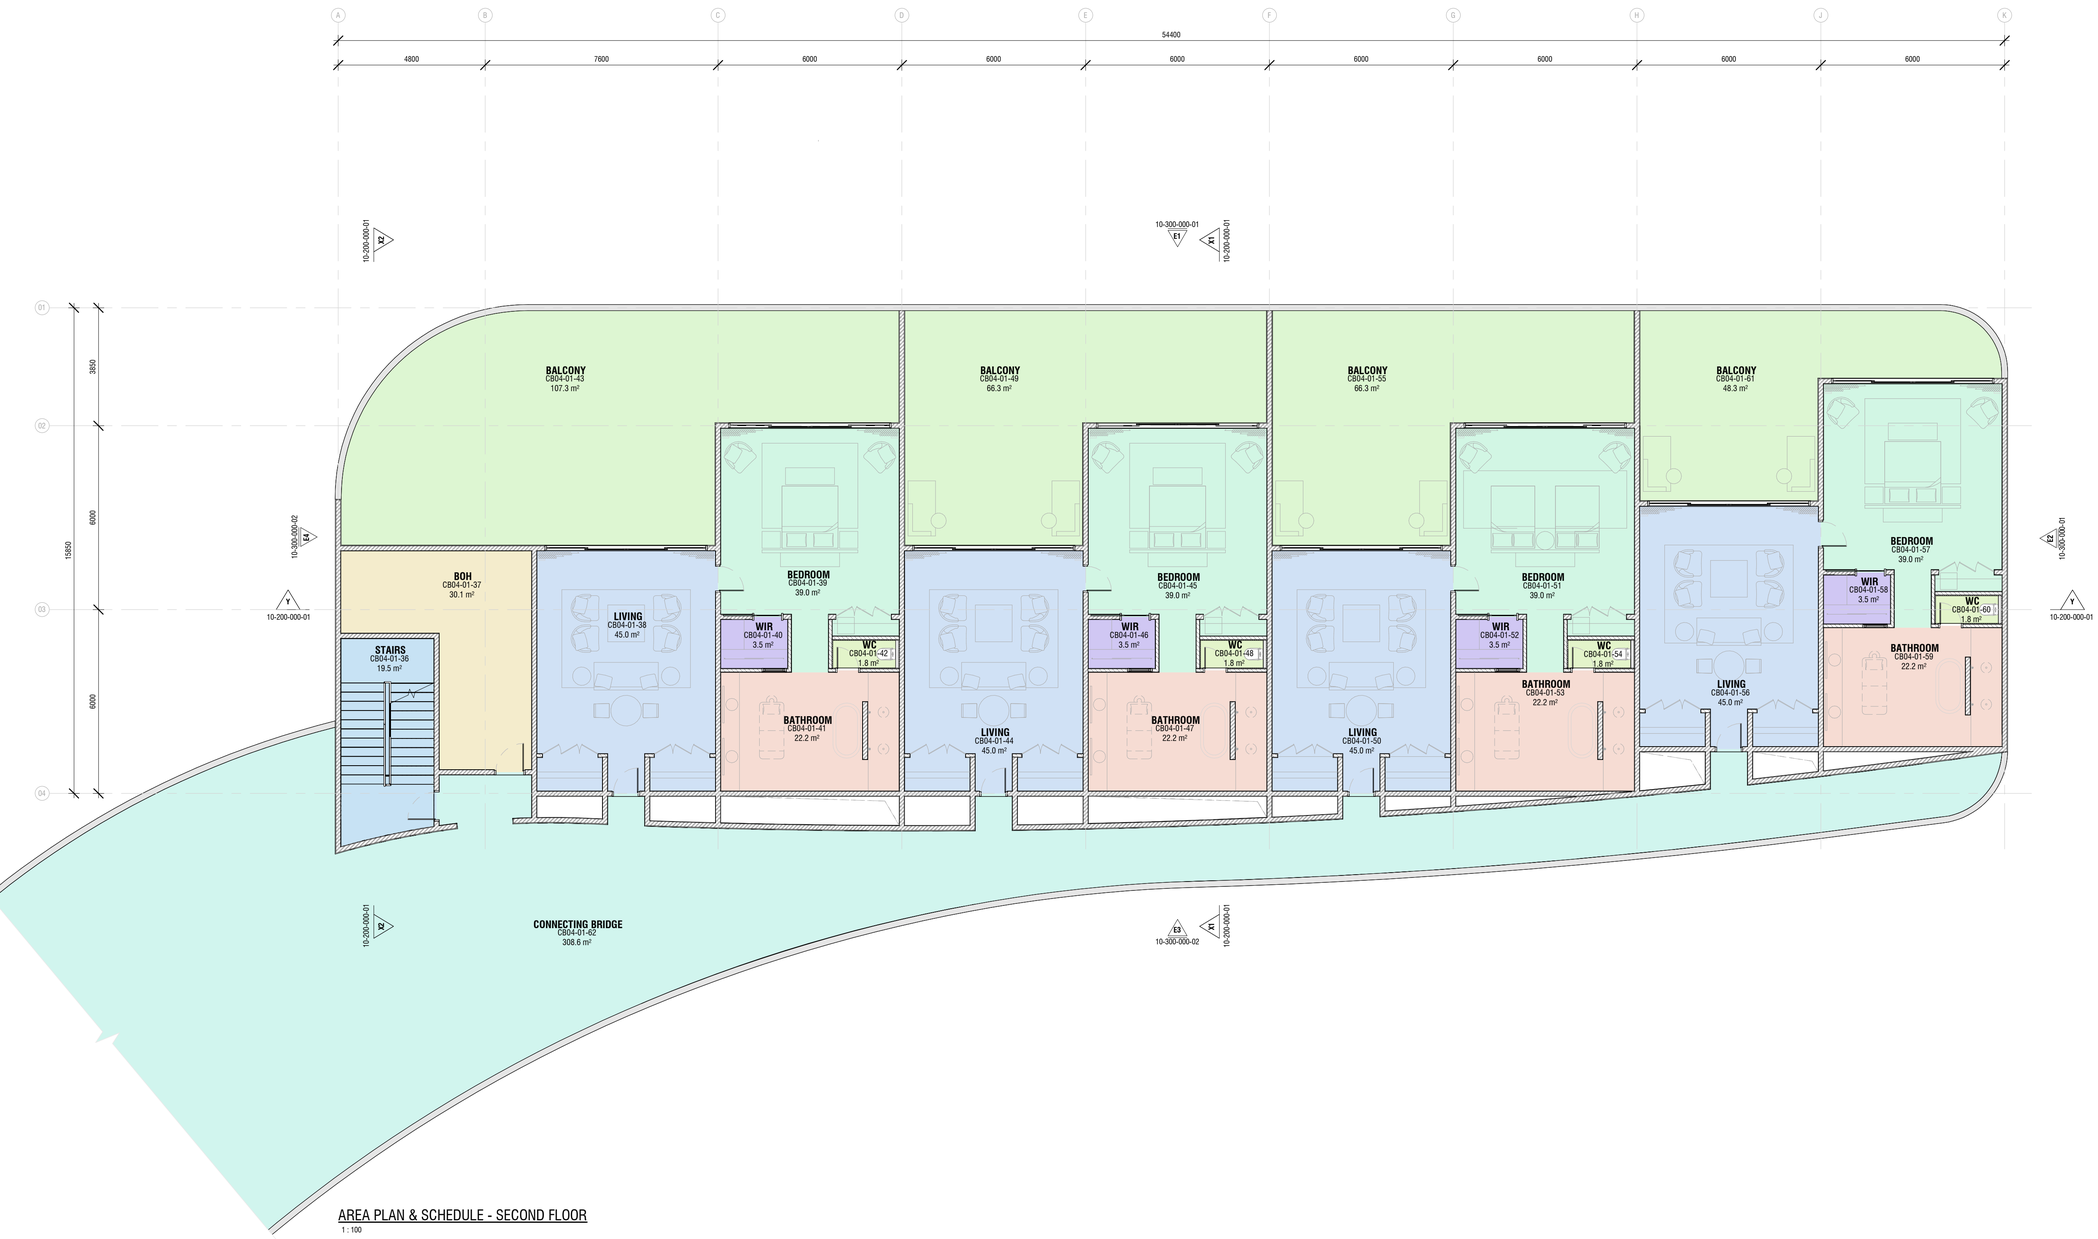

AREA PLAN & SCHEDULE - SECOND FLOOR

1 : 100

AREA SCHEDULE - SECOND FLOOR

NAME	NUMBER	AREA
SECOND FLOOR LVL		
STAIRS	CB04-01-36	19.5 m²
BOH	CB04-01-37	30.1 m²
LIVING	CB04-01-38	45.0 m²
BEDROOM	CB04-01-39	39.0 m²
WIR	CB04-01-40	3.5 m²
BATHROOM	CB04-01-41	22.2 m²
WC	CB04-01-42	1.8 m²
BALCONY	CB04-01-43	107.3 m²
LIVING	CB04-01-44	45.0 m²
BEDROOM	CB04-01-45	39.0 m²
WIR	CB04-01-46	3.5 m²
BATHROOM	CB04-01-47	22.2 m²
WC	CB04-01-48	1.8 m²
BALCONY	CB04-01-49	66.3 m²
LIVING	CB04-01-50	45.0 m²
BEDROOM	CB04-01-51	39.0 m²
WIR	CB04-01-52	3.5 m²
BATHROOM	CB04-01-53	22.2 m²
WC	CB04-01-54	1.8 m²
BALCONY	CB04-01-55	66.3 m²
LIVING	CB04-01-56	45.0 m²
BEDROOM	CB04-01-57	39.0 m²
WIR	CB04-01-58	3.5 m²
BATHROOM	CB04-01-59	22.2 m²
WC	CB04-01-60	1.8 m²
BALCONY	CB04-01-61	48.3 m²
CONNECTING BRIDGE	CB04-01-62	308.6 m²
TOTAL USABLE AREA		1092.7 m²

	TOTAL BUA PER UNIT	NO. OF UNITS	TOTAL BUA
GROUND FLOOR	1224.10 m²	01	4488.48 m²
FIRST FLOOR	1155.31 m²		
SECOND FLOOR	1211.49 m²		
ROOF SLAB	874.48 m²		
STAIR ROOF	23.1 m²		
TOTAL	4488.48 m²		

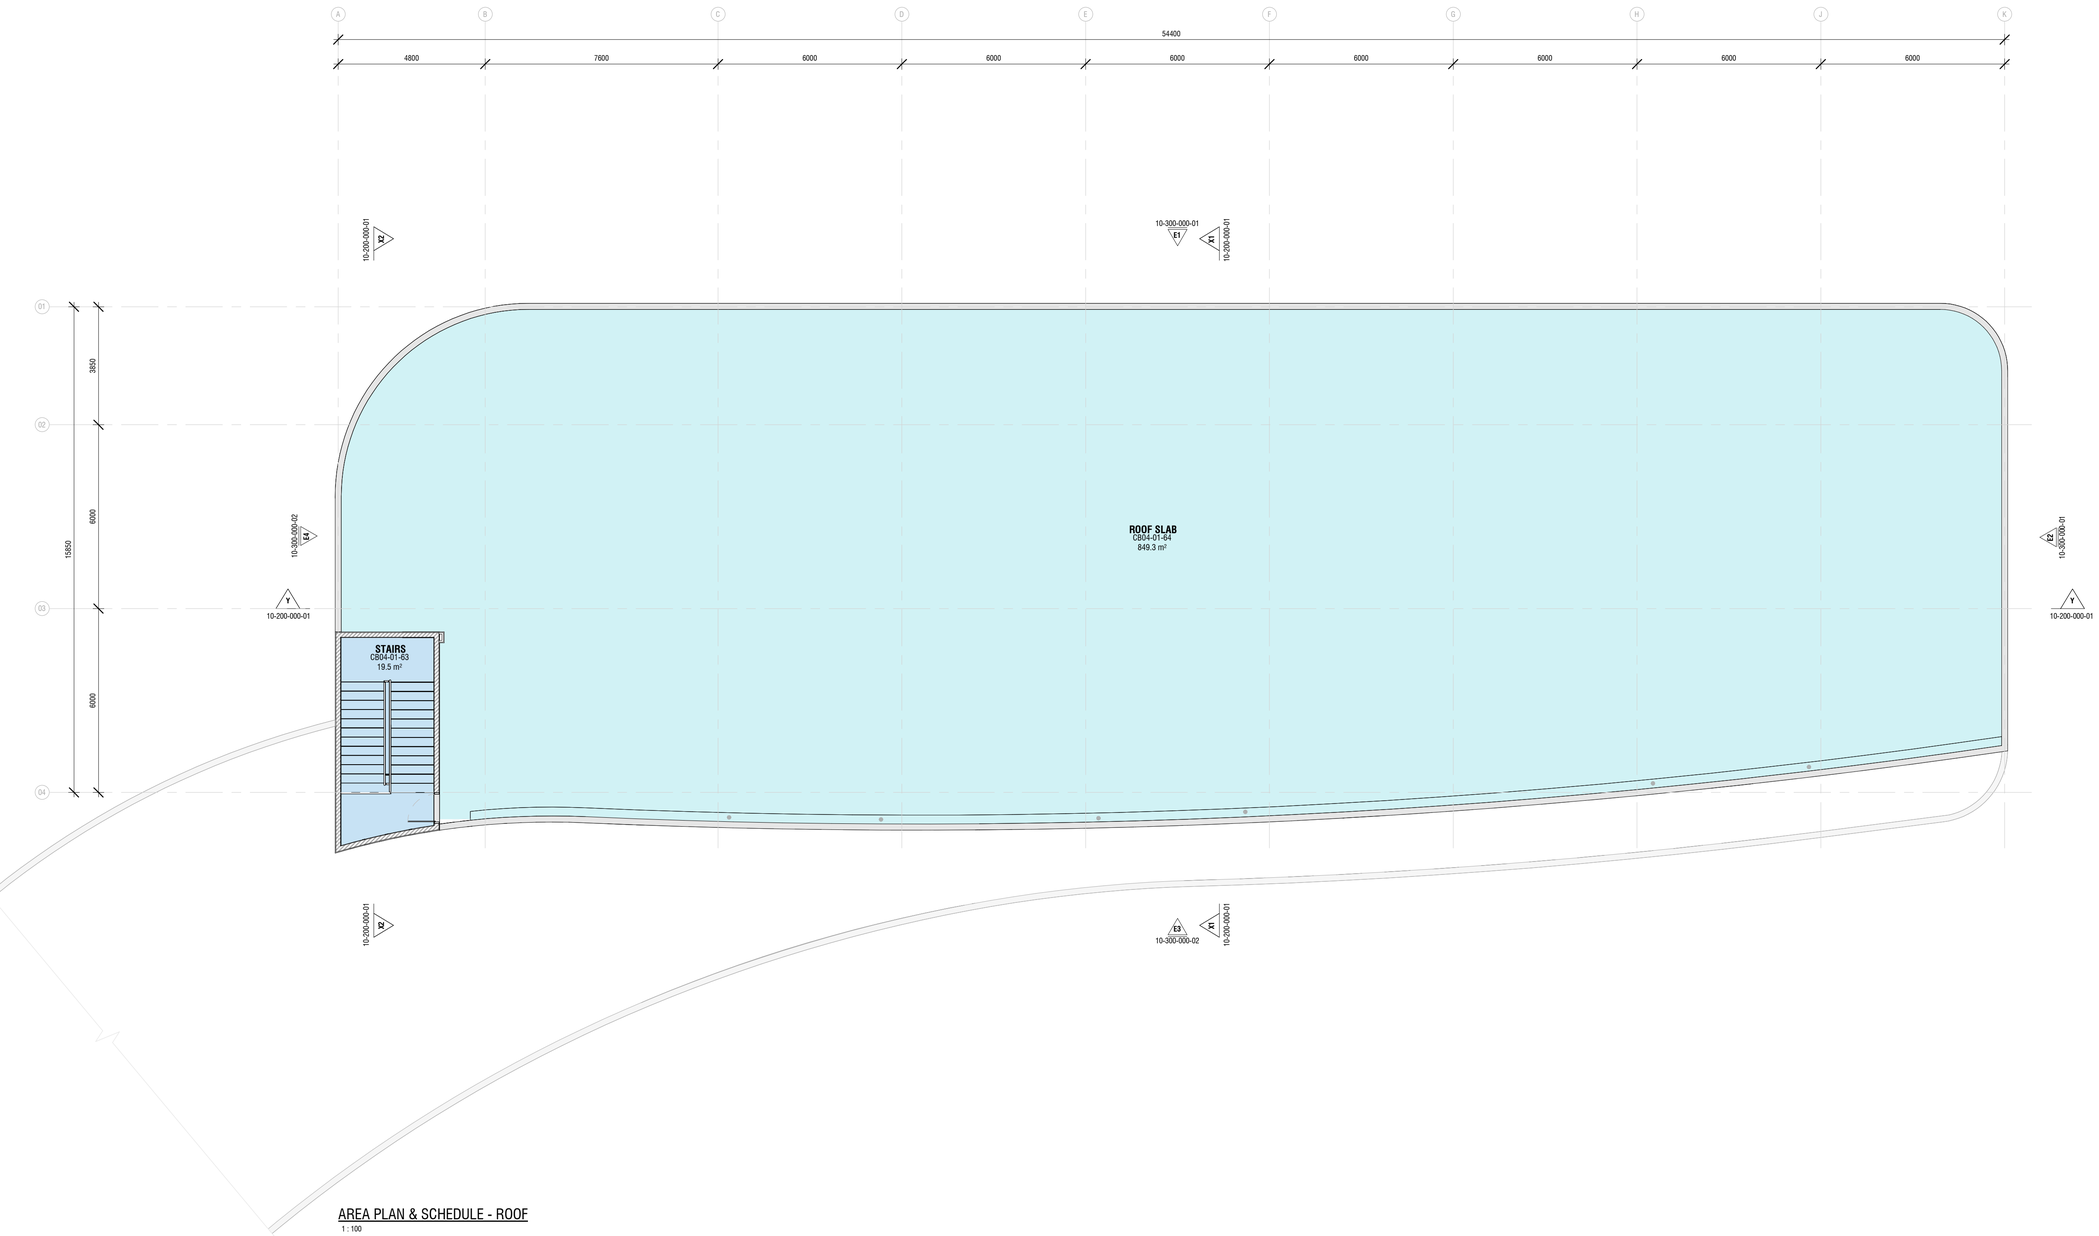

AREA PLAN & SCHEDULE - ROOF

1 : 100

AREA SCHEDULE - ROOF

NAME	NUMBER	AREA
ROOF SLAB LVL		
STAIRS	CB04-01-63	19.5 m²
ROOF SLAB	CB04-01-64	849.3 m²
TOTAL USABLE AREA		868.8 m²

	TOTAL BUA PER UNIT	NO. OF UNITS	TOTAL BUA
GROUND FLOOR	1224.10 m²	01	4488.48 m²
FIRST FLOOR	1155.31 m²		
SECOND FLOOR	1211.49 m²		
ROOF SLAB	874.48 m²		
STAIR ROOF	23.1 m²		
TOTAL	4488.48 m²		

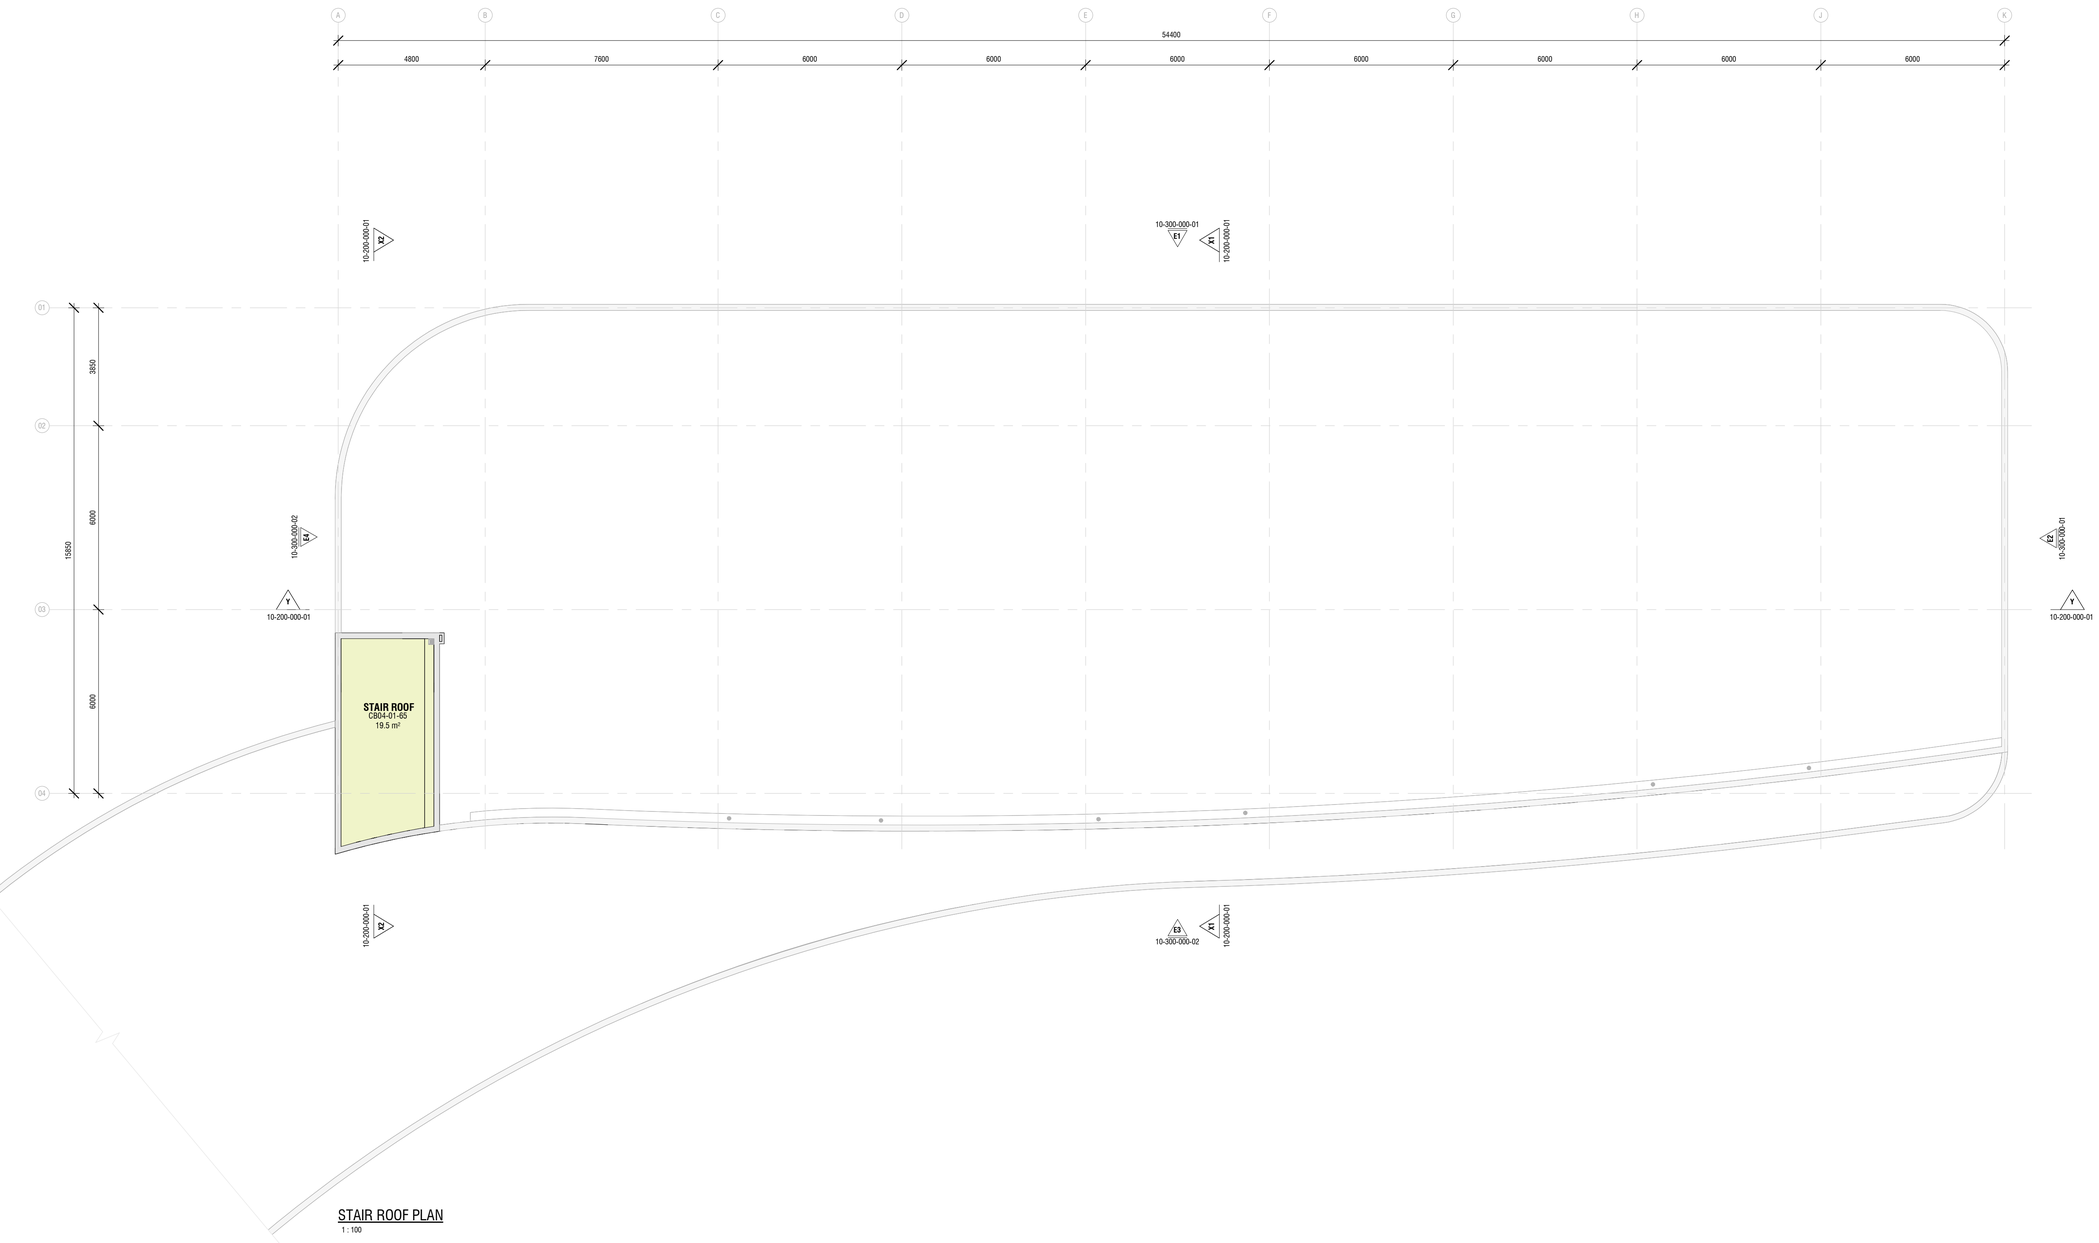

STAIR ROOF PLAN

1 : 100

AREA SCHEDULE - STAIR ROOF

NAME	NUMBER	AREA
ROOF APEX LVL		
STAIR ROOF	CB04-01-65	19.5 m²
TOTAL USABLE AREA		19.5 m²

	TOTAL BUA PER UNIT	NO. OF UNITS	TOTAL BUA
GROUND FLOOR	1224.10 m²	01	4488.48 m²
FIRST FLOOR	1155.31 m²		
SECOND FLOOR	1211.49 m²		
ROOF SLAB	874.48 m²		
STAIR ROOF	23.1 m²		
TOTAL	4488.48 m²		

WALL LEGEND

- 150mm THICK SOLID BLOCK MASONRY WALL
- 100mm THICK SOLID BLOCK MASONRY WALL
- 150mm CONCRETE WALL / FILLINGS
- 20mm GLASS WALL

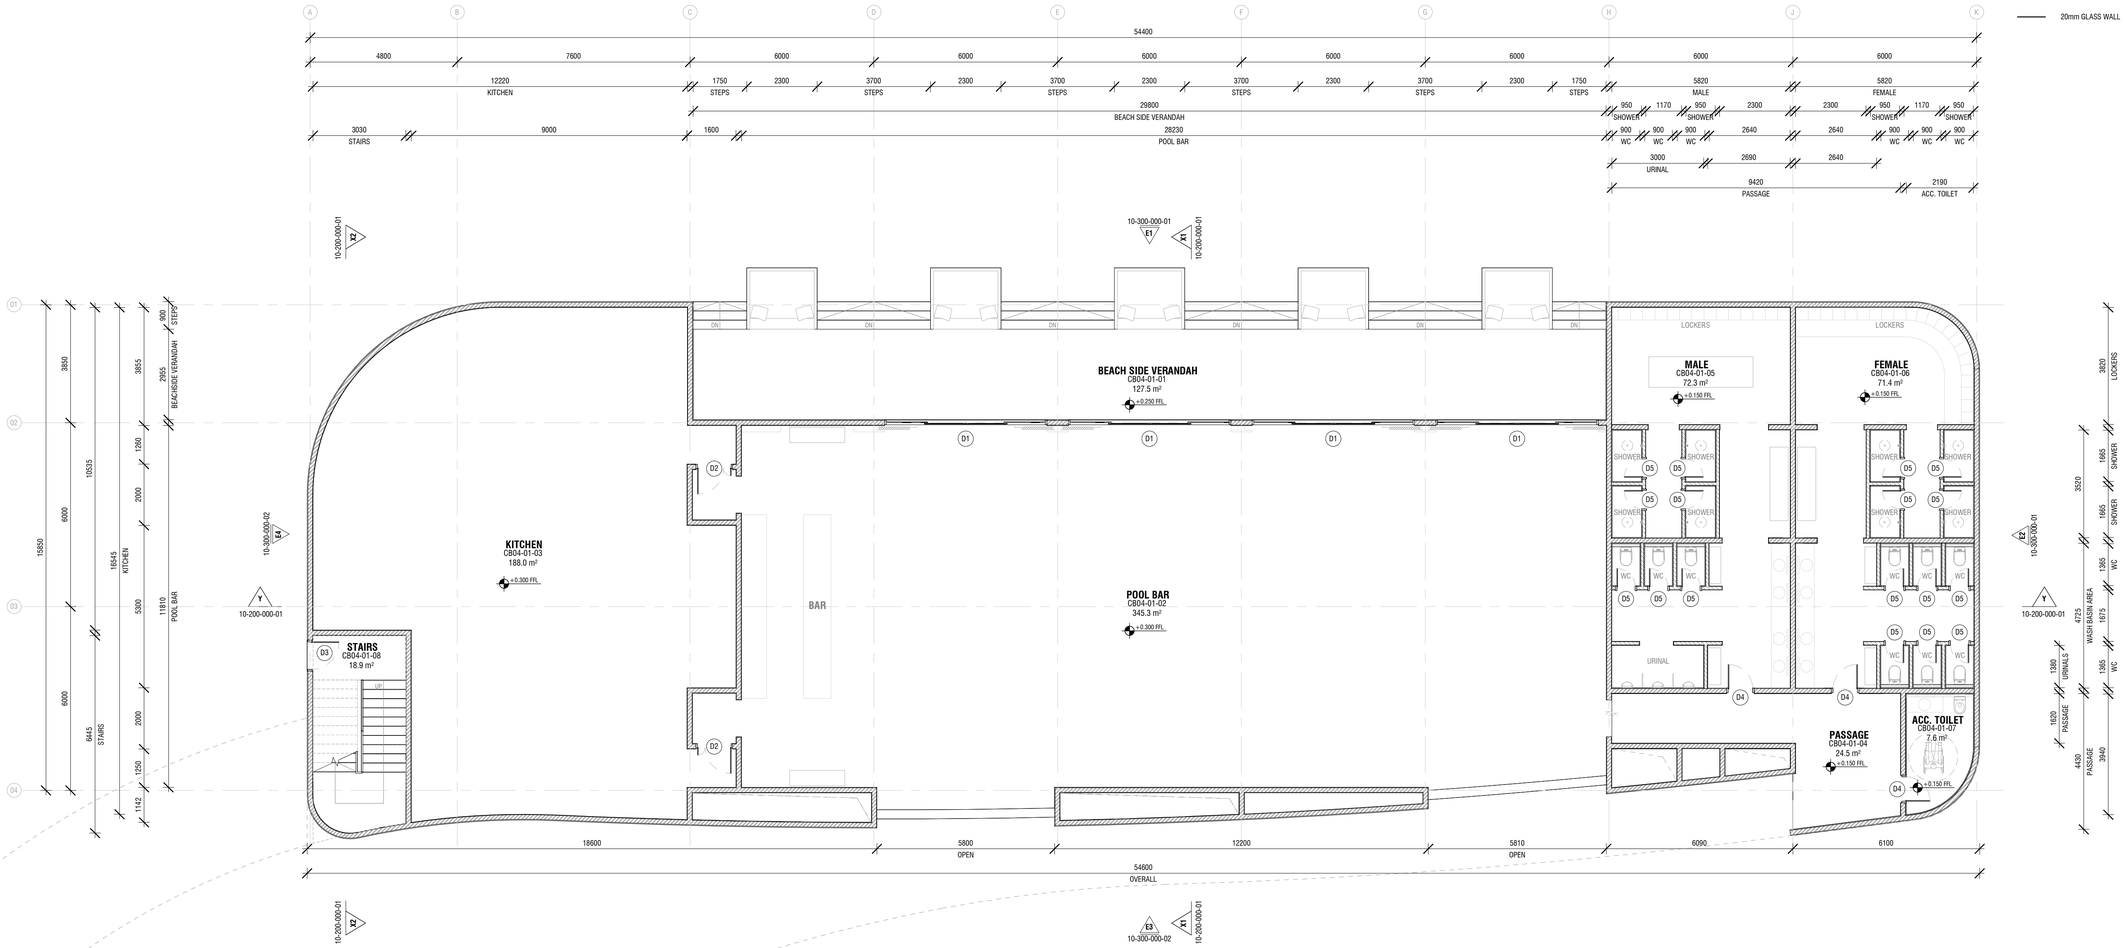

GROUND FLOOR PLAN

1 : 100

WALL LEGEND

- 150mm THICK SOLID BLOCK MASONRY WALL
- 100mm THICK SOLID BLOCK MASONRY WALL
- 150mm CONCRETE WALL / FILLINGS
- 20mm GLASS WALL

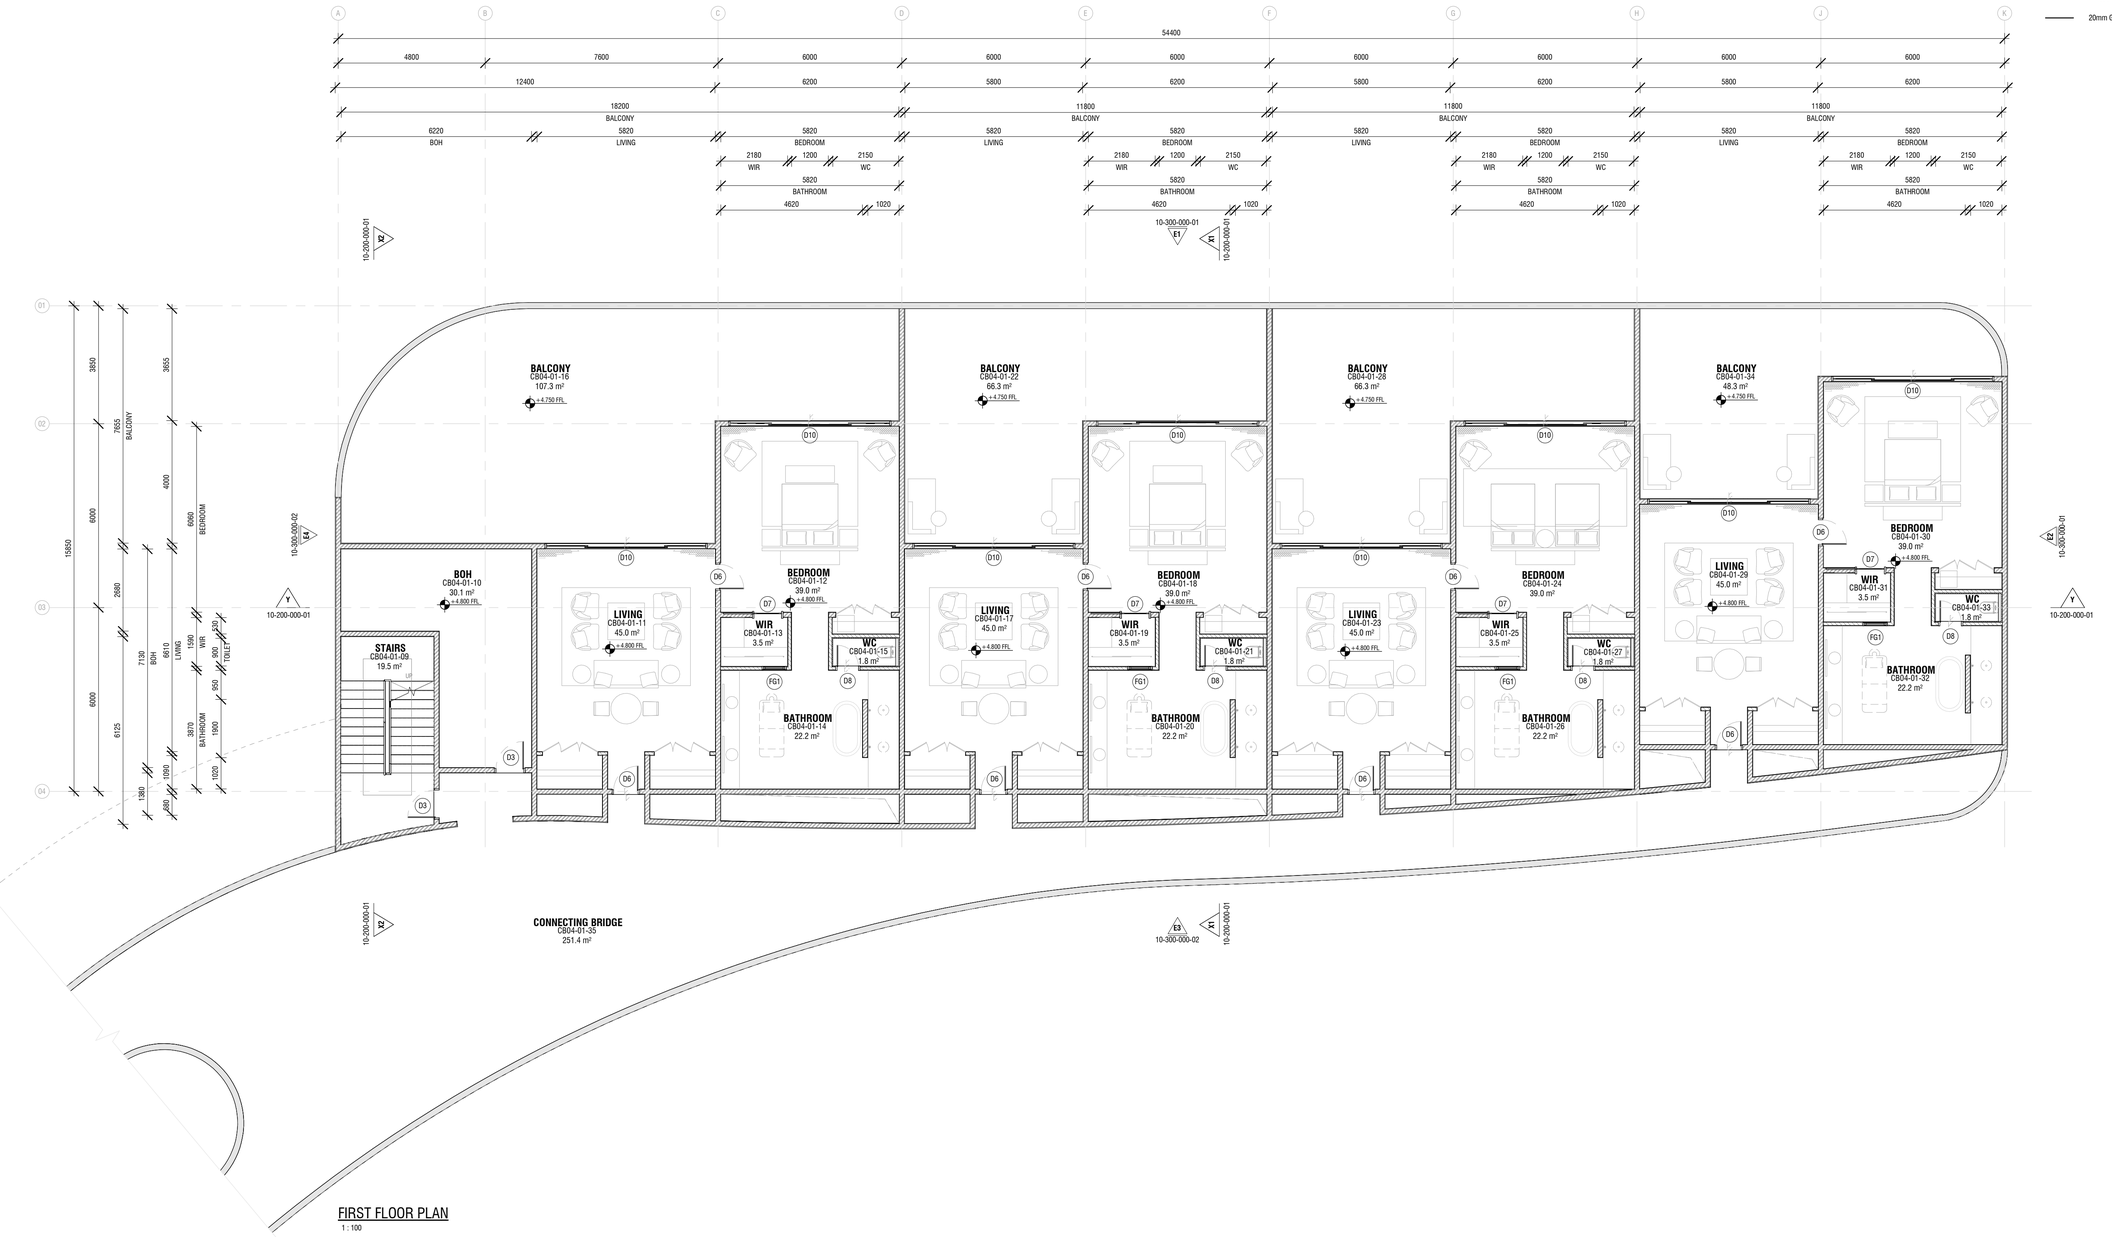

FIRST FLOOR PLAN

1 : 100

WALL LEGEND

- 150mm THICK SOLID BLOCK MASONRY WALL
- 100mm THICK SOLID BLOCK MASONRY WALL
- 150mm CONCRETE WALL / FILLINGS
- 20mm GLASS WALL

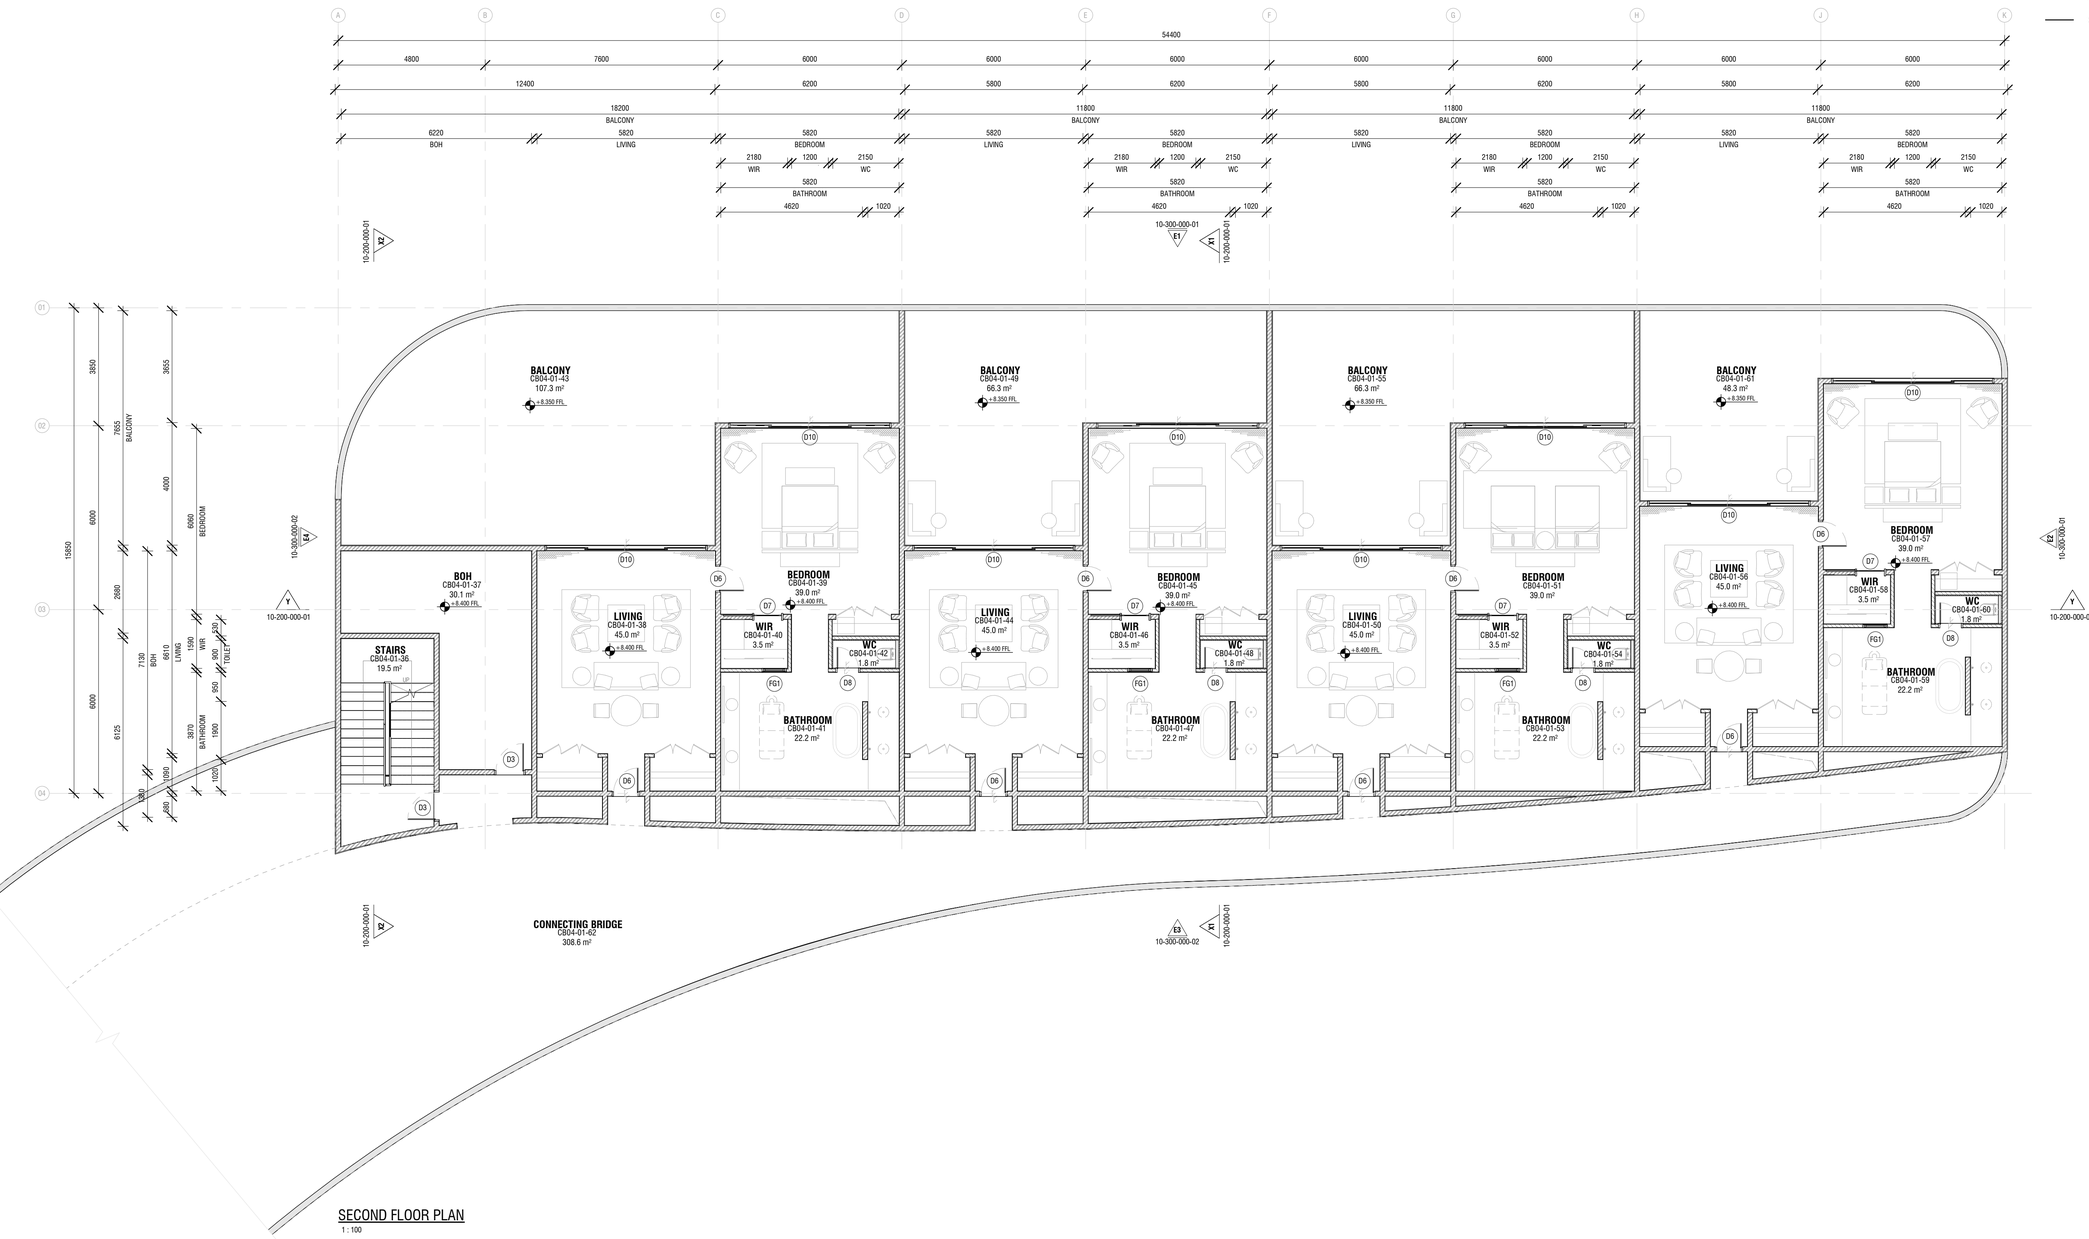

SECOND FLOOR PLAN

1 : 100

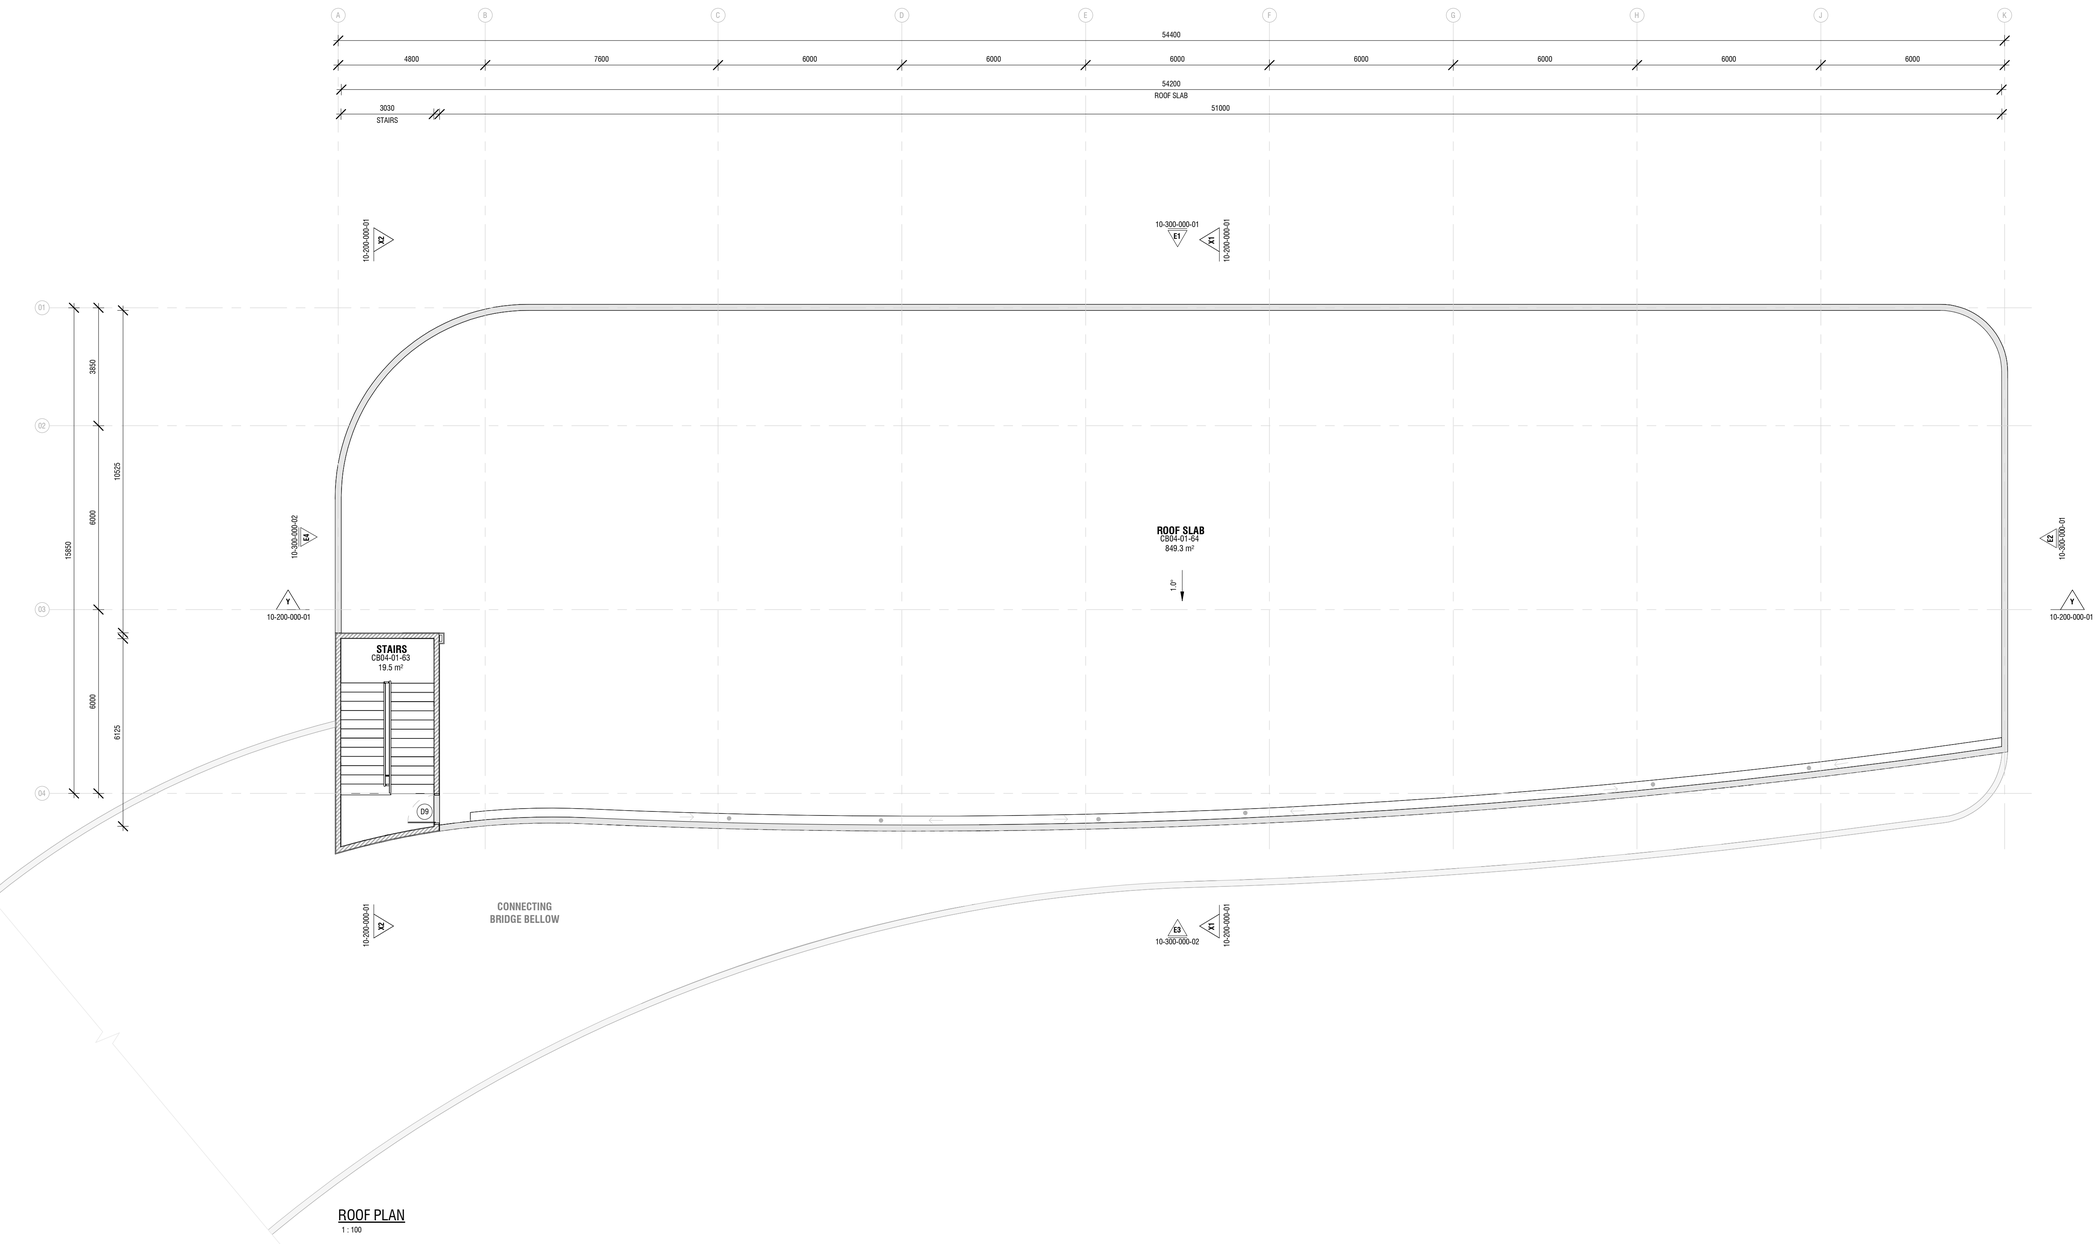

ROOF PLAN

1 : 100

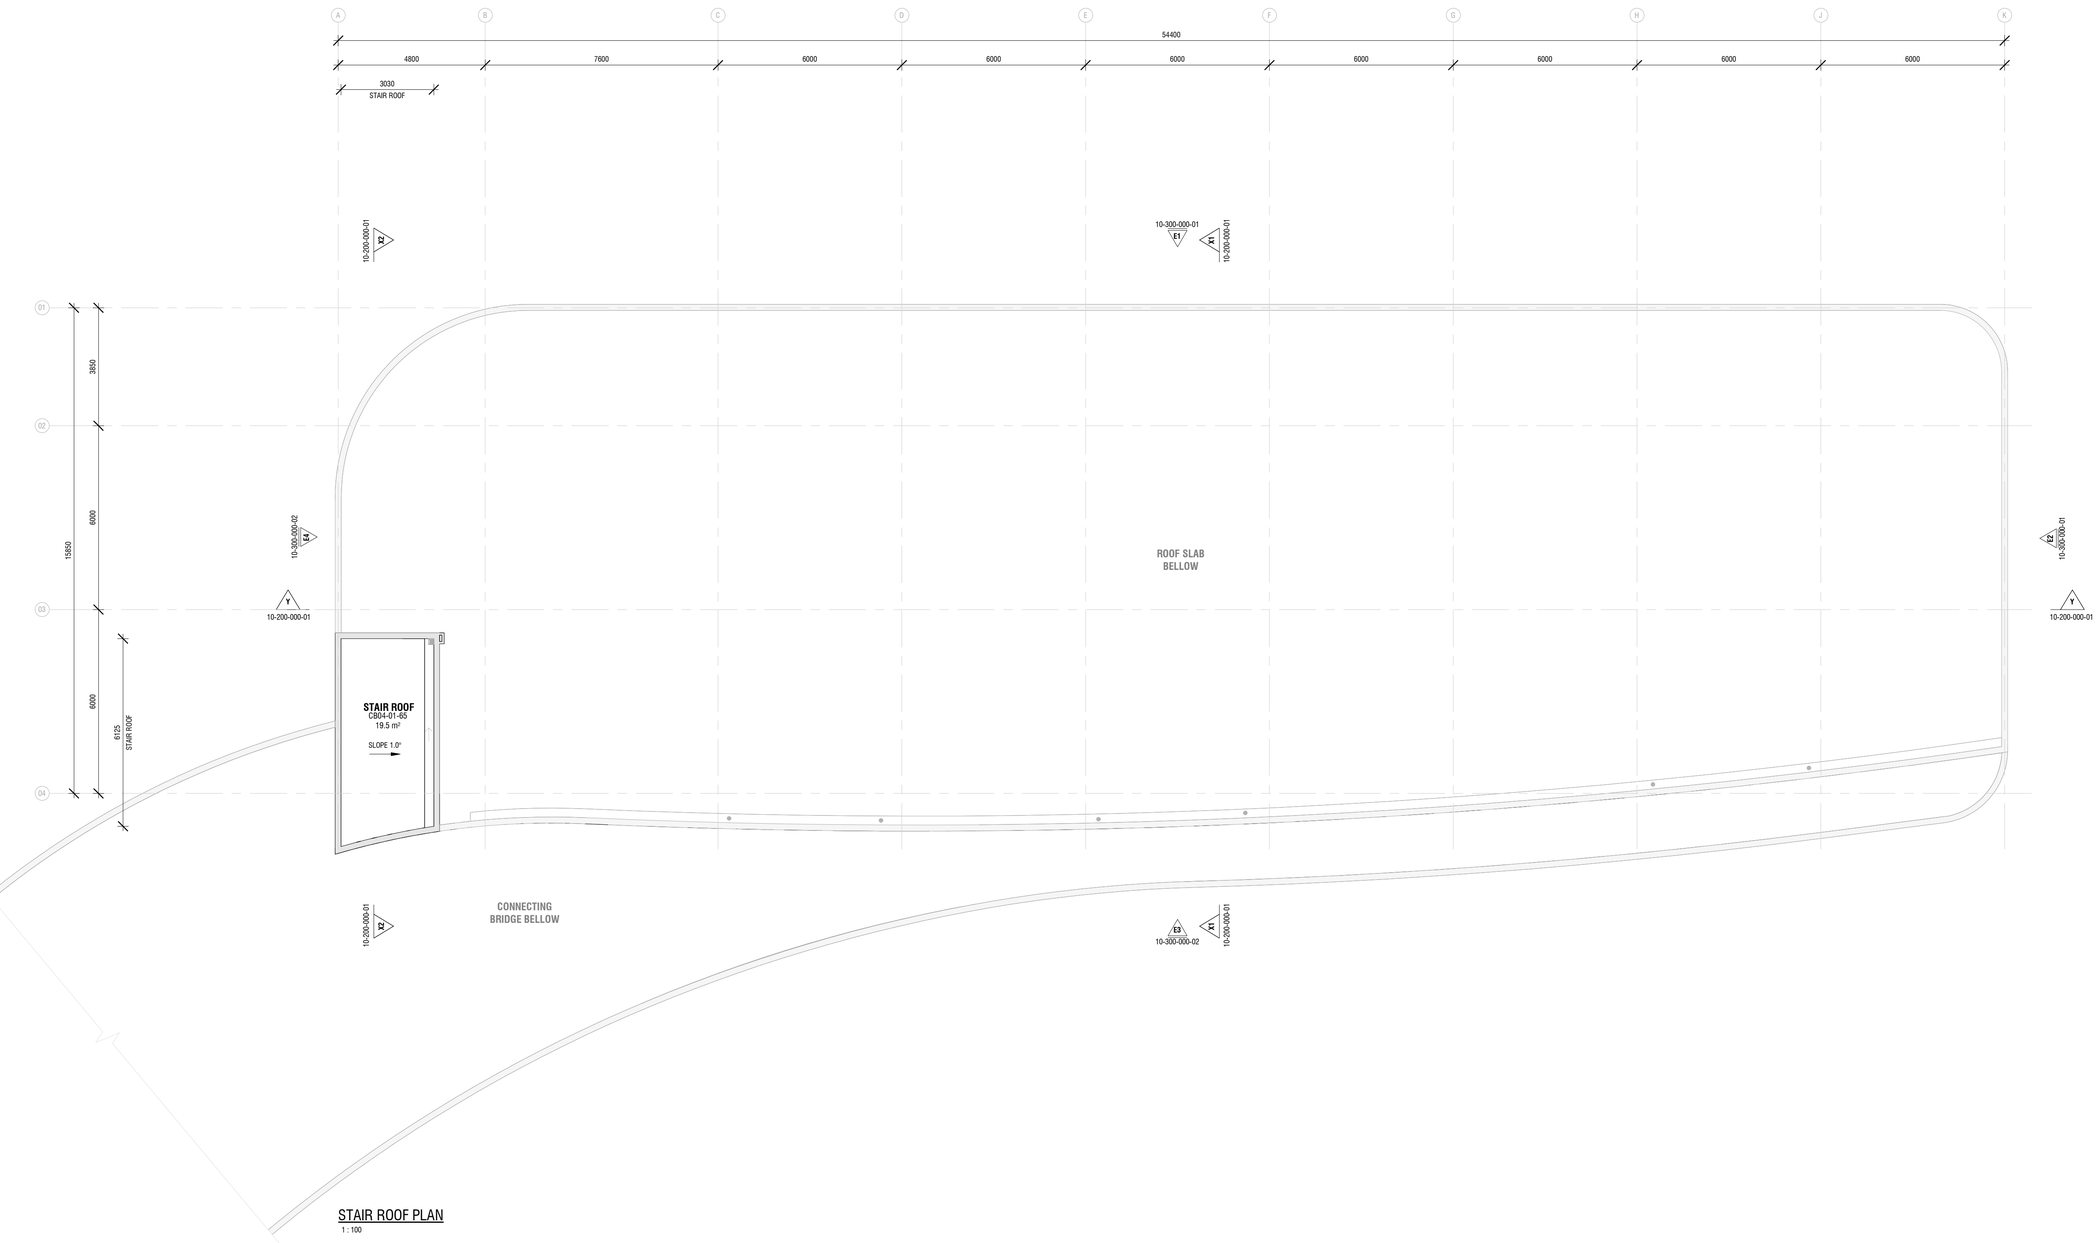

STAIR ROOF PLAN

1 : 100

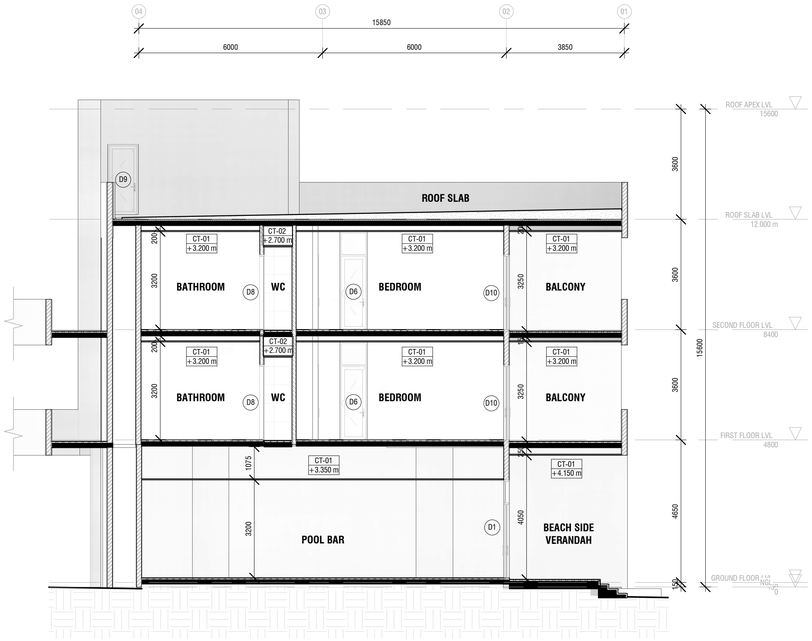

SECTION X1

1 : 100

SECTION X

1 : 100

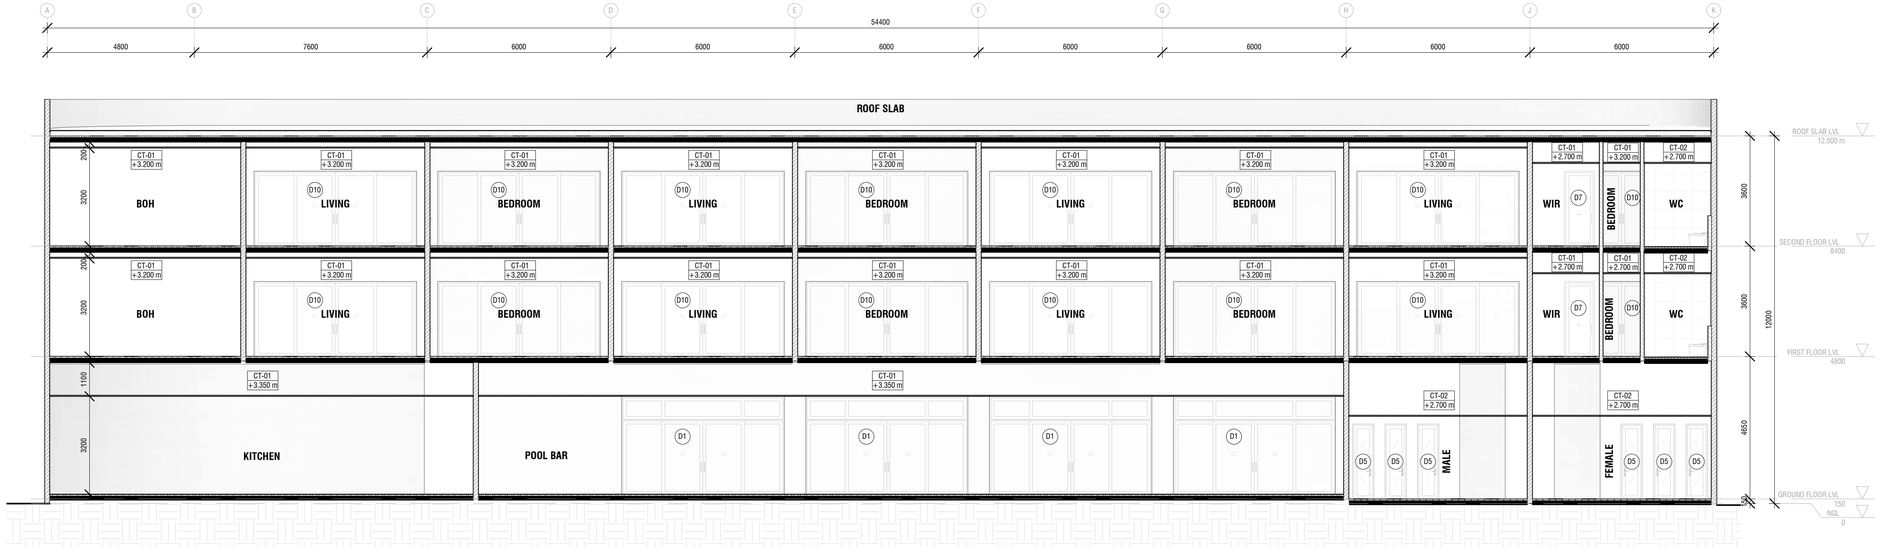

SECTION Y

1 : 100

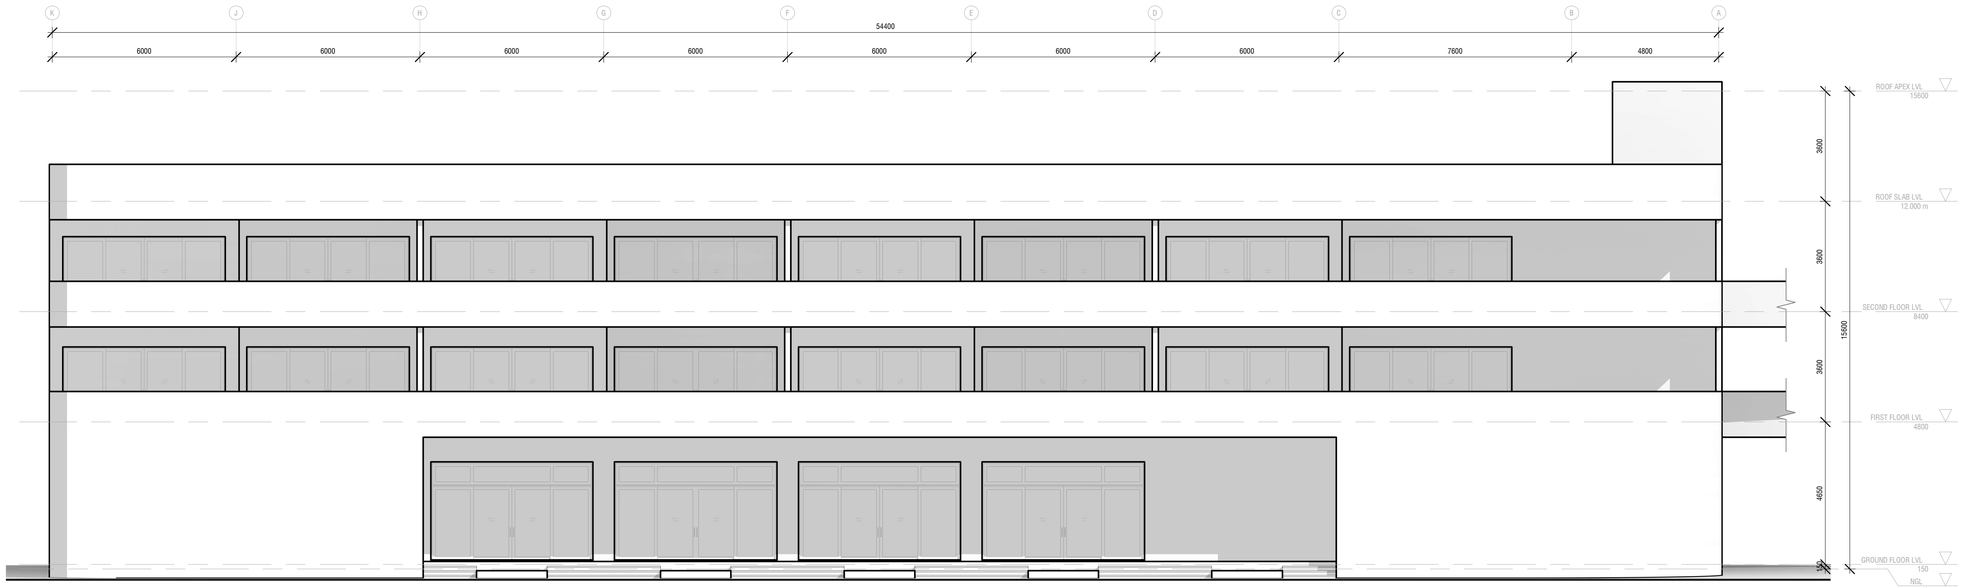

ELEVATION 01

1 : 100

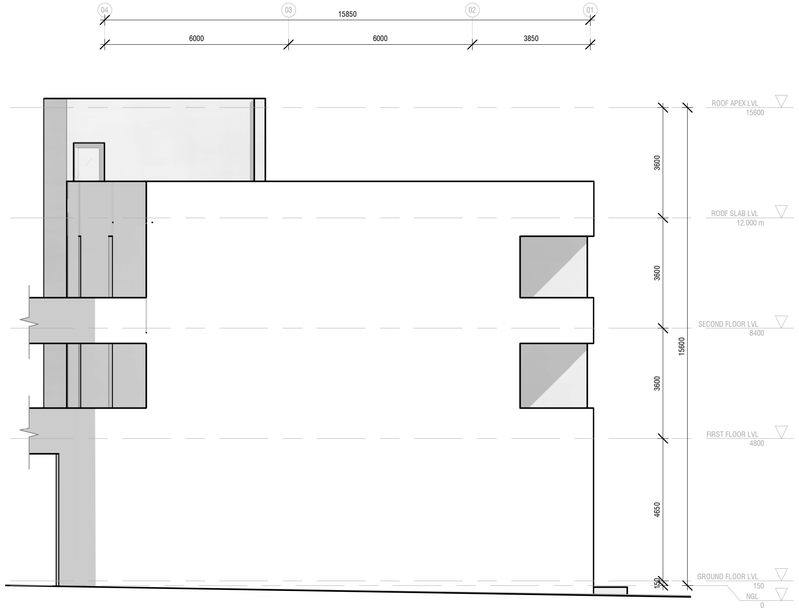

ELEVATION 02

1 : 100

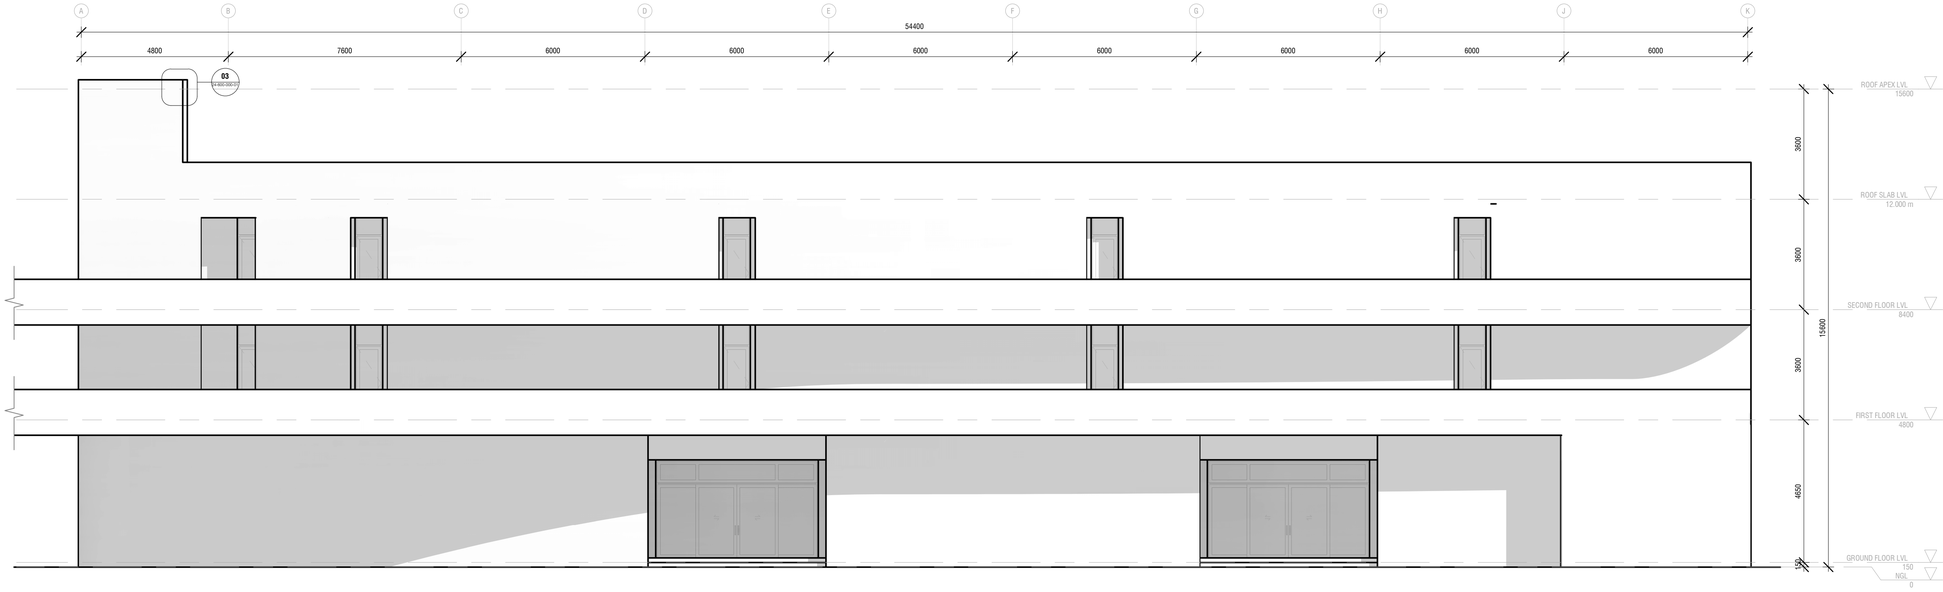

ELEVATION 03

1 : 100

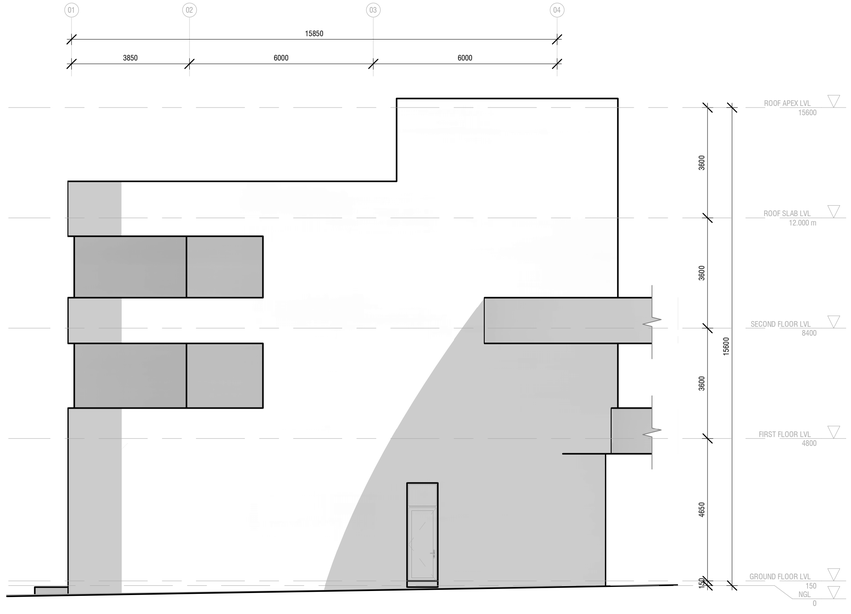

ELEVATION 04

1 : 100

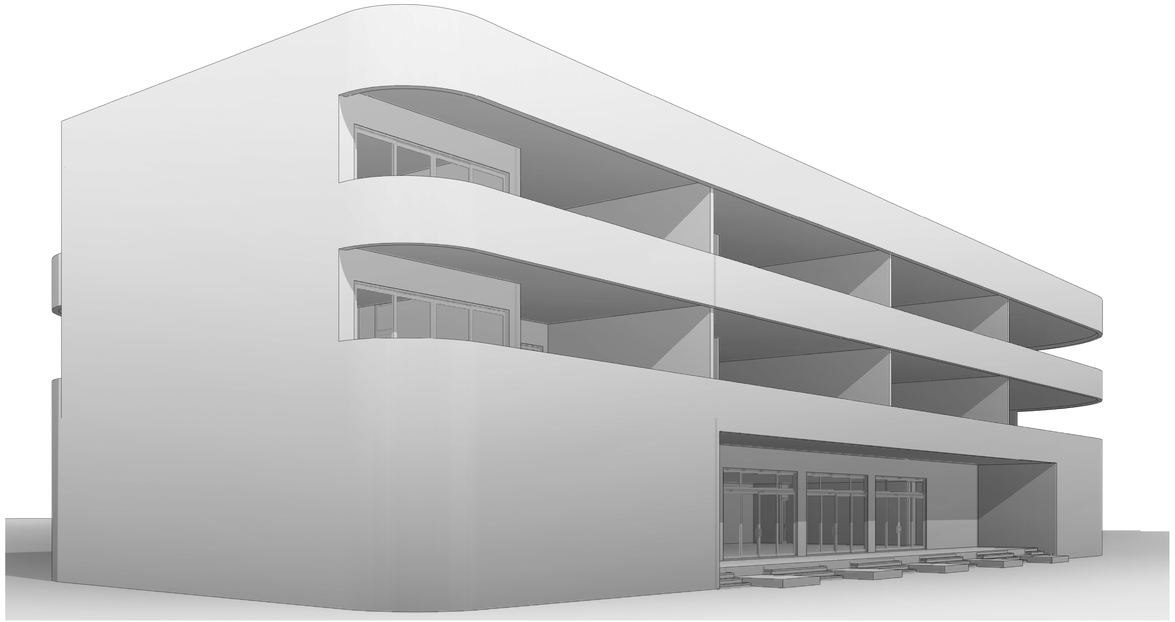

3D VIEW 01

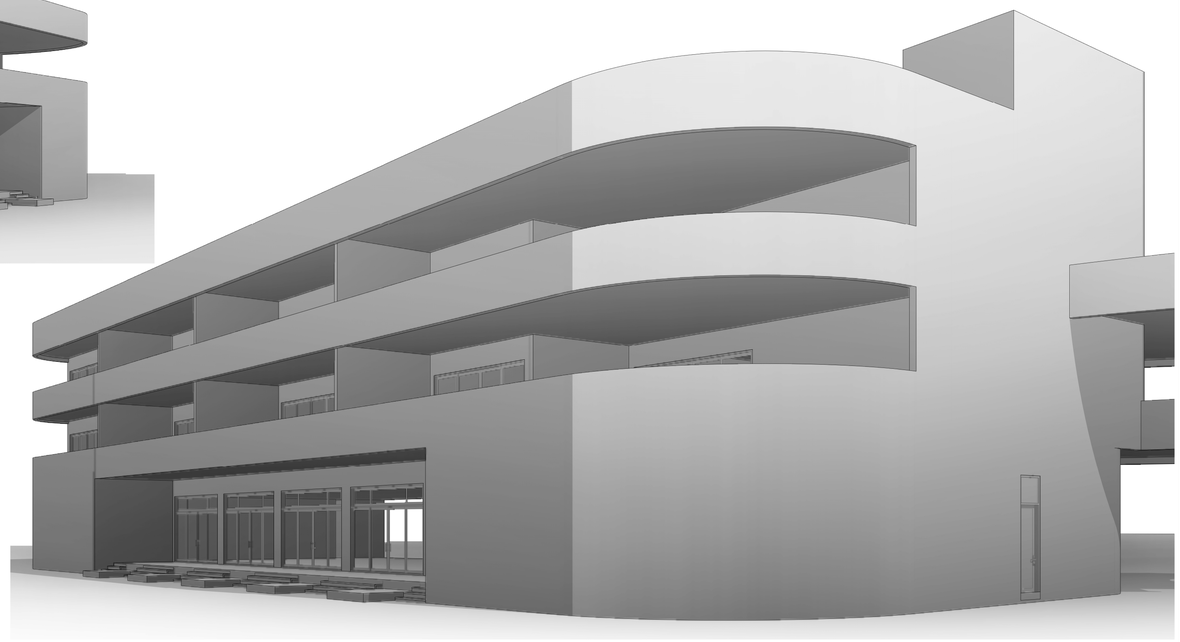

3D VIEW 02

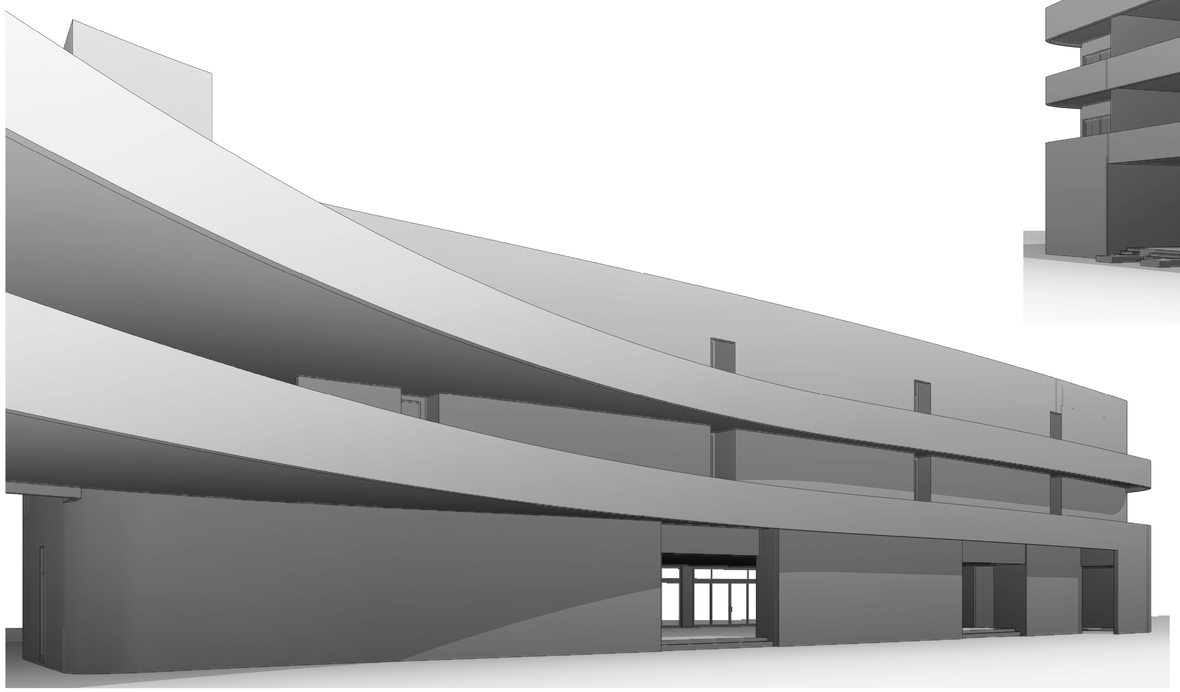

3D VIEW 03

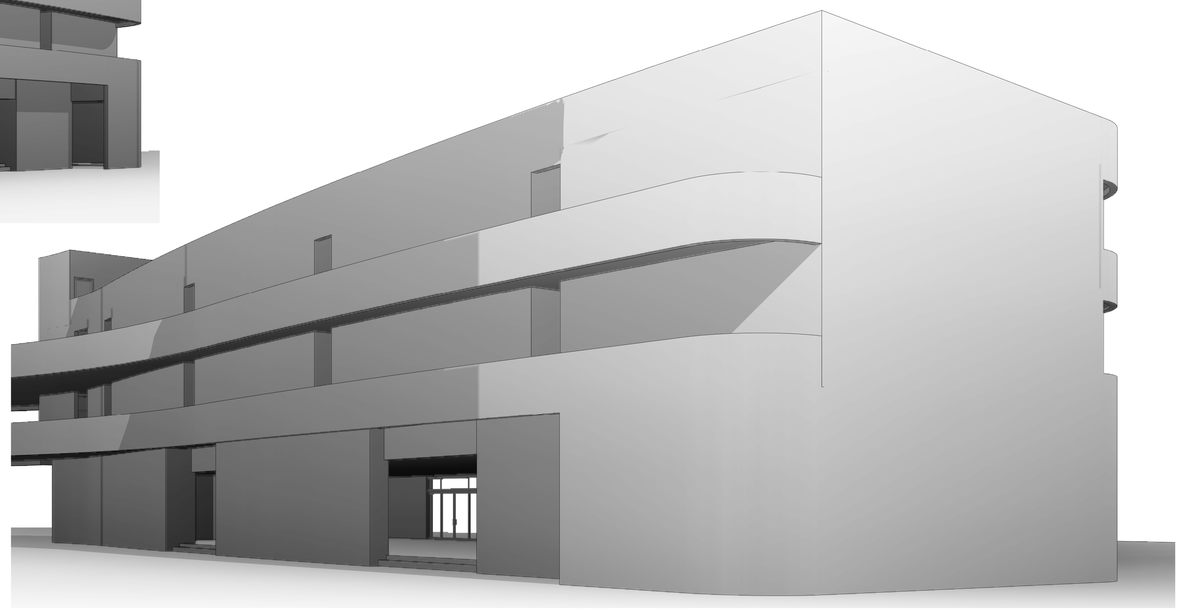

3D VIEW 04

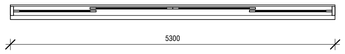

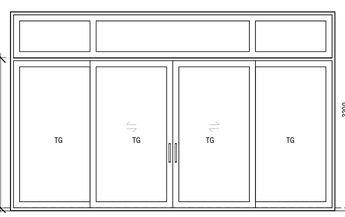

GENERAL	LOCATION	CB04 - POOL BAR		
	TAG	D1		
	WALL OPENING DIM.	5300x3200mm (W x H)	TYPE	4 PANEL SLIDING DOOR
	QUANTITY	04 NOS.	OPEN AREA	16.96 Sqm
FRAME	FRAME SIZE	50x150mm	MATERIAL	BY ID CONSULTANT
	FINISH			
DOOR PANEL	MATERIAL			
	FINISH			
	GLAZING			
	FIRE RATING			
	ACOUSTIC RATING			
IRONMONGERY	HINGES/ SLIDING GEAR			
	HANDLE			
	LOCK SET	BY ID CONSULTANT		
	DOOR VIEWER			
	DOOR CLOSER			
	SOFT CLOSING			
	FLUSH BOLTS			
	DOOR STOPPER			
	RUBBER SEAL			
	KICK PLATE			
	ACCESS CONTROL			

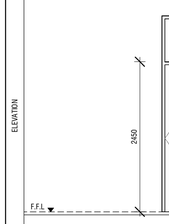

GENERAL	LOCATION	CB04 - KITCHEN		
	TAG	D2		
	WALL OPENING DIM.	1200x3200mm (W x H)	TYPE	2 PANEL SWING DOOR
	QUANTITY	02 NOS.	OPEN AREA	3.84 Sqm
FRAME	FRAME SIZE	50x150mm	MATERIAL	BY ID CONSULTANT
	FINISH			
DOOR PANEL	MATERIAL			
	FINISH			
	GLAZING			
	FIRE RATING			
	ACOUSTIC RATING			
IRONMONGERY	HINGES/ SLIDING GEAR			
	HANDLE			
	LOCK SET	BY ID CONSULTANT		
	DOOR VIEWER			
	DOOR CLOSER			
	SOFT CLOSING			
	FLUSH BOLTS			
	DOOR STOPPER			
	RUBBER SEAL			
	KICK PLATE			
	ACCESS CONTROL			

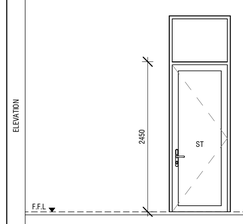

GENERAL	LOCATION	CB04 - STAIRS		
	TAG	D3		
	WALL OPENING DIM.	1000x3200mm (W x H)	TYPE	1 PANEL SWING DOOR
	QUANTITY	05 NOS.	OPEN AREA	3.20 Sqm
FRAME	FRAME SIZE	50x150mm	MATERIAL	BY ID CONSULTANT
	FINISH			
DOOR PANEL	MATERIAL			
	FINISH			
	GLAZING			
	FIRE RATING			
	ACOUSTIC RATING			
IRONMONGERY	HINGES/ SLIDING GEAR			
	HANDLE			
	LOCK SET	BY ID CONSULTANT		
	DOOR VIEWER			
	DOOR CLOSER			
	SOFT CLOSING			
	FLUSH BOLTS			
	DOOR STOPPER			
	RUBBER SEAL			
	KICK PLATE			
	ACCESS CONTROL			

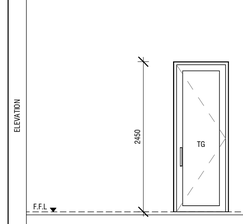

GENERAL	LOCATION	CB04 - MALE, FEMALE, ACC. TOILET		
	TAG	D4		
	WALL OPENING DIM.	900x2450mm (W x H)	TYPE	1 PANEL SWING DOOR
	QUANTITY	03 NOS.	OPEN AREA	2.21 Sqm
FRAME	FRAME SIZE	50x150mm	MATERIAL	BY ID CONSULTANT
	FINISH			
DOOR PANEL	MATERIAL			
	FINISH			
	GLAZING			
	FIRE RATING			
	ACOUSTIC RATING			
IRONMONGERY	HINGES/ SLIDING GEAR			
	HANDLE			
	LOCK SET	BY ID CONSULTANT		
	DOOR VIEWER			
	DOOR CLOSER			
	SOFT CLOSING			
	FLUSH BOLTS			
	DOOR STOPPER			
	RUBBER SEAL			
	KICK PLATE			
	ACCESS CONTROL			

LEGEND

TG - CLEAR GLASS
FTG - FIXED CLEAR GLASS
FG - FROSTED GLASS
FFG - FIXED FROSTED GLASS
RG - REFLECTED GLASS
FRG - FIXED REFLECTED GLASS
TG - TEMPERED CLEAR GLASS
AL - ALUMINUM LOUVERS
ST - SOLID TIMBER
T - TIMBER
PVC - POLYVINYL CHLORIDE
GS - GALVANIZED STEEL

NOTE

- ALL DOORS & WINDOWS TO BE CHECKED ON SITE BEFORE FABRICATION.
- ALL DOOR & WINDOWS VIEWED FROM EXTERIOR, FOR DOOR SWING, REFER TO FLOOR PLANS.
- INTERNAL DOORS FRAME DEPTH TO BE WIDTH OF THE WALL.
- THE DOORS / WINDOWS WHICH DO NOT TOUCH THE BEAM SHALL HAVE A LINTEL BEAM (LB) ABOVE THE DOOR / WINDOW.
- FOR ALL THE WINDOWS PUT A SILL BEAM BELOW THE WINDOW (SB)

DOOR SCHEDULE

No.	DESCRIPTION	WIDTH	HEIGHT	QTY
D1	4 Panel Sliding Door - Clear Glass Panel - Aluminum Frame	5300	3200	4
D2	2 Panel Swing Door - Solid Timber Panel - Solid Timber Frame	1200	3200	2
D3	1 Panel Swing Door - Solid Timber Panel - Solid Timber Frame	1000	3200	5
D4	1 Panel Swing Door - Solid Timber Panel - Solid Timber Frame	900	2450	3
D5	1 Panel Swing Door - Solid Timber Panel - Solid Timber Frame	700	2450	17
D6	1 Panel Swing Door - Solid Timber Panel - Solid Timber Frame	900	3200	16
D7	1 Panel Sliding Pocket Door - Frosted Glass Panel - Aluminum Frame	1000	2450	8
D8	1 Panel Swing Door - Solid Timber Panel - Solid Timber Frame	800	2450	8
D9	1 Panel Swing Door - Solid Timber Panel - Solid Timber Frame	1000	2300	1
D10	4 Panel Sliding Door - Clear Glass Panel - Aluminum Frame	5300	2450	16

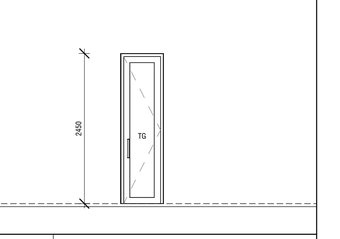

GENERAL	LOCATION	CB04 - WC, SHOWER		
	TAG	D5		
	WALL OPENING DIM.	700x2450mm (W x H)	TYPE	1 PANEL SWING DOOR
	QUANTITY	17 NOS.	OPEN AREA	1.72 Sqm
FRAME	FRAME SIZE	50x150mm	MATERIAL	BY ID CONSULTANT
	FINISH			
DOOR PANEL	MATERIAL			
	FINISH			
	GLAZING			
	FIRE RATING			
	ACOUSTIC RATING			
IRONMONGERY	HINGES/ SLIDING GEAR			
	HANDLE			
	LOCK SET	BY ID CONSULTANT		
	DOOR VIEWER			
	DOOR CLOSER			
	SOFT CLOSING			
	FLUSH BOLTS			
	DOOR STOPPER			
	RUBBER SEAL			
	KICK PLATE			
	ACCESS CONTROL			

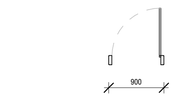

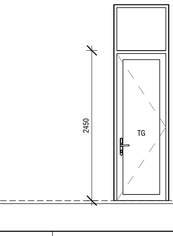

GENERAL	LOCATION	CB04 - LIVING, BEDROOM		
	TAG	D6		
	WALL OPENING DIM.	900x3200mm (W x H)	TYPE	1 PANEL SWING DOOR
	QUANTITY	16 NOS.	OPEN AREA	2.88 Sqm
FRAME	FRAME SIZE	50x150mm	MATERIAL	BY ID CONSULTANT
	FINISH			
DOOR PANEL	MATERIAL			
	FINISH			
	GLAZING			
	FIRE RATING			
	ACOUSTIC RATING			
IRONMONGERY	HINGES/ SLIDING GEAR			
	HANDLE			
	LOCK SET	BY ID CONSULTANT		
	DOOR VIEWER			
	DOOR CLOSER			
	SOFT CLOSING			
	FLUSH BOLTS			
	DOOR STOPPER			
	RUBBER SEAL			
	KICK PLATE			
	ACCESS CONTROL			

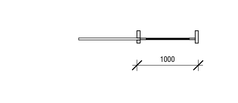

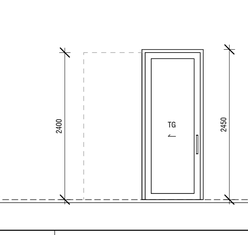

GENERAL	LOCATION	CB04 - WIR		
	TAG	D7		
	WALL OPENING DIM.	1000x2450mm (W x H)	TYPE	1 PANEL SWING DOOR
	QUANTITY	08 NOS.	OPEN AREA	2.45 Sqm
FRAME	FRAME SIZE	50x150mm	MATERIAL	BY ID CONSULTANT
	FINISH			
DOOR PANEL	MATERIAL			
	FINISH			
	GLAZING			
	FIRE RATING			
	ACOUSTIC RATING			
IRONMONGERY	HINGES/ SLIDING GEAR			
	HANDLE			
	LOCK SET	BY ID CONSULTANT		
	DOOR VIEWER			
	DOOR CLOSER			
	SOFT CLOSING			
	FLUSH BOLTS			
	DOOR STOPPER			
	RUBBER SEAL			
	KICK PLATE			
	ACCESS CONTROL			

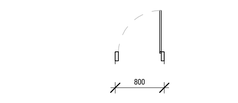

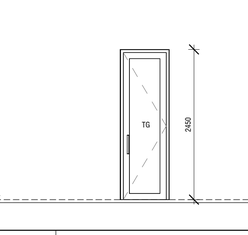

GENERAL	LOCATION	CB04 - WC AT FIRST FLOOR & SECOND FLOOR		
	TAG	D8		
	WALL OPENING DIM.	800x2450mm (W x H)	TYPE	1 PANEL SWING DOOR
	QUANTITY	08 NOS.	OPEN AREA	1.96 Sqm
FRAME	FRAME SIZE	50x150mm	MATERIAL	BY ID CONSULTANT
	FINISH			
DOOR PANEL	MATERIAL			
	FINISH			
	GLAZING			
	FIRE RATING			
	ACOUSTIC RATING			
IRONMONGERY	HINGES/ SLIDING GEAR			
	HANDLE			
	LOCK SET	BY ID CONSULTANT		
	DOOR VIEWER			
	DOOR CLOSER			
	SOFT CLOSING			
	FLUSH BOLTS			
	DOOR STOPPER			
	RUBBER SEAL			
	KICK PLATE			
	ACCESS CONTROL			

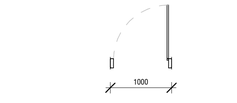

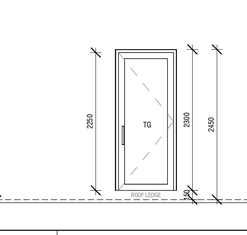

GENERAL	LOCATION	CB04 - STAIRS AT ROOF		
	TAG	D9		
	WALL OPENING DIM.	1000x2300mm (W x H)	TYPE	1 PANEL SWING DOOR
	QUANTITY	01 NOS.	OPEN AREA	2.30 Sqm
FRAME	FRAME SIZE	50x150mm	MATERIAL	BY ID CONSULTANT
	FINISH			
DOOR PANEL	MATERIAL			
	FINISH			
	GLAZING			
	FIRE RATING			
	ACOUSTIC RATING			
IRONMONGERY	HINGES/ SLIDING GEAR			
	HANDLE			
	LOCK SET	BY ID CONSULTANT		
	DOOR VIEWER			
	DOOR CLOSER			
	SOFT CLOSING			
	FLUSH BOLTS			
	DOOR STOPPER			
	RUBBER SEAL			
	KICK PLATE			
	ACCESS CONTROL			

DOOR SCHEDULE 01

1 : 50

PLAN

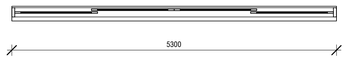

ELEVATION

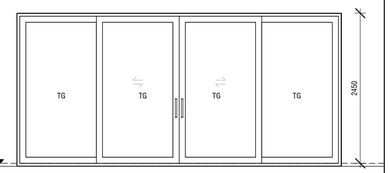

GENERAL	LOCATION	CB04 - LIVING, BEDROOM		
	TAG	D10		
	WALL OPENING DIM.	5300x2450mm (W x H)	TYPE	4 PANEL SLIDING DOOR
	QUANTITY	16 NOS.	OPEN AREA	12.99 Sqm
FRAME	FRAME SIZE	50x150mm	MATERIAL	BY ID CONSULTANT
	FINISH			
DOOR PANEL	MATERIAL			
	FINISH			
	GLAZING			
	FIRE RATING			
	ACOUSTIC RATING			
IRONMONGERY	HINGES/ SLIDING GEAR			
	HANDLE			
	LOCK SET	BY ID CONSULTANT		
	DOOR VIEWER			
	DOOR CLOSER			
	SOFT CLOSING			
	FLUSH BOLTS			
	DOOR STOPPER			
	RUBBER SEAL			
	KICK PLATE			
	ACCESS CONTROL			

DOOR SCHEDULE 02

1 : 50

LEGEND

TG - CLEAR GLASS
FTG - FIXED CLEAR GLASS
FG - FROSTED GLASS
FFG - FIXED FROSTED GLASS
RG - REFLECTED GLASS
FRG - FIXED REFLECTED GLASS
TG - TEMPERED CLEAR GLASS
AL - ALUMINUM LOUVERS
ST - SOLID TIMBER
T - TIMBER
PVC - POLYVINYL CHLORIDE
GS - GALVANIZED STEEL

NOTE

- ALL DOORS & WINDOWS TO BE CHECKED ON SITE BEFORE FABRICATION.
- ALL DOOR & WINDOWS VIEWED FROM EXTERIOR, FOR DOOR SWING, REFER TO FLOOR PLANS.
- INTERNAL DOORS FRAME DEPTH TO BE WIDTH OF THE WALL.
- THE DOORS / WINDOWS WHICH DO NOT TOUCH THE BEAM SHALL HAVE A LINTEL BEAM (LB) ABOVE THE DOOR / WINDOW.
- FOR ALL THE WINDOWS PUT A SILL BEAM BELOW THE WINDOW (SB)

DOOR SCHEDULE

No.	DESCRIPTION	WIDTH	HEIGHT	QTY
D1	4 Panel Sliding Door - Clear Glass Panel - Aluminum Frame	5300	3200	4
D2	2 Panel Swing Door - Solid Timber Panel - Solid Timber Frame	1200	3200	2
D3	1 Panel Swing Door - Solid Timber Panel - Solid Timber Frame	1000	3200	5
D4	1 Panel Swing Door - Solid Timber Panel - Solid Timber Frame	900	2450	3
D5	1 Panel Swing Door - Solid Timber Panel - Solid Timber Frame	700	2450	17
D6	1 Panel Swing Door - Solid Timber Panel - Solid Timber Frame	900	3200	16
D7	1 Panel Sliding Pocket Door - Frosted Glass Panel - Aluminum Frame	1000	2450	8
D8	1 Panel Swing Door - Solid Timber Panel - Solid Timber Frame	800	2450	8
D9	1 Panel Swing Door - Solid Timber Panel - Solid Timber Frame	1000	2300	1
D10	4 Panel Sliding Door - Clear Glass Panel - Aluminum Frame	5300	2450	16

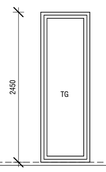

GENERAL	LOCATION	CB04 - WIR		
	TAG	FG1		
	WALL OPENING DIM.	800x2450mm (W x H)	TYPE	BY ID CONSULTANT
	QUANTITY	08 NOS.	OPEN AREA	1.96 Sqm
FRAME	FRAME SIZE	50x100mm	MATERIAL	BY ID CONSULTANT
	FINISH	BY ID CONSULTANT		
WINDOW PANEL	MATERIAL			
	FINISH			
	GLAZING			
	FIRE RATING			
	ACOUSTIC RATING			
IRONMONGERY	HINGES/ SLIDING GEAR			
	HANDLE			
	LOCK			
	FLUSH BOLTS			
	SHADING CANOPY			

WINDOW SCHEDULE

1 : 50

LEGEND

TG - CLEAR GLASS
FTG - FIXED CLEAR GLASS
FG - FROSTED GLASS
FFG - FIXED FROSTED GLASS
RG - REFLECTED GLASS
FRG - FIXED REFLECTED GLASS
TG - TEMPERED CLEAR GLASS
AL - ALUMINUM LOUVERS
ST - SOLID TIMBER
T - TIMBER
PVC - POLYVINYL CHLORIDE
GS - GALVANIZED STEEL

NOTE

- ALL DOORS & WINDOWS TO BE CHECKED ON SITE BEFORE FABRICATION.
- ALL DOOR & WINDOWS VIEWED FROM EXTERIOR, FOR DOOR SWING, REFER TO FLOOR PLANS.
- INTERNAL DOORS FRAME DEPTH TO BE WIDTH OF THE WALL.
- THE DOORS / WINDOWS WHICH DO NOT TOUCH THE BEAM SHALL HAVE A LINTEL BEAM (LB) ABOVE THE DOOR / WINDOW.
- FOR ALL THE WINDOWS PUT A SILL BEAM BELOW THE WINDOW (SB)

WINDOW SCHEDULE

NO	DESCRIPTION	WIDTH	HEIGHT	QTY
FG1	1 Panel Window - Fixed Panel - Aluminum Frame	800	2450	8

LEGEND

CT-01 9MM THICK MOISTURE RESISTANT GYPSUM CEILING WITH ALUMINIUM FRAMING CHANNELS. GROUND SMOOTH AND COMPLETE WITH SELECTED PAINT FINISH.

CT-02 6MM THICK CEMENT BOARD CEILING WITH ALUMINIUM FRAMING CHANNEL. GROUND SMOOTH AND COMPLETE WITH SELECTED PAINT FINISH.

CT-XX / X.XX m — CEILING TYPE / CEILING LEVEL

NOTE: ANY UNIDENTIFIED AREAS TO HAVE EXPOSED SLAB SOFFIT (B-CF-C00) TO BE GROUND SMOOTH IN SELECT PAINT FINISH (ONE COAT OF PUTTY FOLLOWED BY SEALER AND 2 COATS OF PAINT)

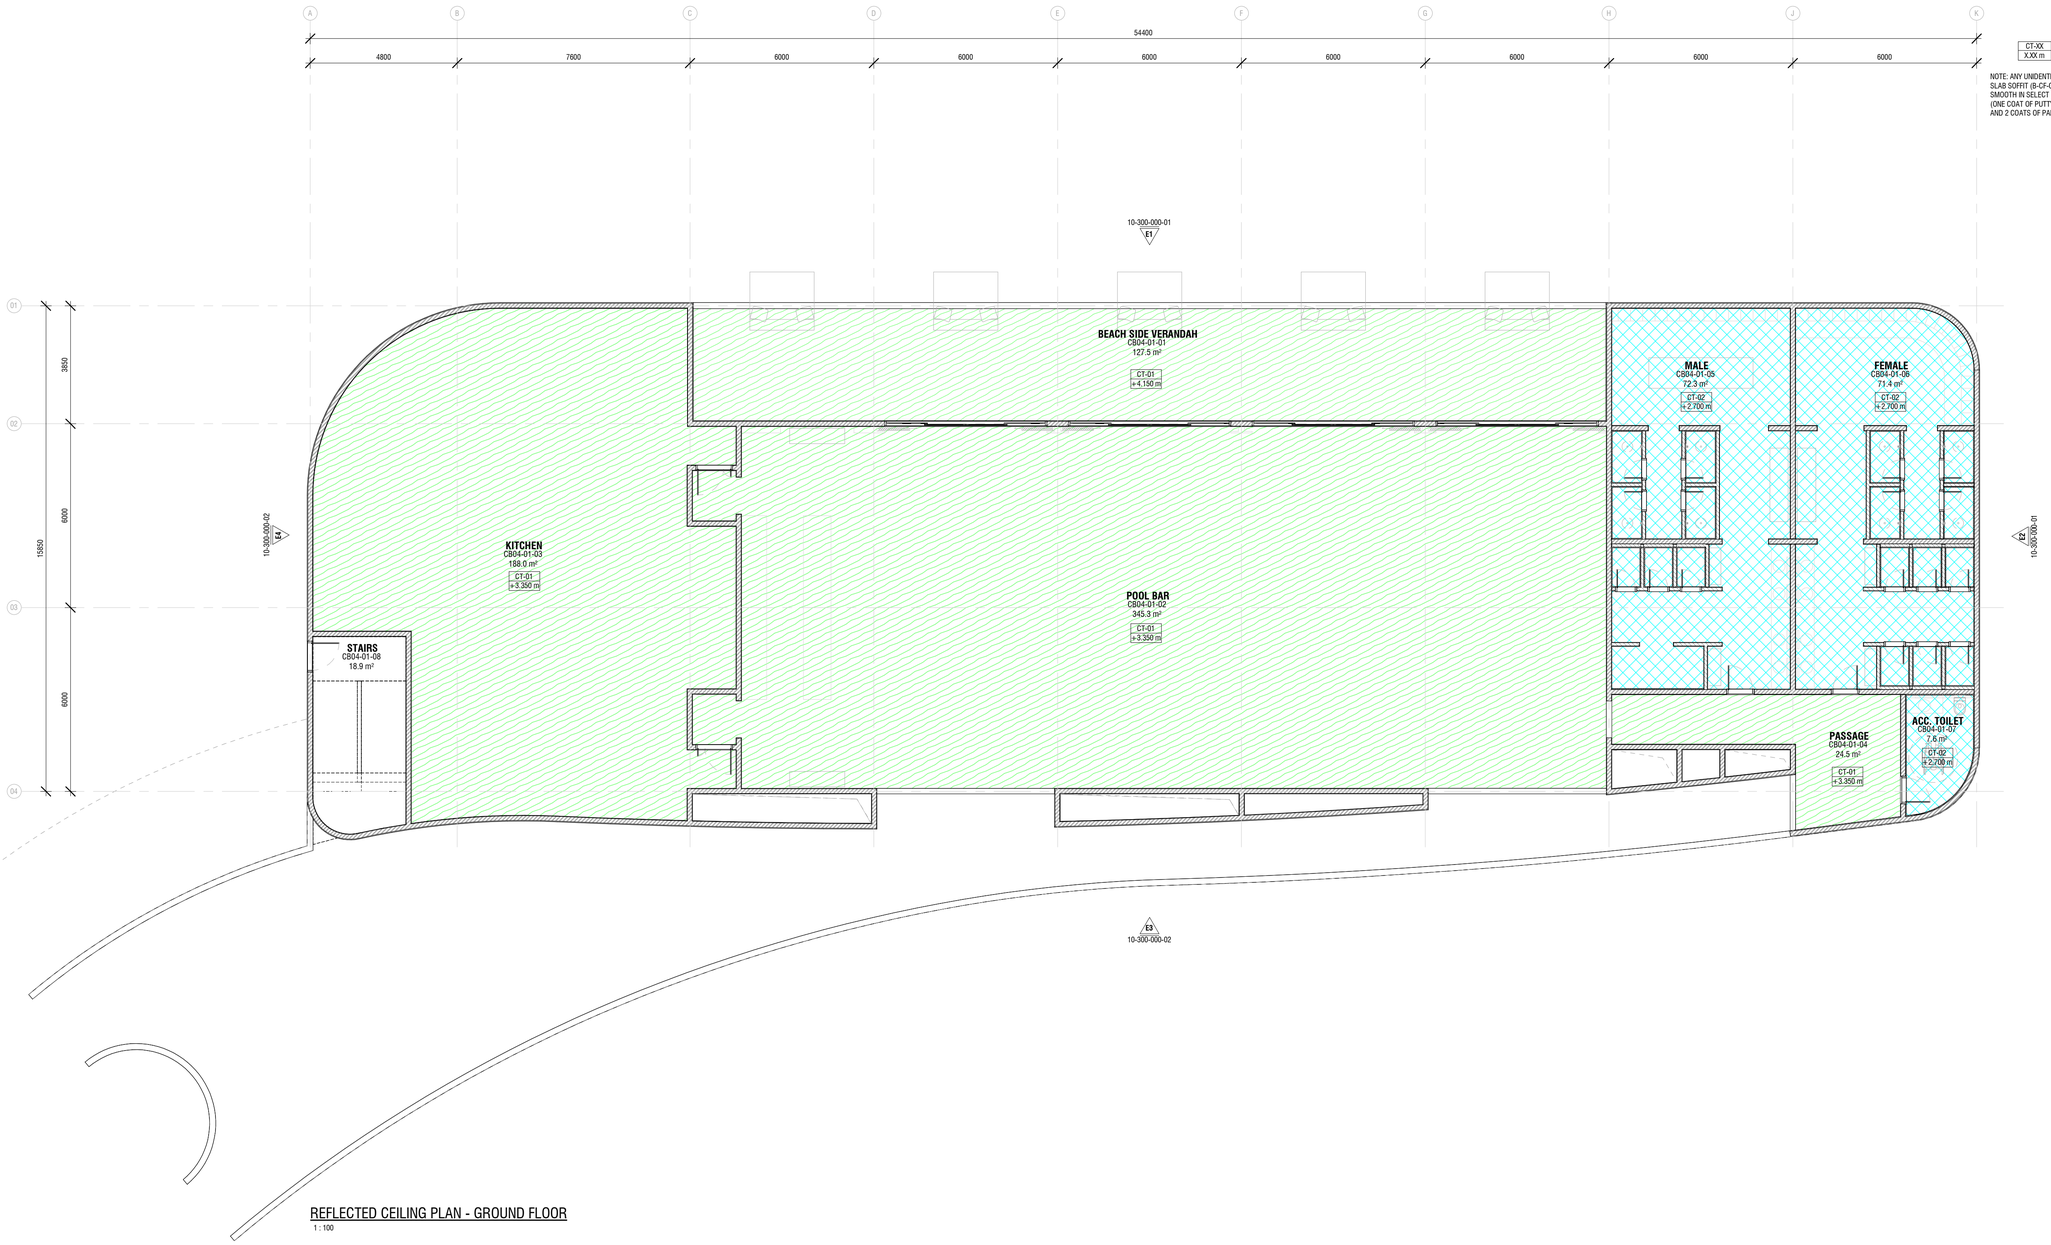

REFLECTED CEILING PLAN - GROUND FLOOR

1 : 100

LEGEND

CT-01		9MM THICK MOISTURE RESISTANT GYPSUM CEILING WITH ALUMINIUM FRAMING CHANNELS. GROUND SMOOTH AND COMPLETE WITH SELECTED PAINT FINISH.
CT-02		6MM THICK CEMENT BOARD CEILING WITH ALUMINIUM FRAMING CHANNEL. GROUND SMOOTH AND COMPLETE WITH SELECTED PAINT FINISH.

CT-XX / X.XX m — CEILING TYPE / CEILING LEVEL

NOTE: ANY UNIDENTIFIED AREAS TO HAVE EXPOSED SLAB SOFFIT (B-CF-C00) TO BE GROUND SMOOTH IN SELECT PAINT FINISH (ONE COAT OF PUTTY FOLLOWED BY SEALER AND 2 COATS OF PAINT)

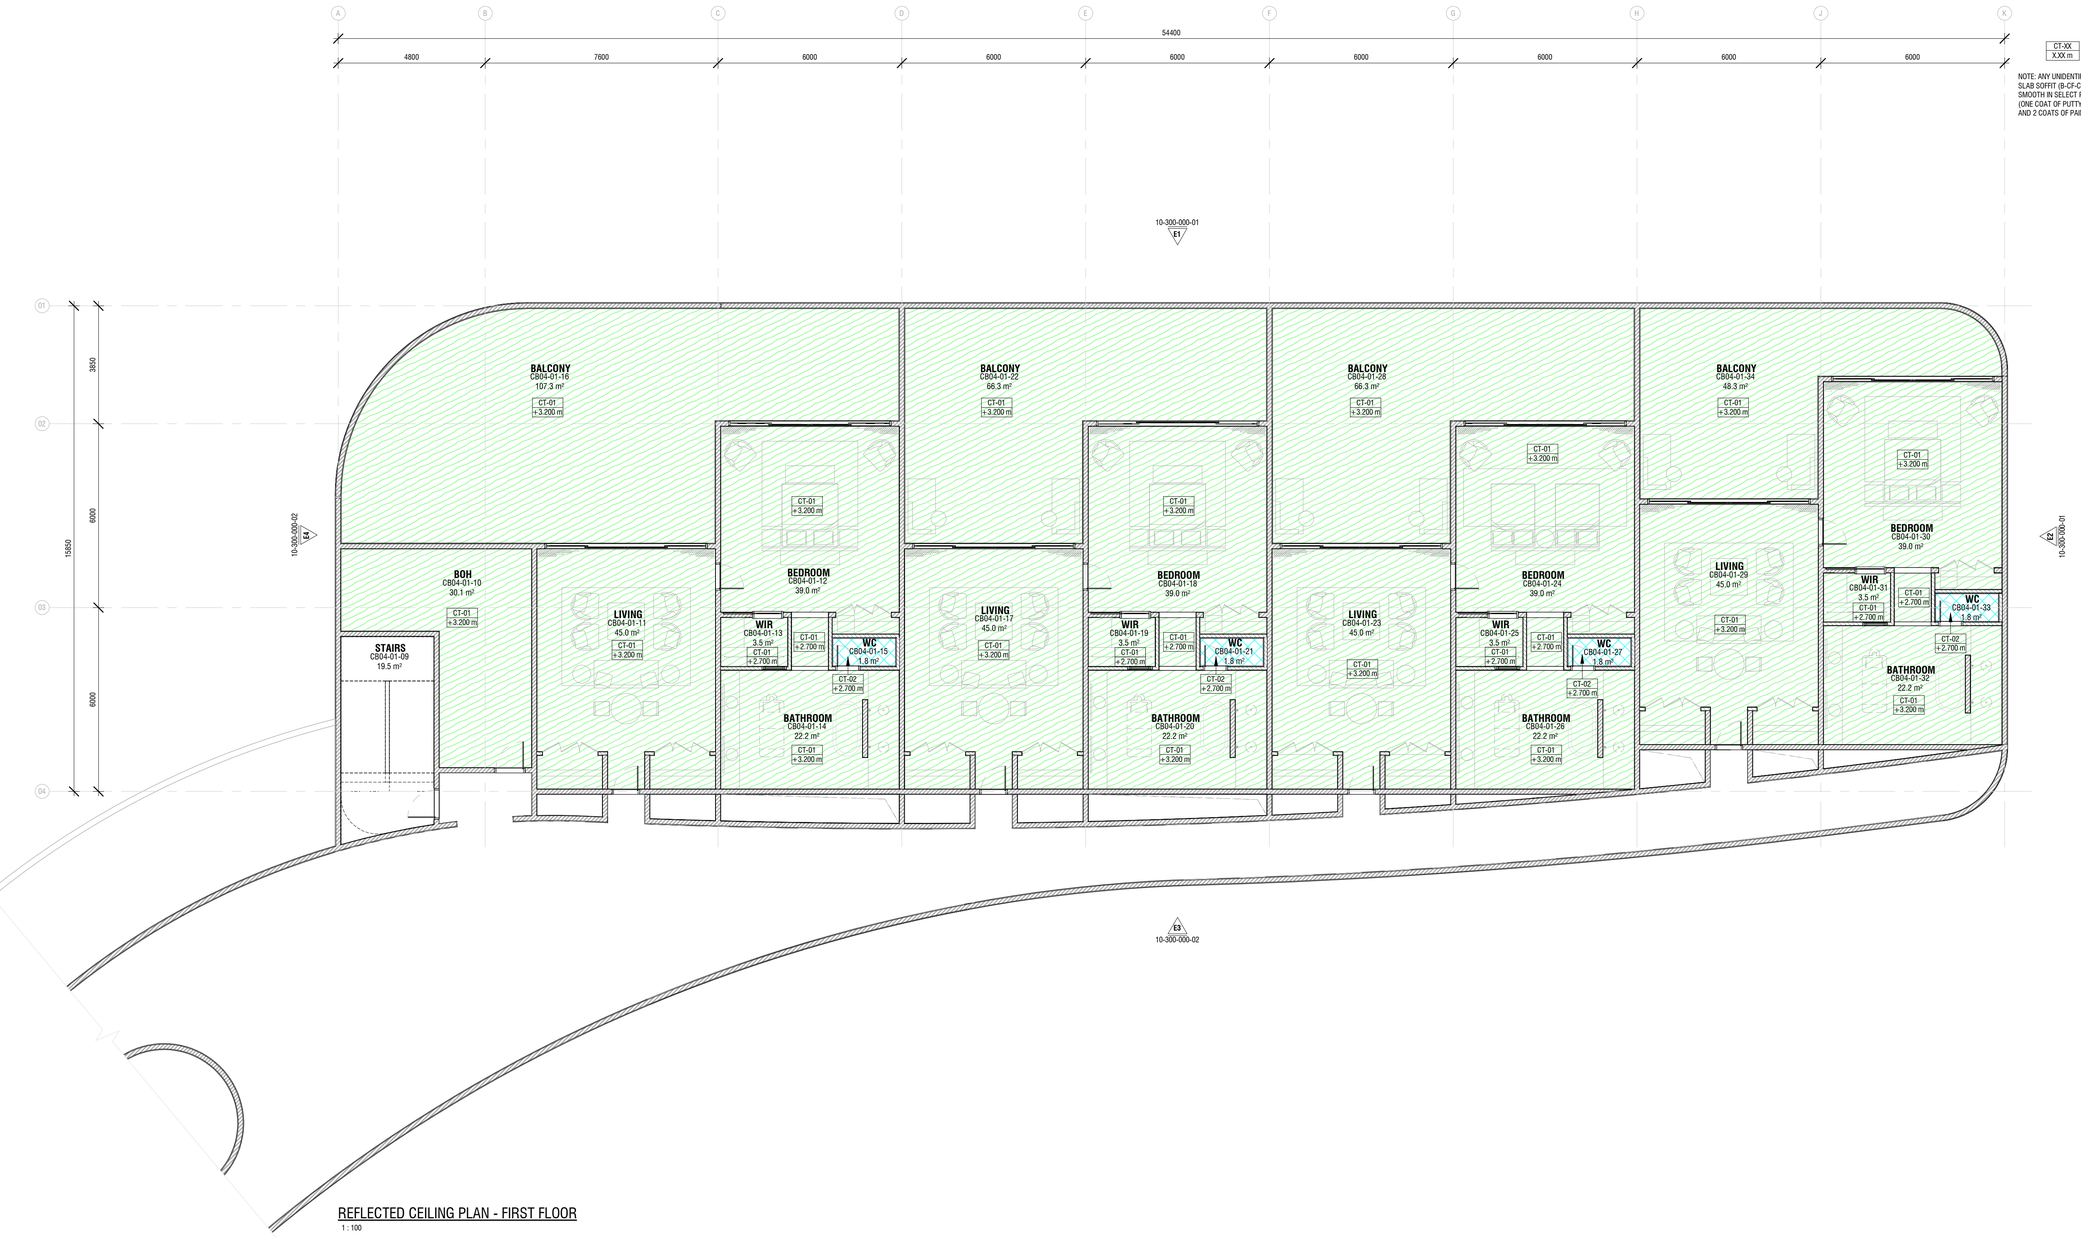

REFLECTED CEILING PLAN - FIRST FLOOR

1 : 100

LEGEND

CT-01 9MM THICK MOISTURE RESISTANT GYPSUM CEILING WITH ALUMINIUM FRAMING CHANNELS. GROUND SMOOTH AND COMPLETE WITH SELECTED PAINT FINISH.

CT-02 6MM THICK CEMENT BOARD CEILING WITH ALUMINIUM FRAMING CHANNEL. GROUND SMOOTH AND COMPLETE WITH SELECTED PAINT FINISH.

CT-XX / X.XX m — CEILING TYPE / CEILING LEVEL

NOTE: ANY UNIDENTIFIED AREAS TO HAVE EXPOSED SLAB SOFFIT (B-CF-C00) TO BE GROUND SMOOTH IN SELECT PAINT FINISH (ONE COAT OF PUTTY FOLLOWED BY SEALER AND 2 COATS OF PAINT)

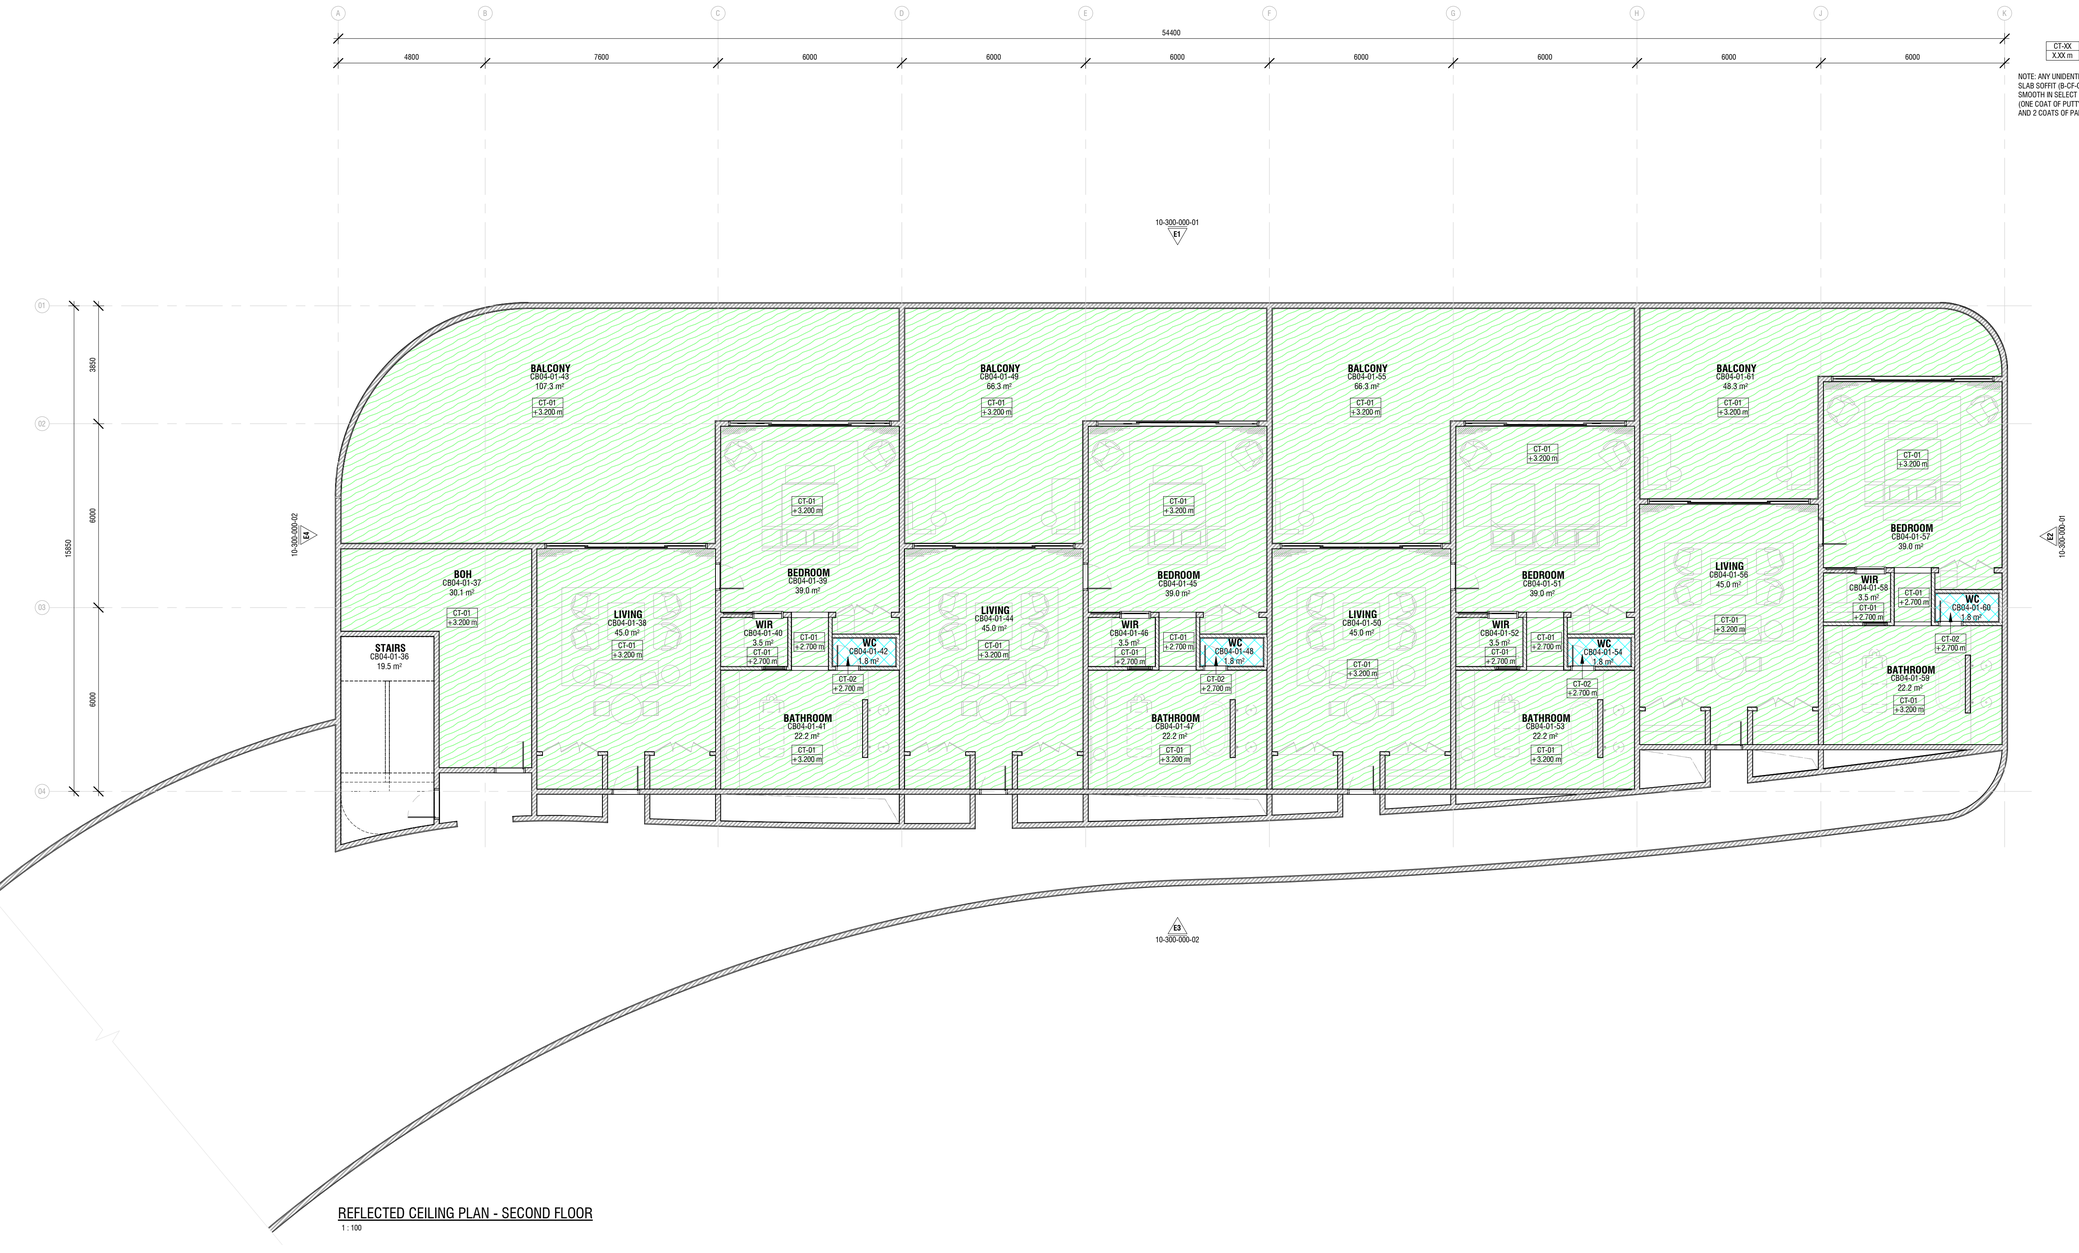

REFLECTED CEILING PLAN - SECOND FLOOR

1 : 100

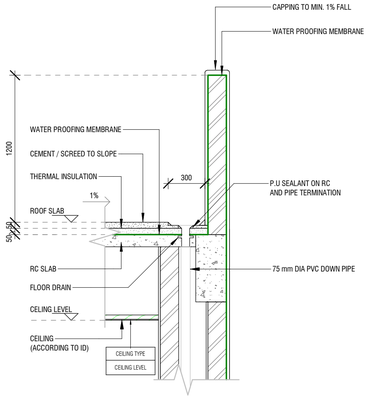

TYPICAL ROOF & FLOOR DRAIN DETAIL - 02

1 : 25

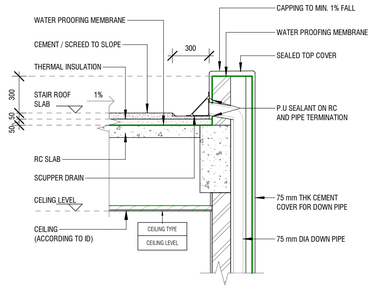

STAIR ROOF SCUPPER DRAIN DETAIL - 03

1 : 25

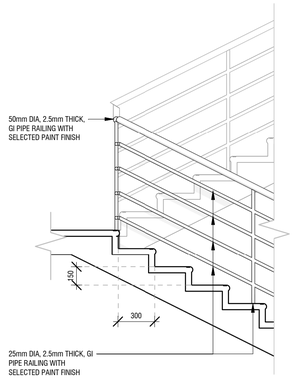

TYPICAL STAIR & HANDRAIL DETAIL - 04

1 : 25

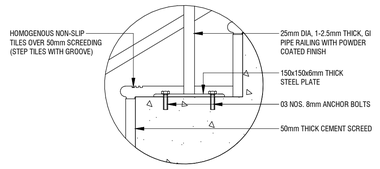

TYPICAL STAIRCASE DETAIL

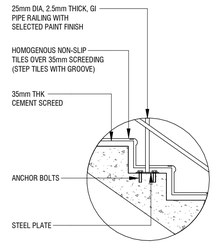

TYPICAL STAIRCASE STEP DETAIL

1 : 20

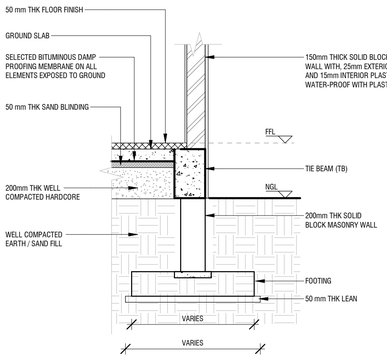

TYPICAL FLOOR TO WALL DETAIL - 01

1 : 25