LUXURIA MALDIVES

11A- CB01- ROOM BLOCK 01 (RETAIL)

LUXURIA HOTELS & RESORTS MALDIVES

ARCHITECTURAL DRAWINGS

The contents of these drawings remai

LIST OF DRAWINGS

SHEET NUMBER	SHEET NAME	SHEET ISSUE DATE	CURRENT REVISION	CURRENT REVISION DATE
00-GENERAL				
00-000-000-01	COVER PAGE	-	00	
00-000-000-02	LIST OF DRAWINGS	-	00	
00-000-000-03	LOCATION PLAN	-	00	
05 - AREAS				
05-100-L00-01	AREA PLAN & SCHEDULE - GROUND FLOOR	-	00	
05-100-L01-01	AREA PLAN & SCHEDULE - FIRST FLOOR	-	00	
05-100-L02-01	AREA PLAN & SCHEDULE - PENTHOUSE FLOOR	-	00	
05-100-R01-01	AREA PLAN & SCHEDULE - ROOF PLAN	-	00	
05-100-R02-01	AREA PLAN & SCHEDULE - LIFT MACHINE ROOM ROOF PLAN	-	00	
10 - GENERAL ARRANGEMENT				
10-100-L00-01	GROUND FLOOR PLAN	-	00	
10-100-L01-01	FIRST FLOOR PLAN	-	00	
10-100-L02-01	PENTHOUSE FLOOR PLAN	-	00	
10-100-R01-01	ROOF PLAN	-	00	
10-100-R02-01	LIFT MACHINE ROOM ROOF PLAN	-	00	
10-200-000-01	SECTIONS	-	00	
10-300-000-01	ELEVATIONS	-	00	
10-500-000-01	3D VIEWS	-	00	
19 - DOORS				
19-400-000-01	DOOR SCHEDULE & DETAILS - 01	-	00	
19-400-000-02	DOOR SCHEDULE & DETAILS - 02	-	00	
20 -WINDOWS				
20-400-000-01	WINDOW SCHEDULE & DETAILS	-	00	
21 - CEILING				
21-100-L00-01	REFLECTED CEILING PLAN - GROUND FLOOR	-	00	
21-100-L01-01	REFLECTED CEILING PLAN - FIRST FLOOR	-	00	
21-100-L02-01	REFLECTED CEILING PLAN - PENTHOUSE FLOOR	-	00	
24 - TYPICAL DETAILS				
24-600-000-01	TYPICAL DETAILS	-	00	

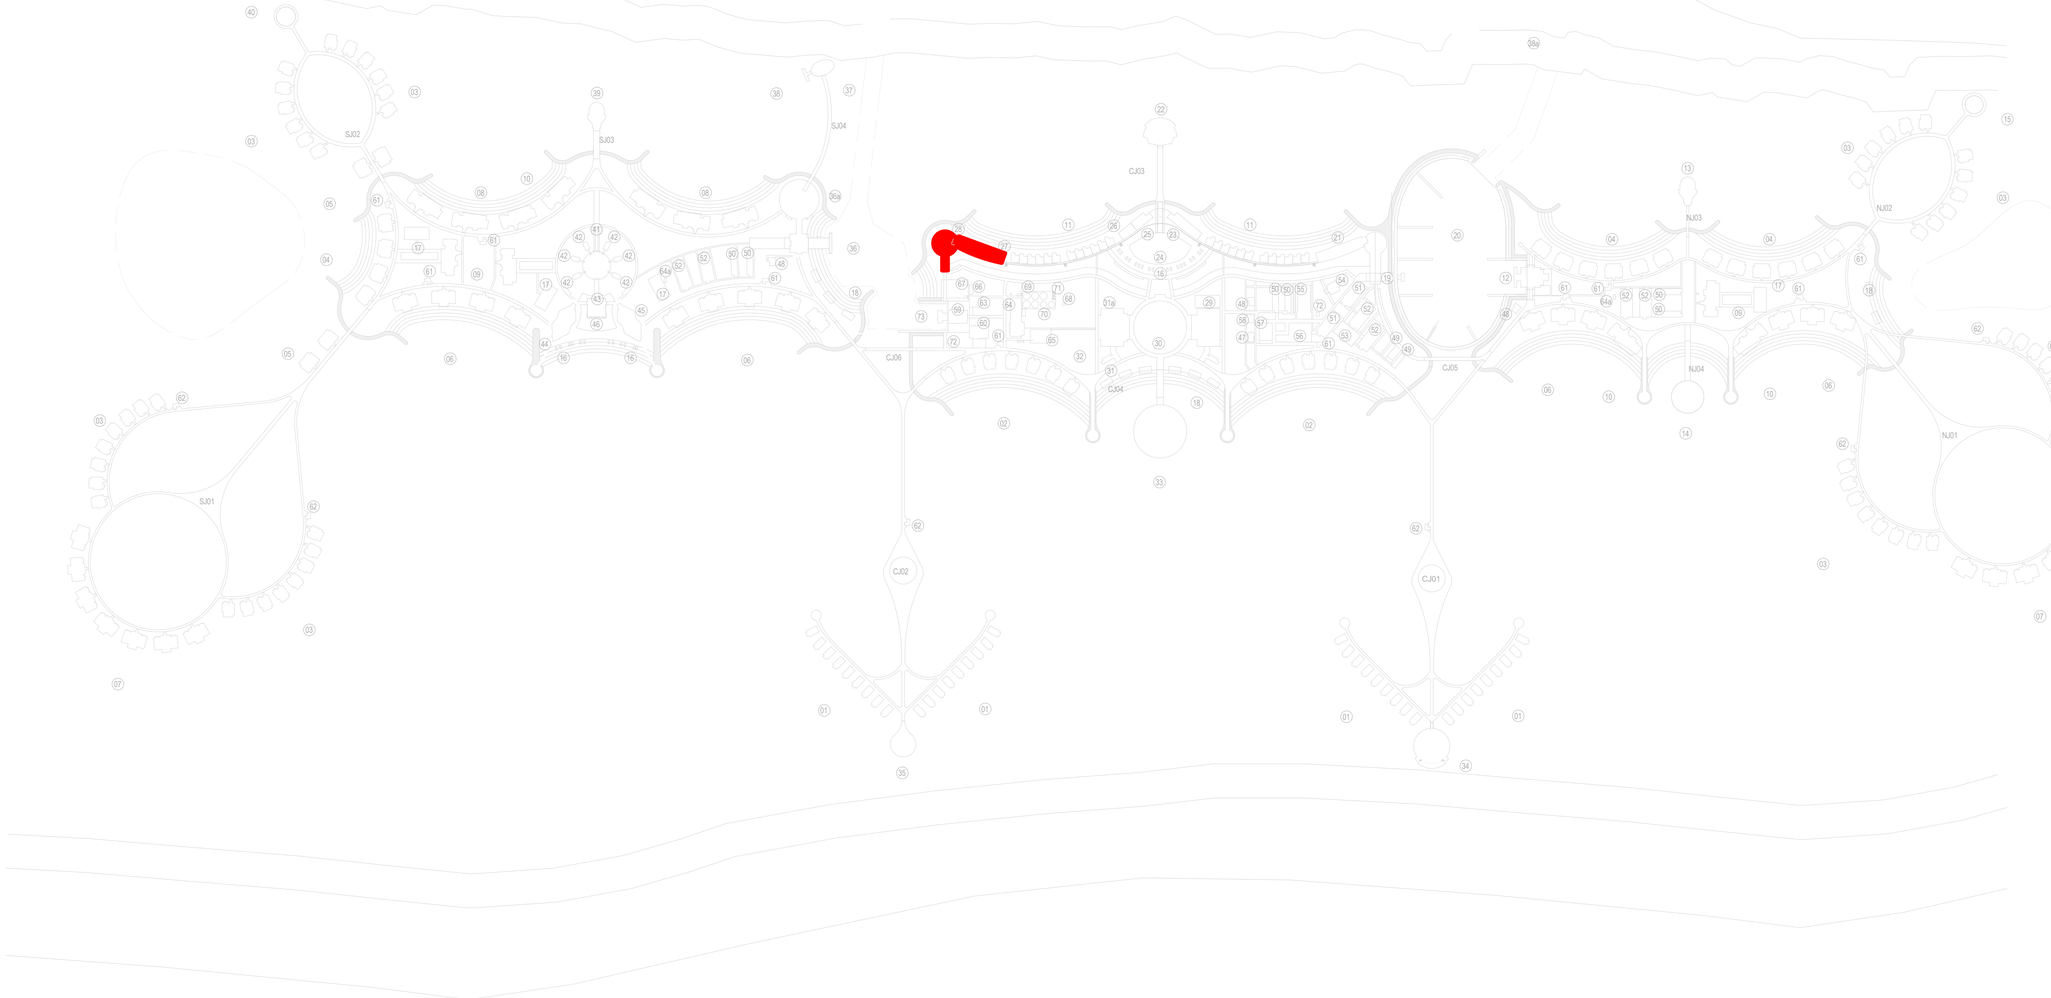

LOCATION PLAN

1 : 4500

WALL LEGEND

- 150mm THICK SOLID BLOCK MASONRY WALL
- 100mm THICK SOLID BLOCK MASONRY WALL
- 150mm CONCRETE WALL / FILLINGS
- 20mm GLASS WALL

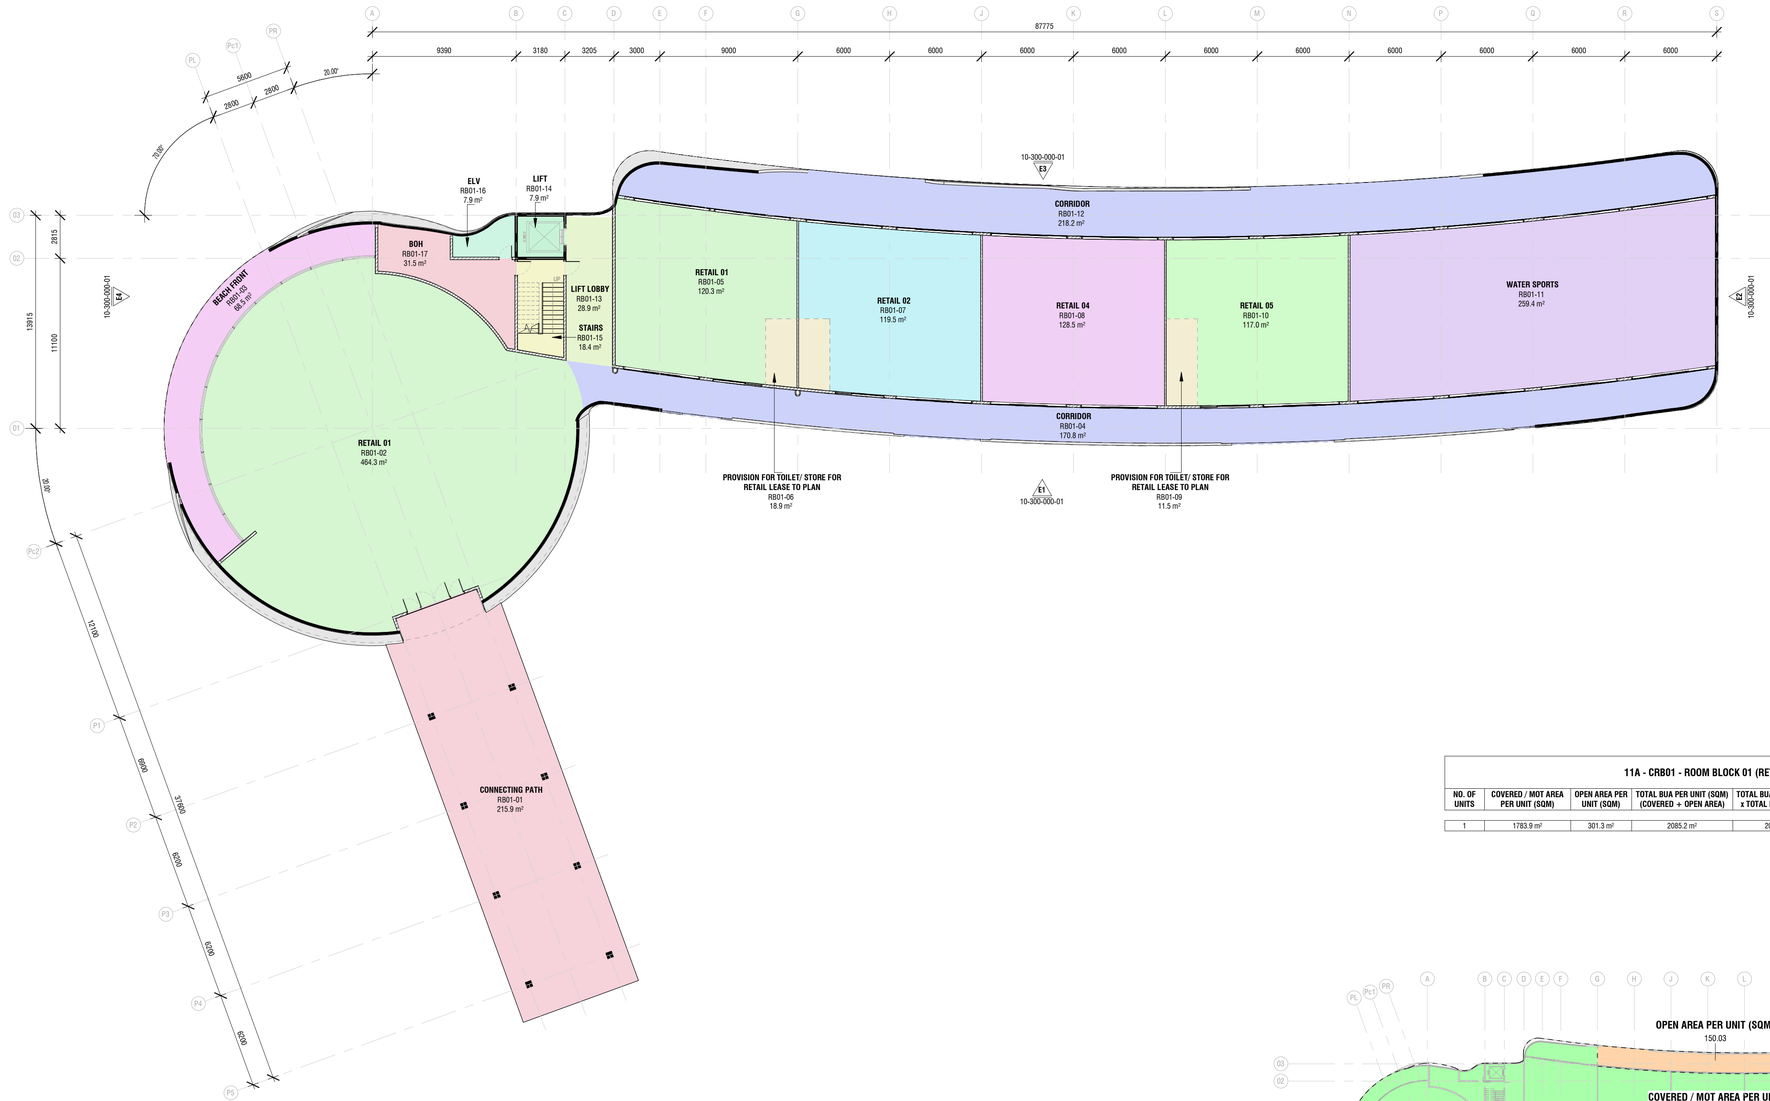

AREA SCHEDULE - GROUND FLOOR

NAME	NUMBER	AREA
CONNECTING PATH	RB01-01	215.9 m²
RETAIL 01	RB01-02	464.3 m²
BEACH FRONT	RB01-03	68.5 m²
CORRIDOR	RB01-04	170.8 m²
RETAIL 01	RB01-05	120.3 m²
PROVISION FOR TOILET/ STORE FOR RETAIL LEASE TO PLAN	RB01-06	18.9 m²
RETAIL 02	RB01-07	119.5 m²
RETAIL 04	RB01-08	128.5 m²
PROVISION FOR TOILET/ STORE FOR RETAIL LEASE TO PLAN	RB01-09	11.5 m²
RETAIL 05	RB01-10	117.0 m²
WATER SPORTS	RB01-11	259.4 m²
CORRIDOR	RB01-12	218.2 m²
LIFT LOBBY	RB01-13	28.9 m²
LIFT	RB01-14	7.9 m²
STAIRS	RB01-15	18.4 m²
ELV	RB01-16	7.9 m²
BOH	RB01-17	31.5 m²
TOTAL USABLE AREA		2007.3 m²

AREA PLAN & SCHEDULE - GROUND FLOOR

1 : 200

11A - CRB01 - ROOM BLOCK 01 (RETAIL)

NO. OF UNITS	COVERED / MOT AREA PER UNIT (SQM)	OPEN AREA PER UNIT (SQM)	TOTAL BUA PER UNIT (SQM) (COVERED + OPEN AREA)	TOTAL BUA (NO. OF UNITS x TOTAL BUA PER UNIT)	TOTAL MOT AREA (SQM) (NO. OF UNITS x COVERED / MOT AREA PER UNIT)
1	1783.9 m²	301.3 m²	2085.2 m²	2085.2 m²	1783.9 m²

	TOTAL BUA PER UNIT	NO. OF UNITS	TOTAL BUA
GROUND FLOOR	2085.2 m²	01	4890.4 m²
FIRST FLOOR	326.4 m²		
PENTHOUSE FLOOR	1280.4 m²		
ROOF FLOOR	1166.9 m²		
LIFT MACHINE ROOM ROOF FLOOR	31.5 m²		
TOTAL	4890.4 m²		

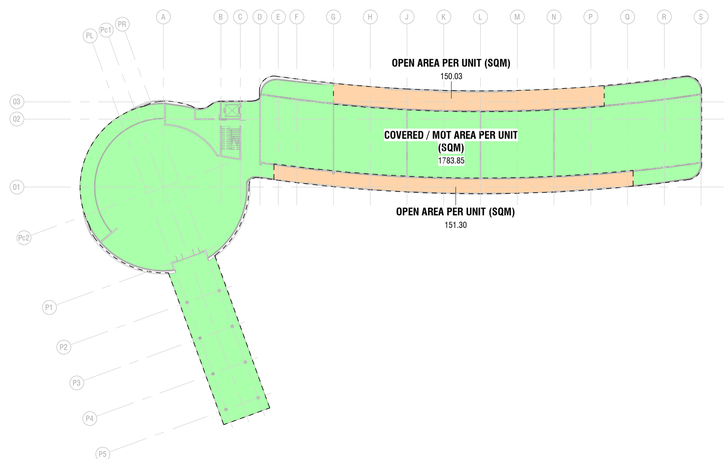

TOTAL BUA UNIT PLAN

1 : 500

WALL LEGEND

- 150mm THICK SOLID BLOCK MASONRY WALL
- 100mm THICK SOLID BLOCK MASONRY WALL
- 150mm CONCRETE WALL / FILLINGS
- 20mm GLASS WALL

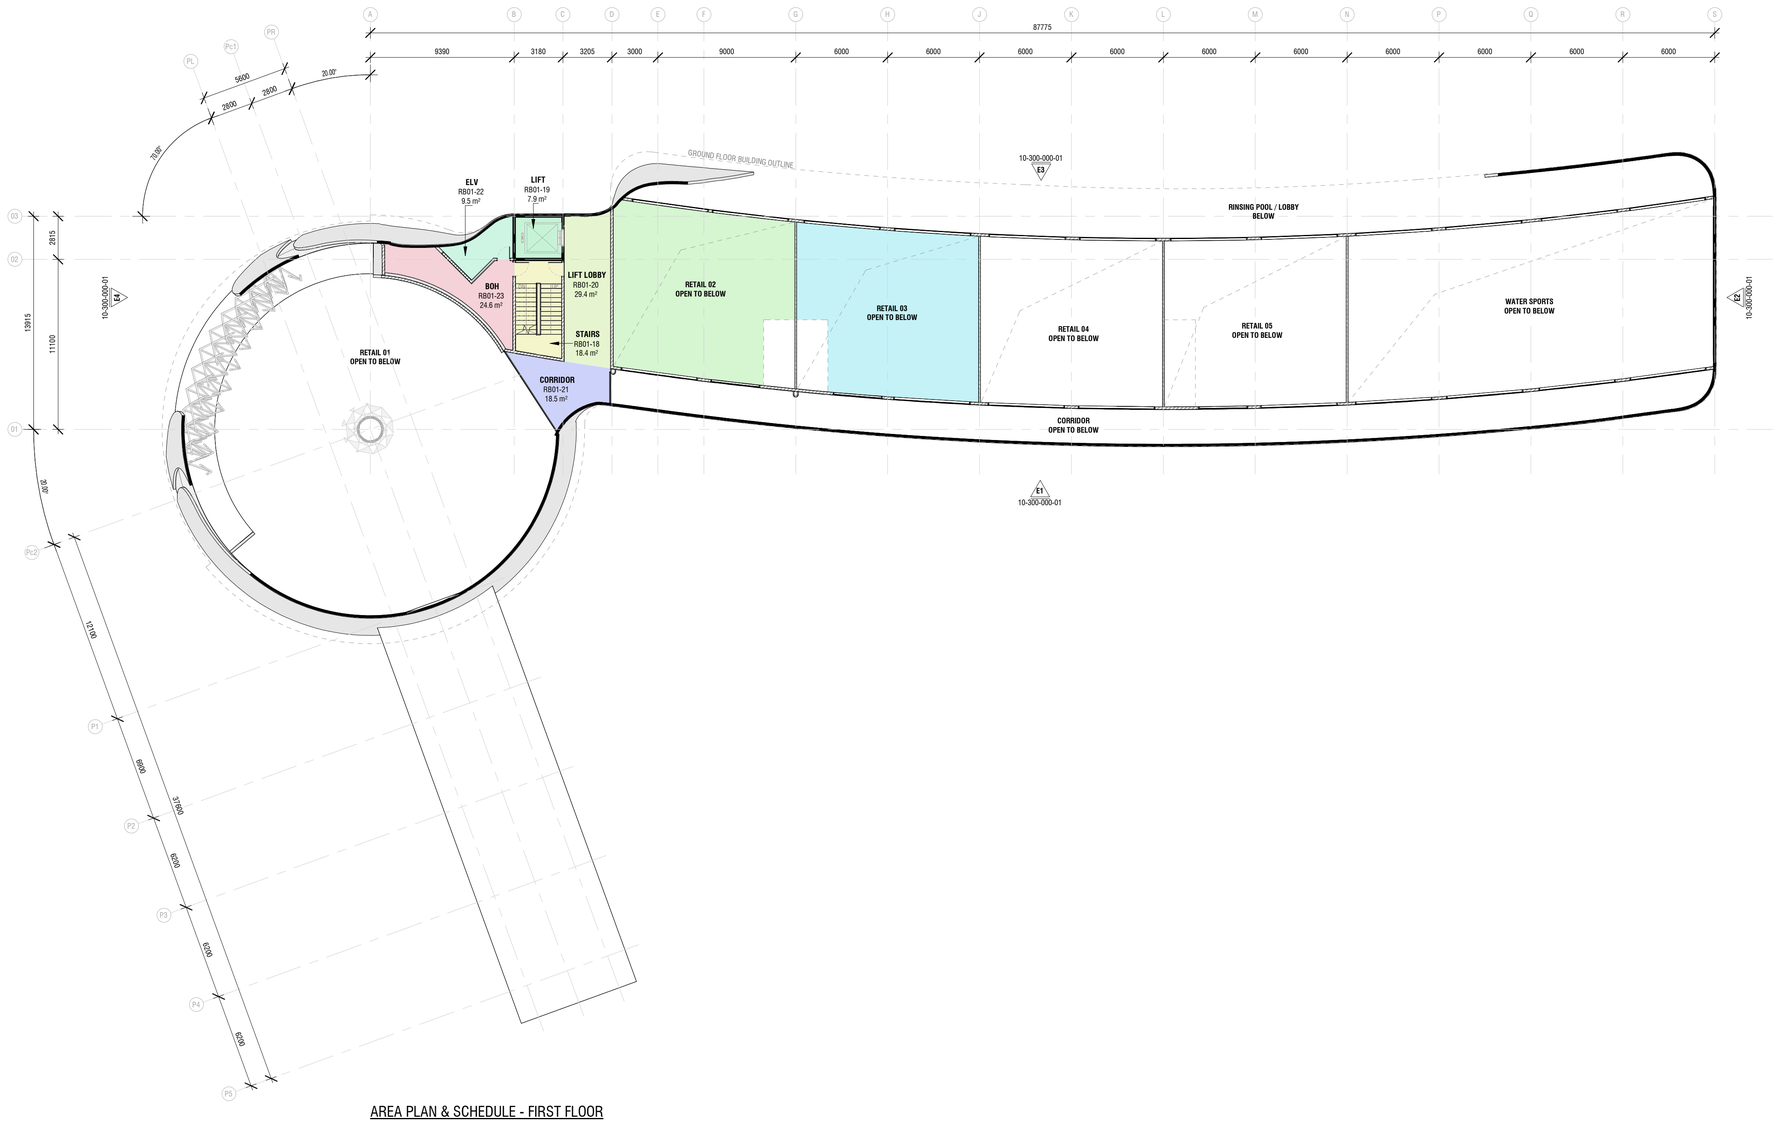

AREA SCHEDULE - FIRST FLOOR

NAME	NUMBER	AREA
STAIRS	RB01-18	18.4 m²
LIFT	RB01-19	7.9 m²
LIFT LOBBY	RB01-20	29.4 m²
CORRIDOR	RB01-21	18.5 m²
ELV	RB01-22	9.5 m²
BOH	RB01-23	24.6 m²
TOTAL USABLE AREA		108.4 m²

AREA PLAN & SCHEDULE - FIRST FLOOR

1 : 200

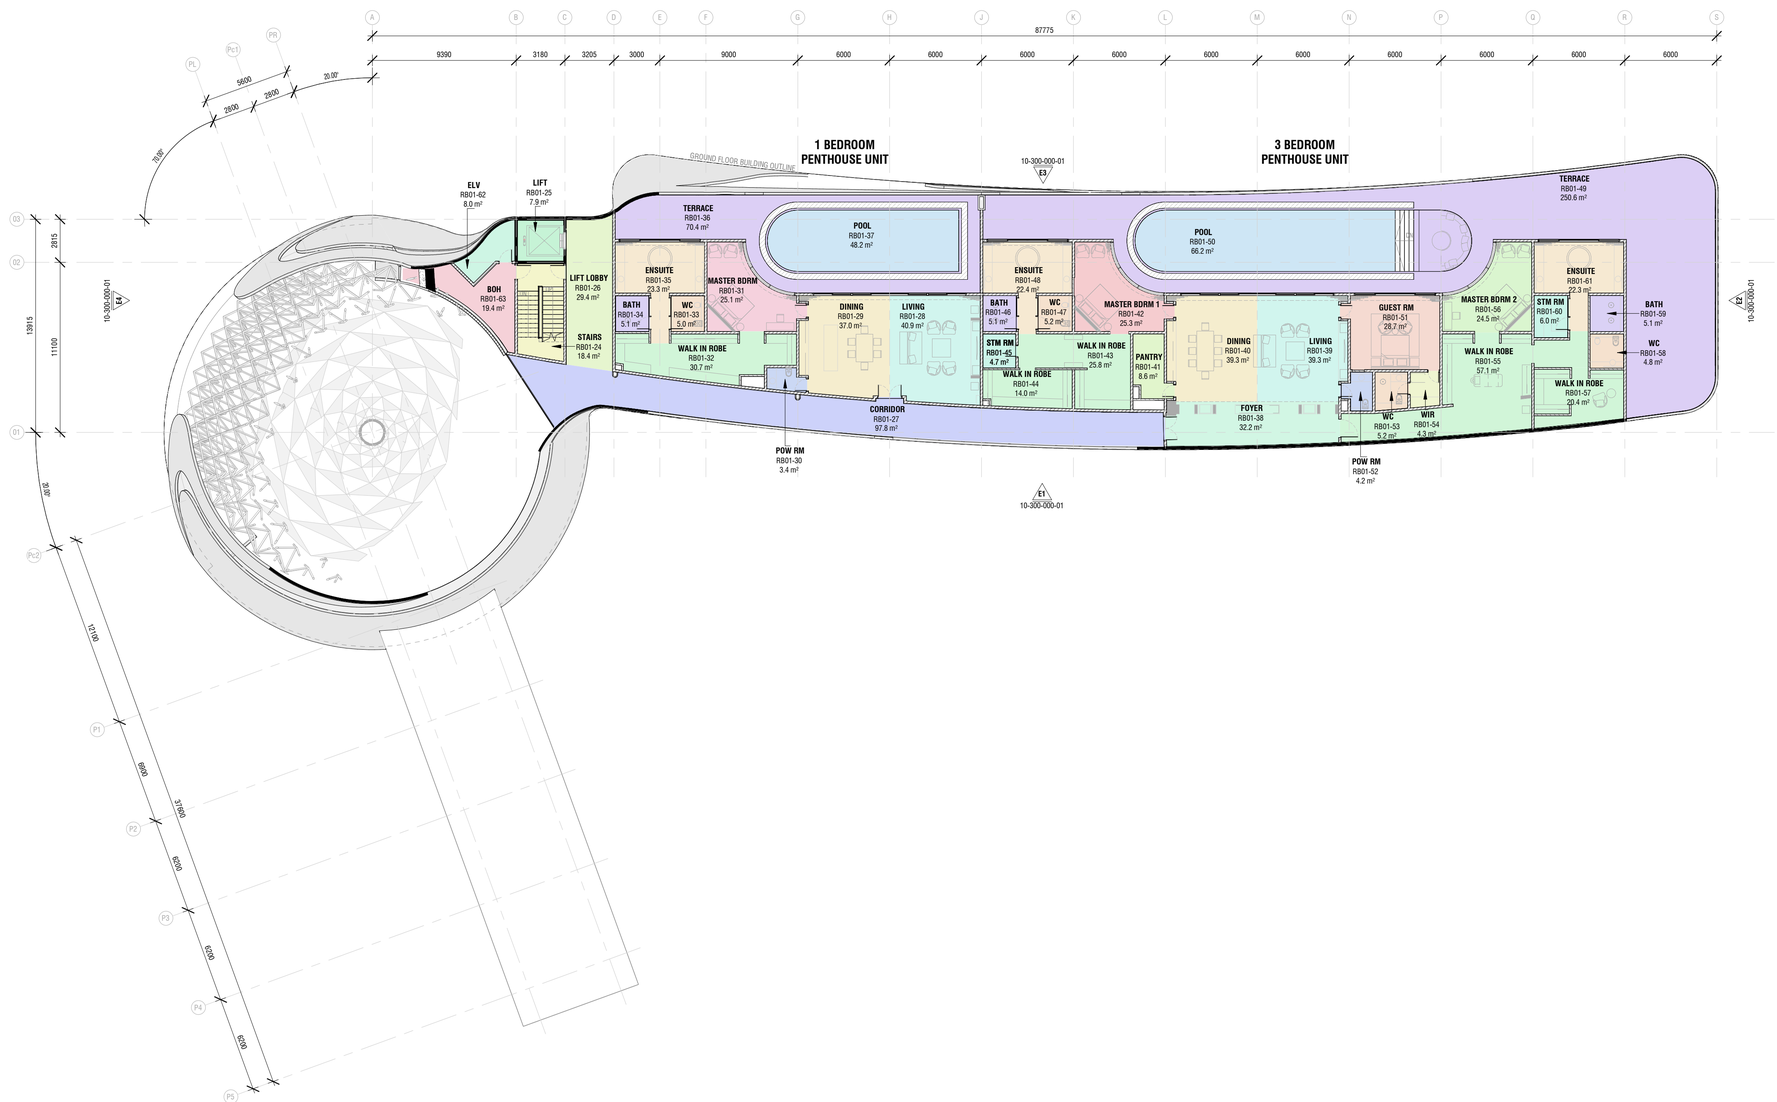
1 BEDROOM PENTHOUSE UNIT
3 BEDROOM PENTHOUSE UNIT
GROUND FLOOR BUILDING OUTLINE
87775
9390
3180
3205
3000
9000
6000
6000
6

WALL LEGEND

- 150mm THICK SOLID BLOCK MASONRY WALL
- 100mm THICK SOLID BLOCK MASONRY WALL
- 150mm CONCRETE WALL / FILLINGS
- 20mm GLASS WALL

AREA SCHEDULE - ROOF		
NAME	**NUMBER**	**AREA**
LIFT MACHINE ROOM	RB01-65	8.1 m²
ROOF	RB01-66	1044.6 m²
STAIRS	RB01-64	18.4 m²
TOTAL USABLE AREA		1071.1 m²

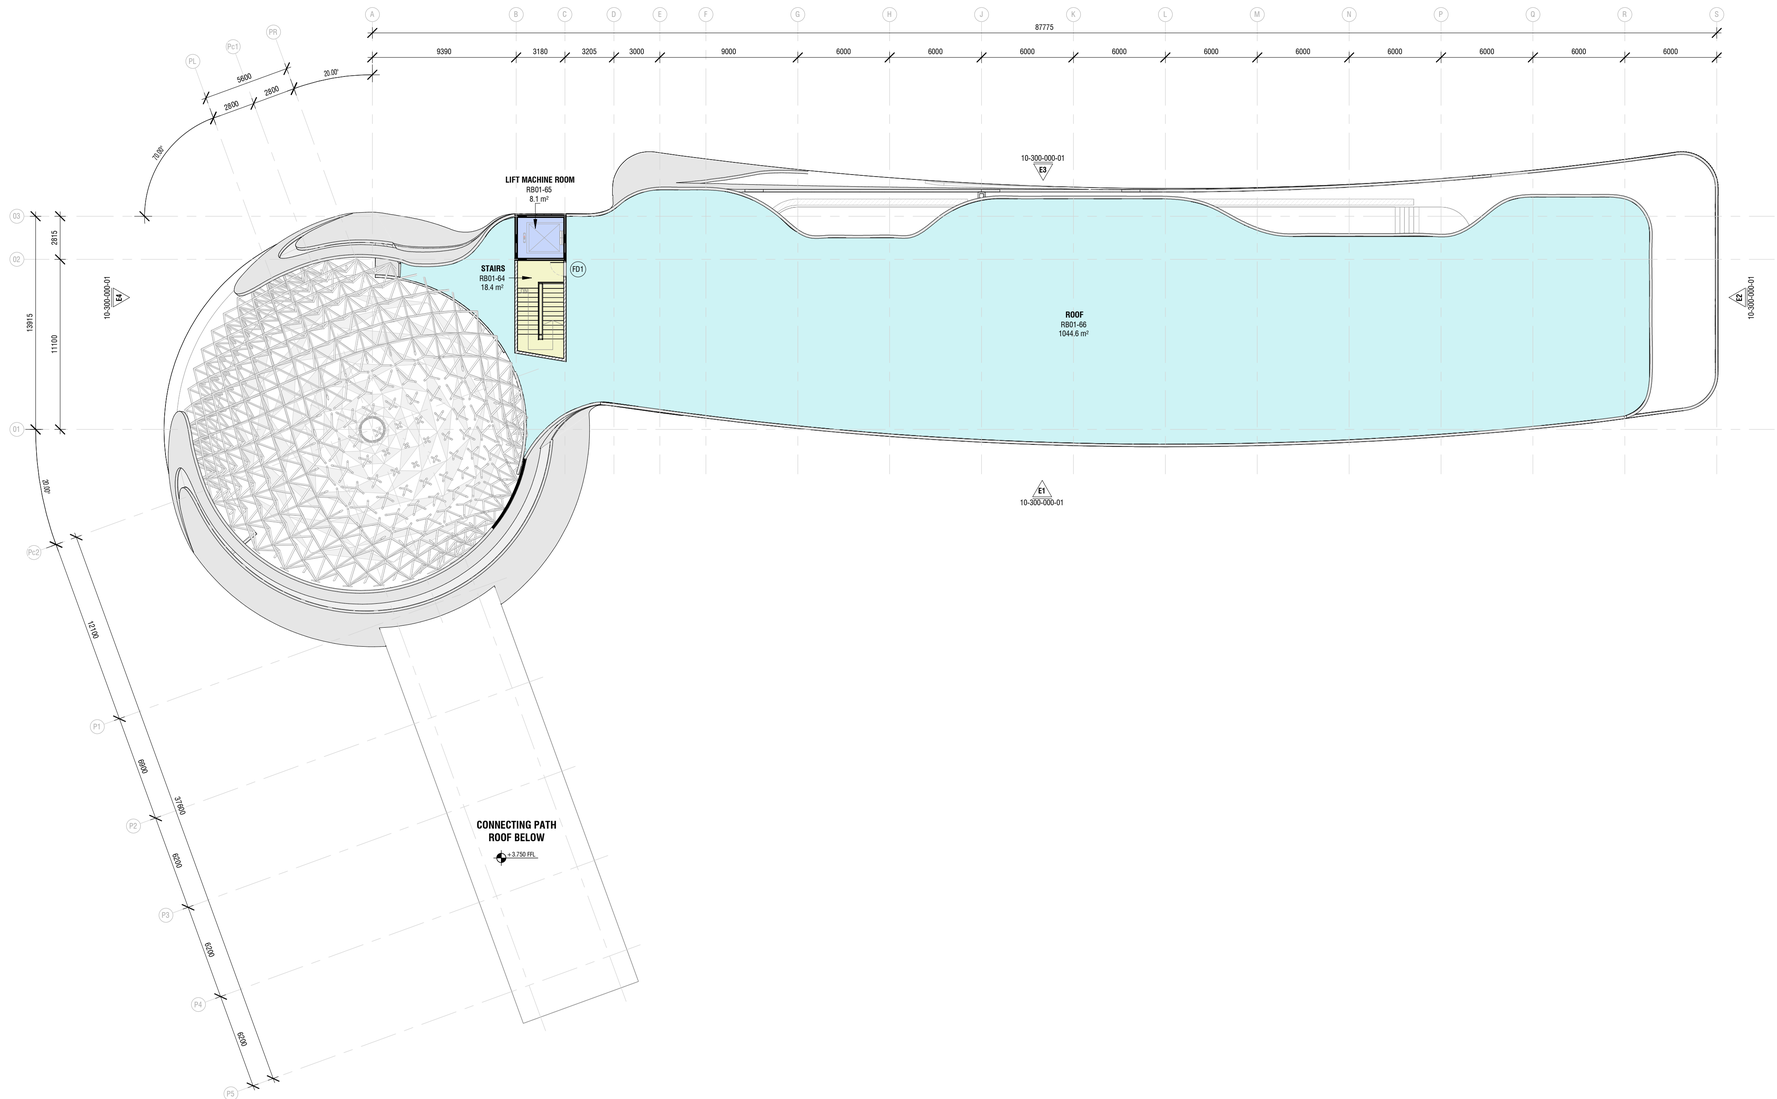

AREA PLAN & SCHEDULE - ROOF PLAN

1 : 200

WALL LEGEND

- 150mm THICK SOLID BLOCK MASONRY WALL
- 100mm THICK SOLID BLOCK MASONRY WALL
- 150mm CONCRETE WALL / FILLINGS
- 20mm GLASS WALL

AREA SCHEDULE - LIFT MACHINE ROOM ROOF

NAME	NUMBER	AREA
LIFT MACHINE ROOM ROOF	RB01-67	26.8 m²
TOTAL USABLE AREA		26.8 m²

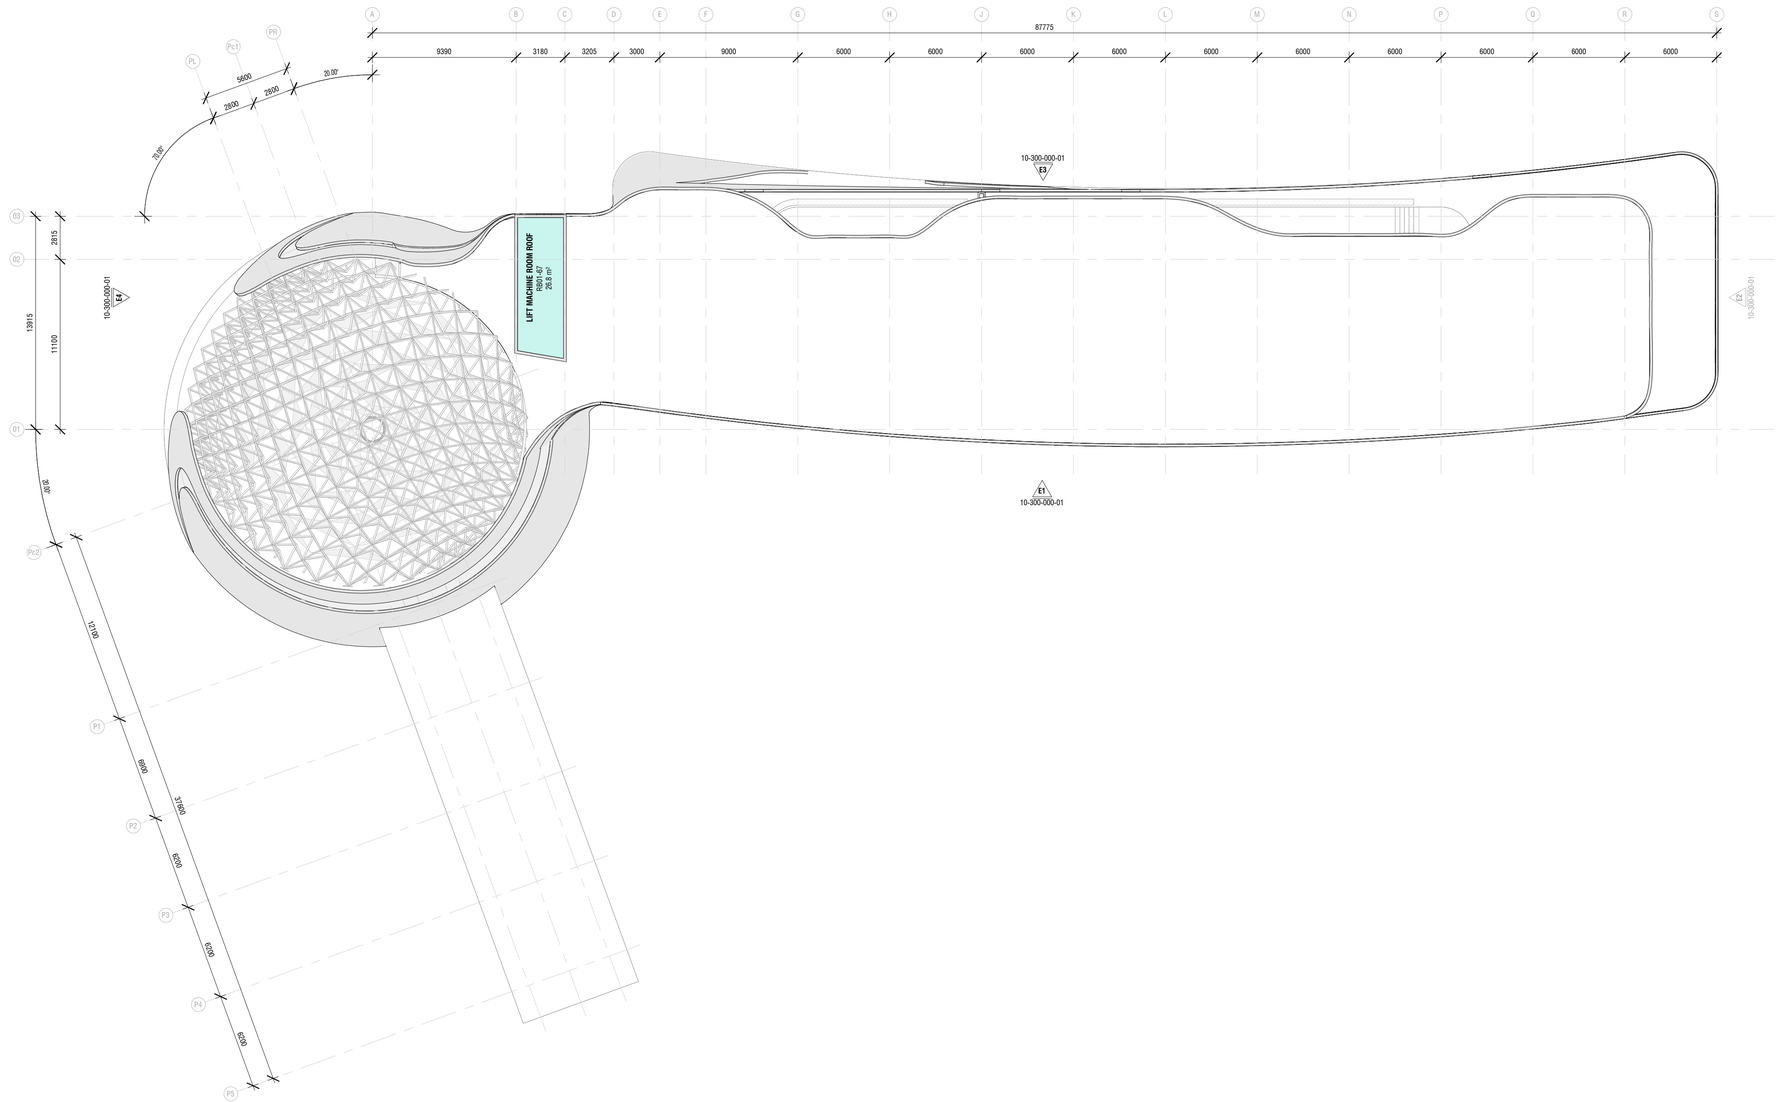

AREA PLAN & SCHEDULE - LIFT MACHINE ROOM ROOF PLAN

1 : 200

WALL LEGEND

- 150mm THICK SOLID BLOCK MASONRY WALL
- 100mm THICK SOLID BLOCK MASONRY WALL
- 150mm CONCRETE WALL / FILLINGS
- 20mm GLASS WALL

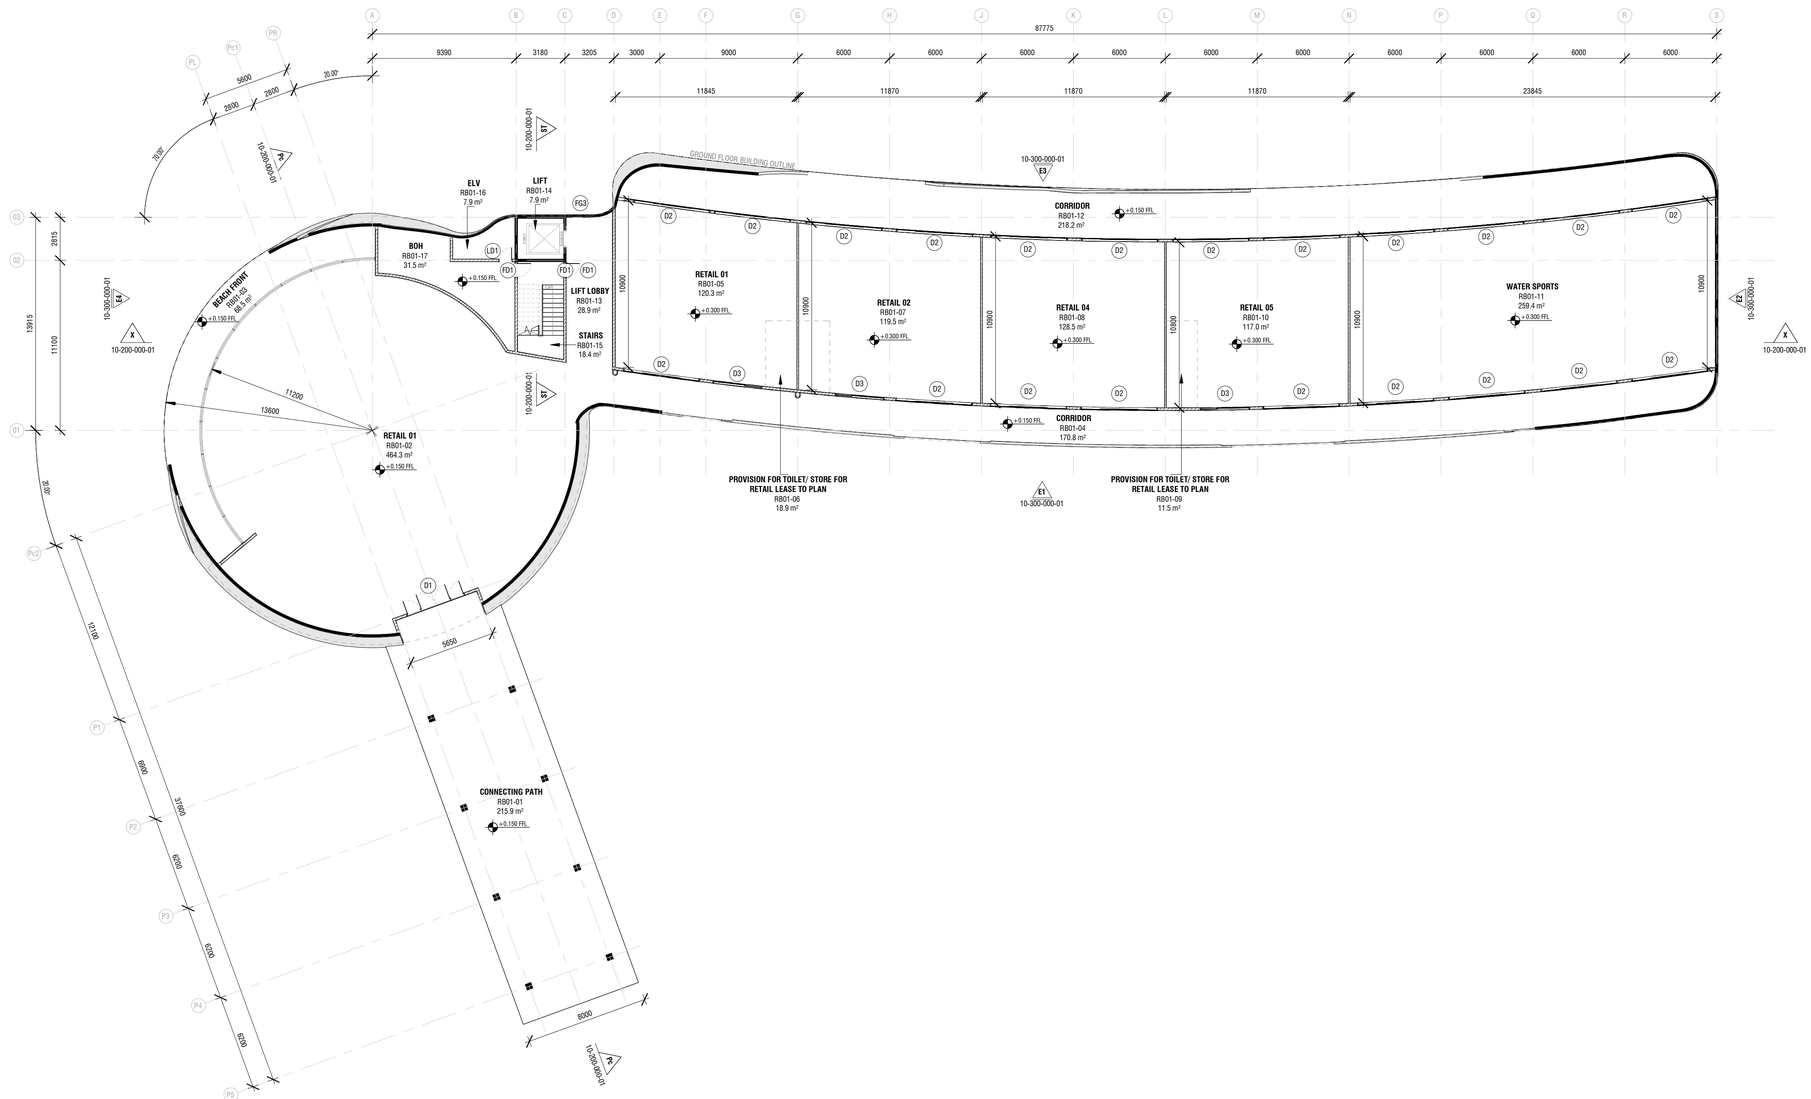

GROUND FLOOR PLAN

1 : 200

WALL LEGEND

- 150mm THICK SOLID BLOCK MASONRY WALL
- 100mm THICK SOLID BLOCK MASONRY WALL
- 150mm CONCRETE WALL / FILLINGS
- 20mm GLASS WALL

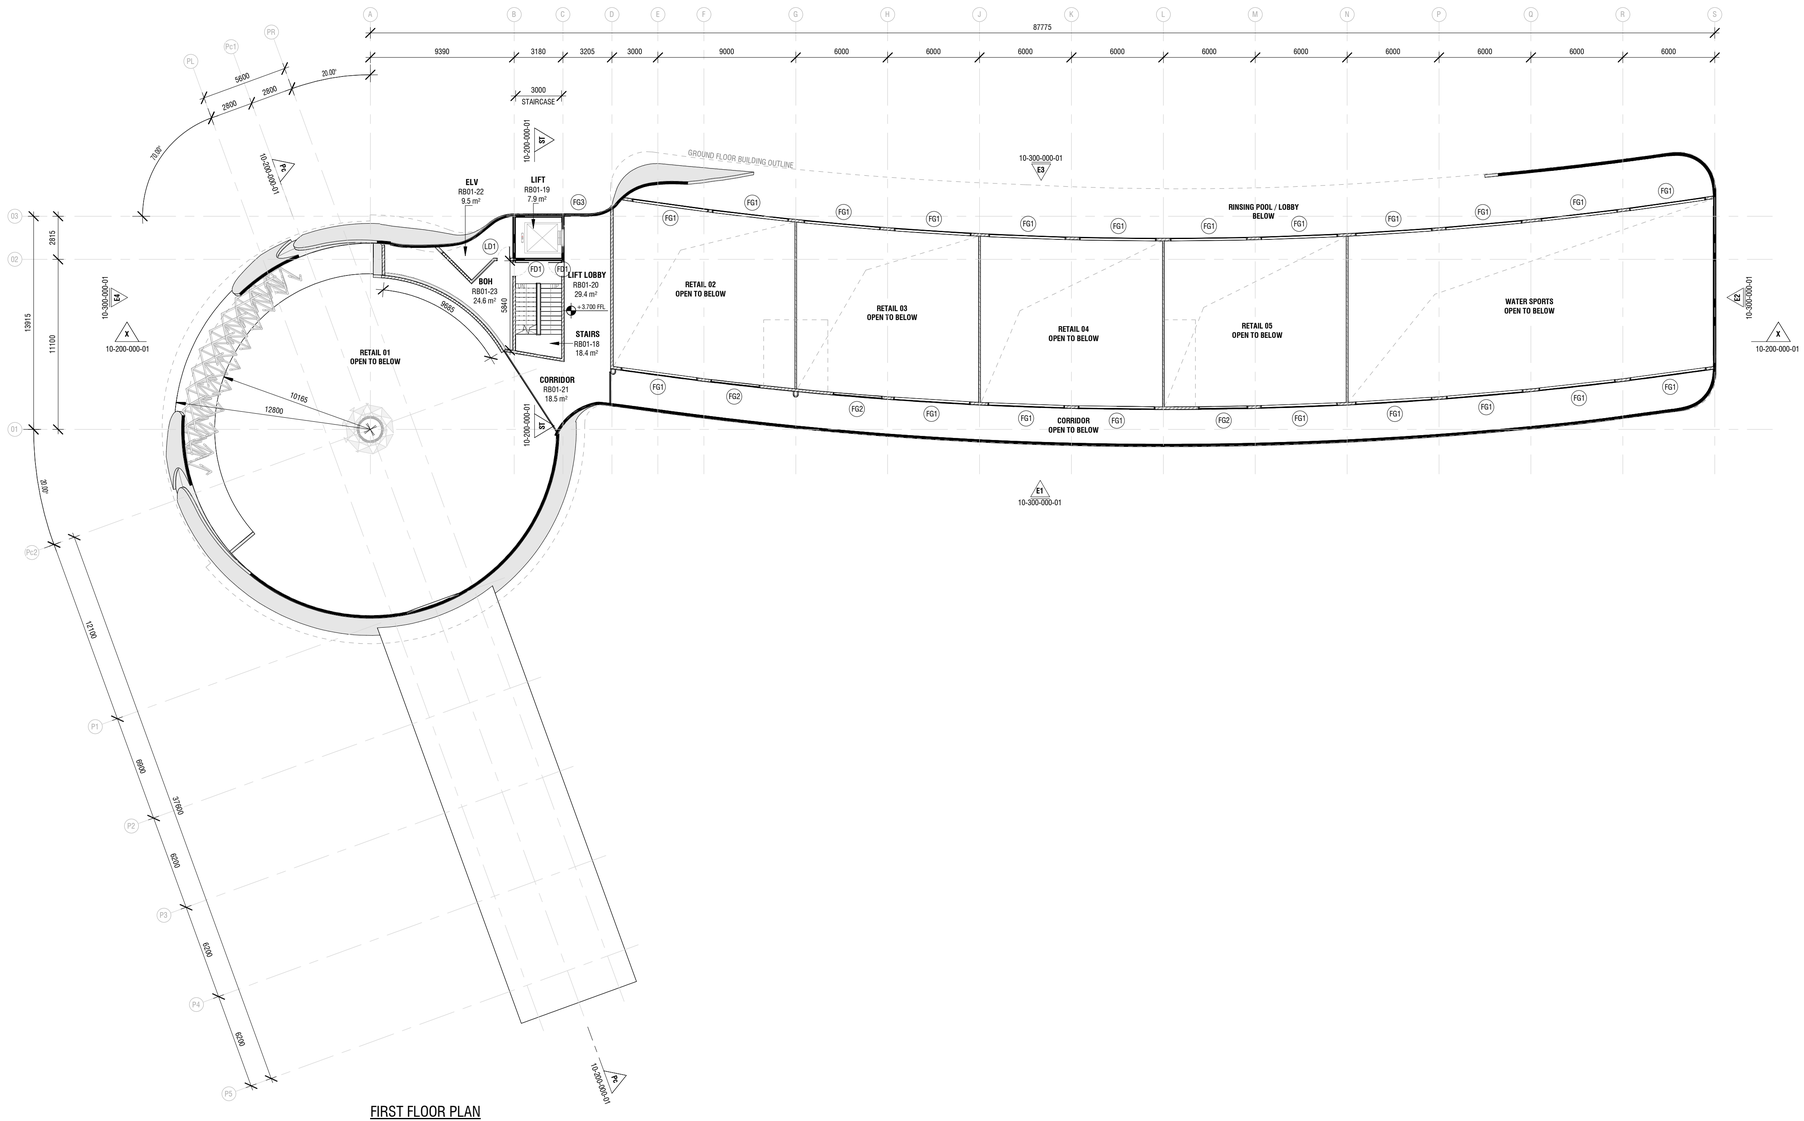

FIRST FLOOR PLAN

1 : 200

WALL LEGEND

- 150mm THICK SOLID BLOCK MASONRY WALL
- 100mm THICK SOLID BLOCK MASONRY WALL
- 150mm CONCRETE WALL / FILLINGS
- 20mm GLASS WALL

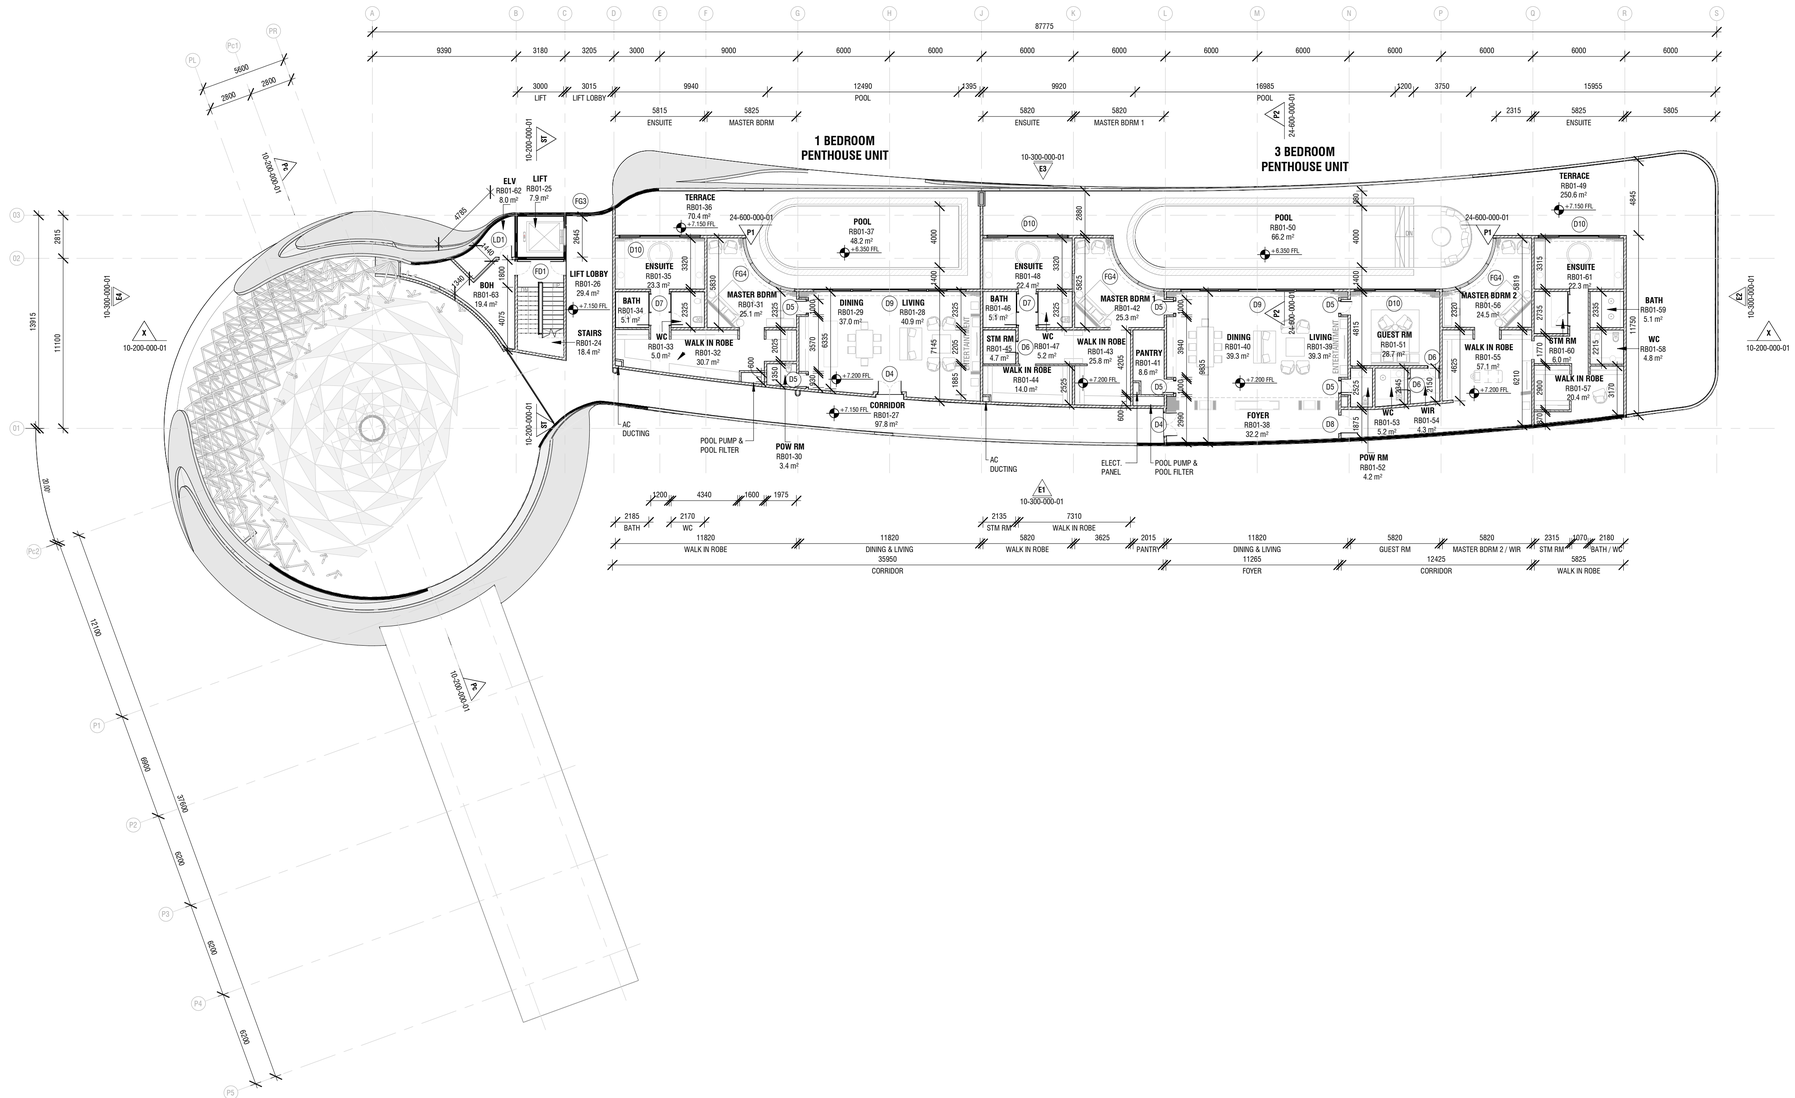

PENTHOUSE FLOOR PLAN

1 : 200

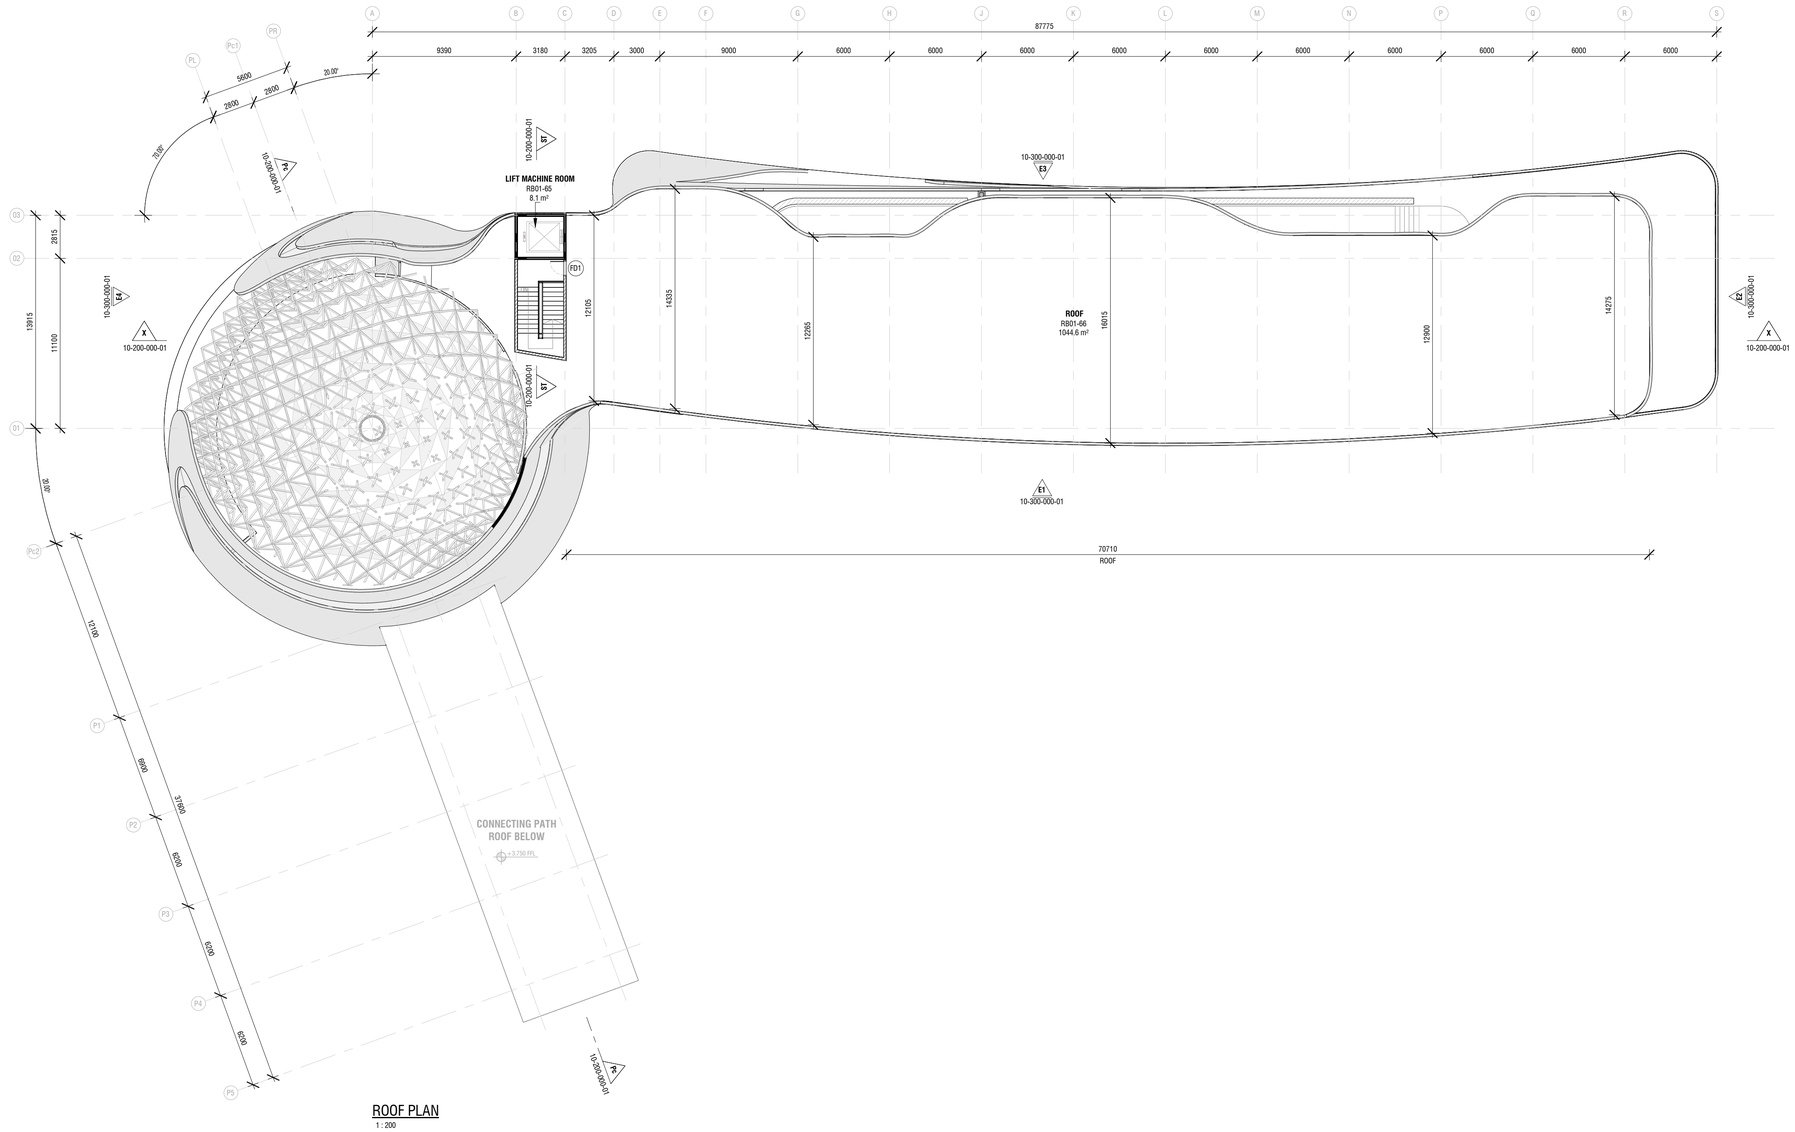

ROOF PLAN
1 : 200

WALL LEGEND

- 150mm THICK SOLID BLOCK MASONRY WALL
- 100mm THICK SOLID BLOCK MASONRY WALL
- 150mm CONCRETE WALL / FILLINGS
- 20mm GLASS WALL

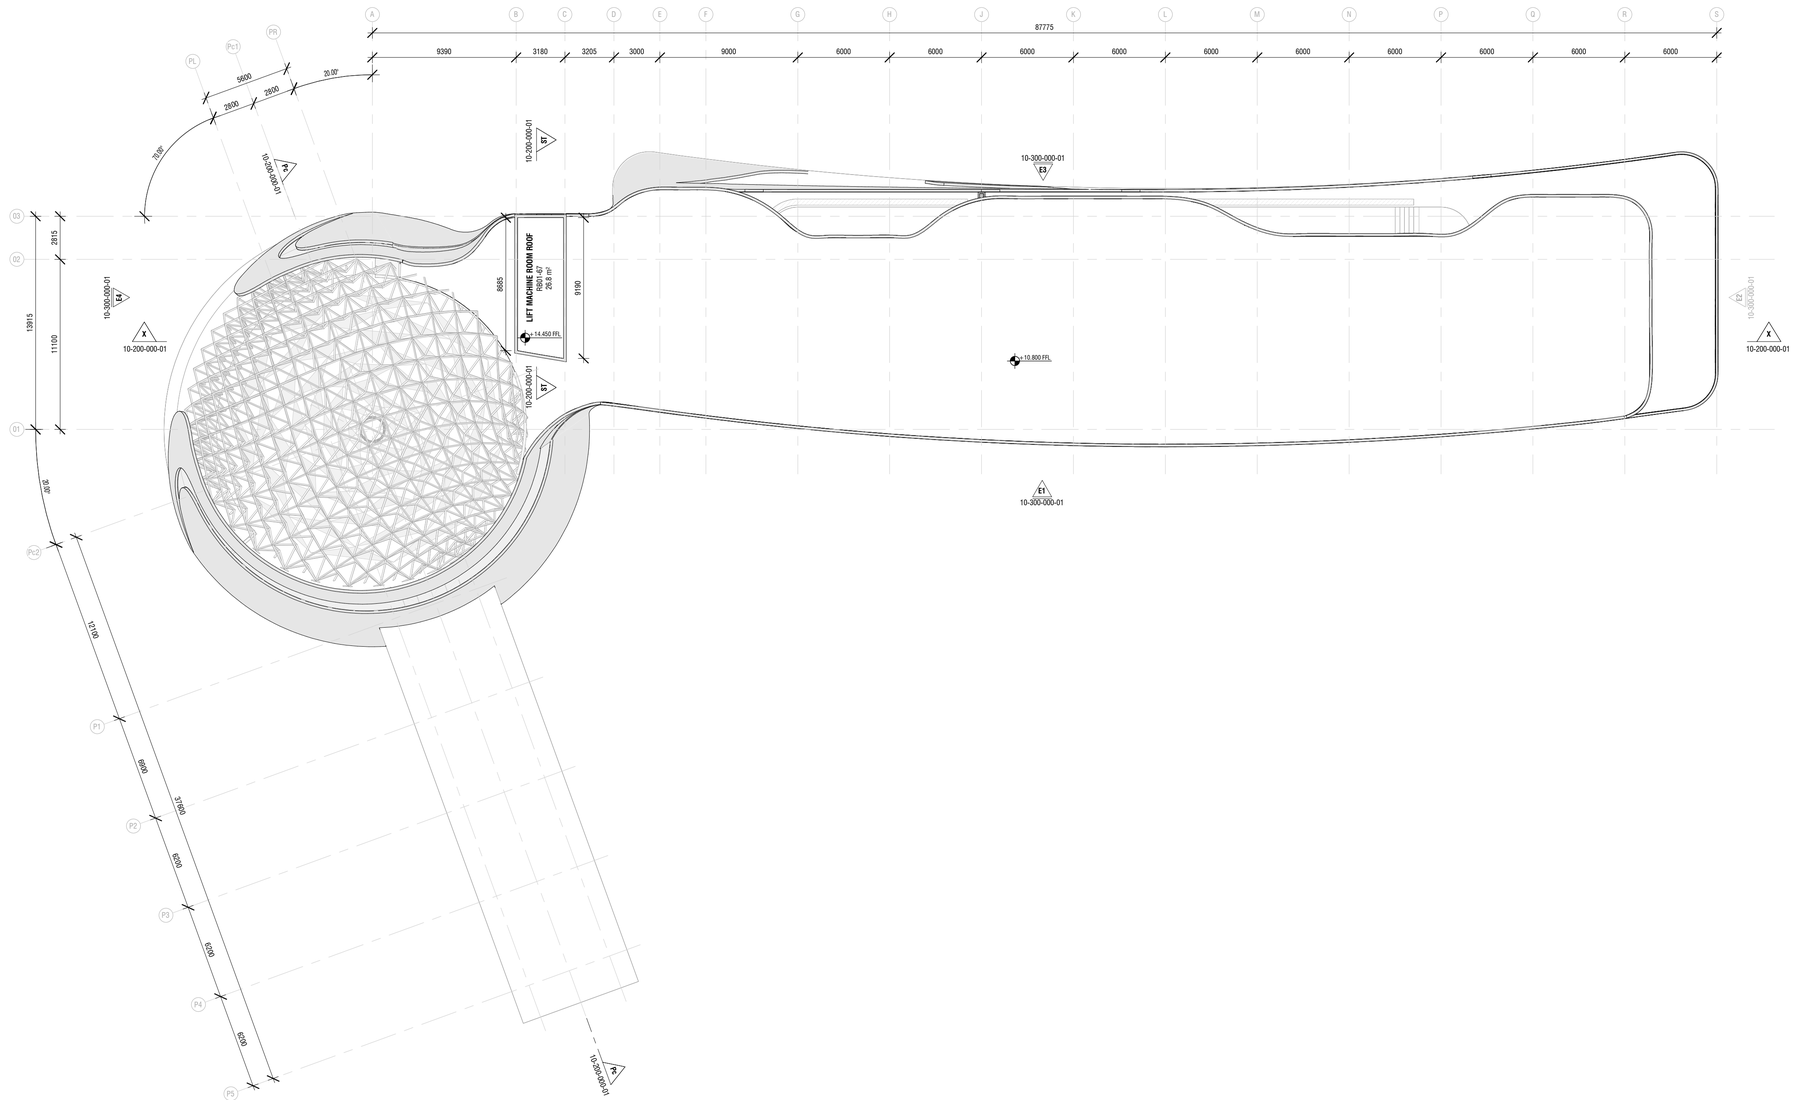

LIFT MACHINE ROOM ROOF PLAN

1 : 200

SECTION X

1 : 200

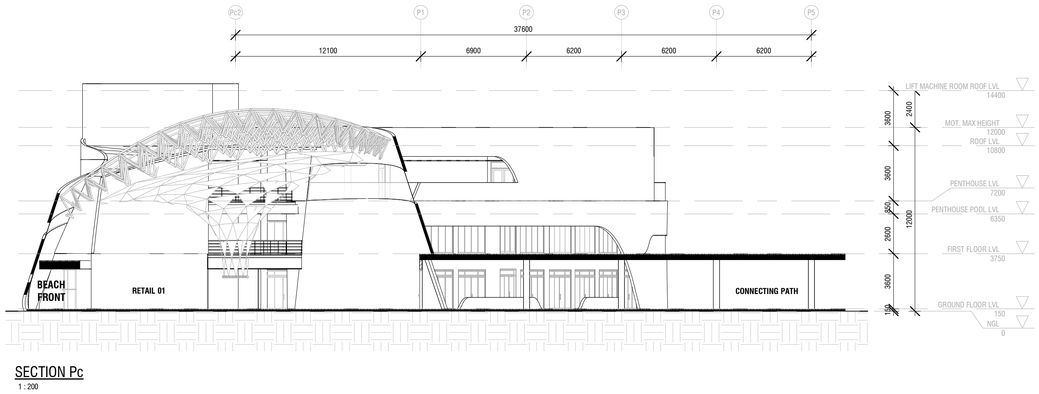

SECTION Pc

1 : 200

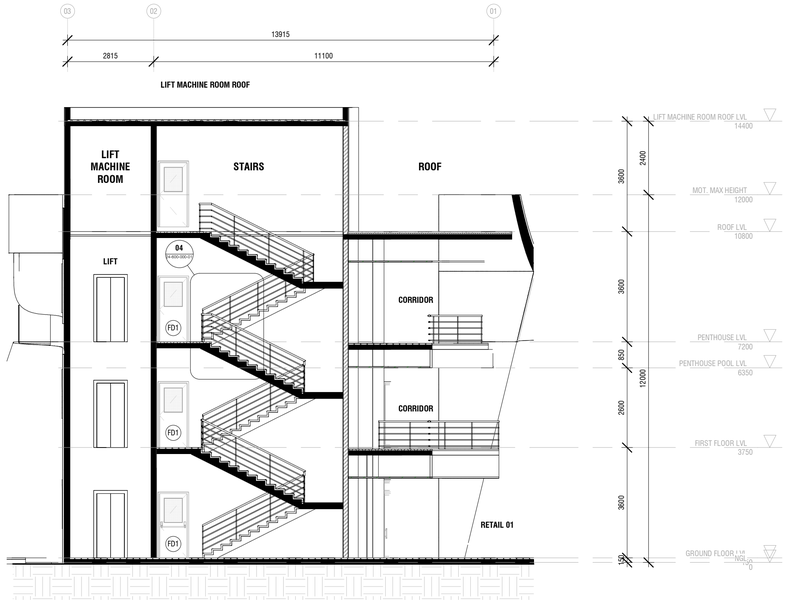

SECTION ST

1 : 100

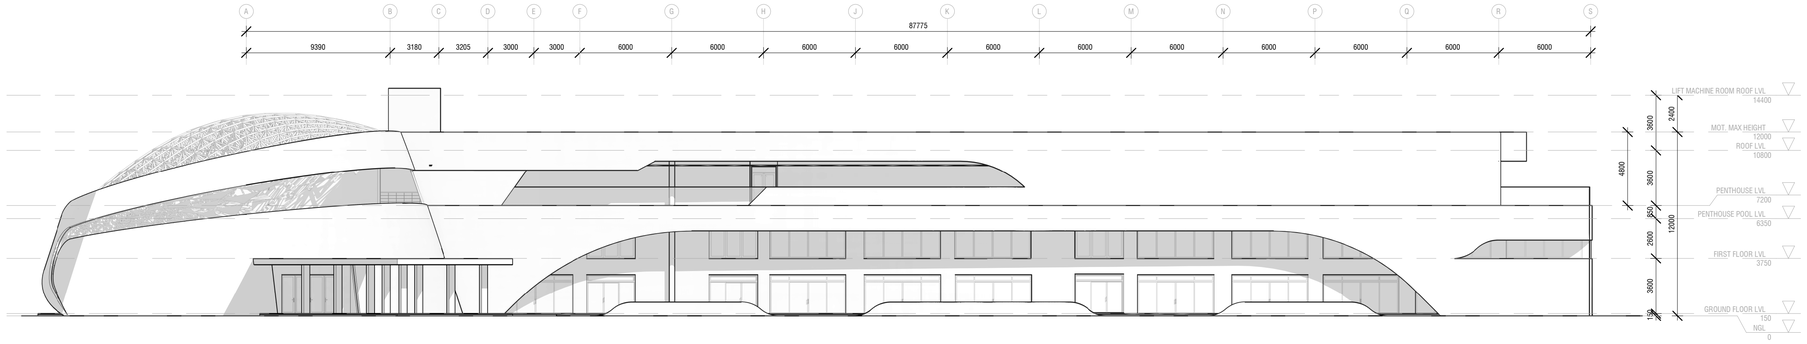

ELEVATION 01

1 : 200

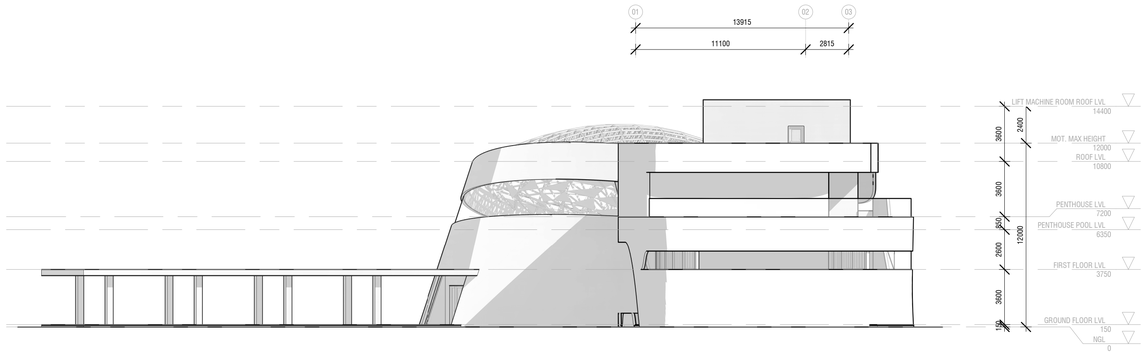

ELEVATION 02

1 : 200

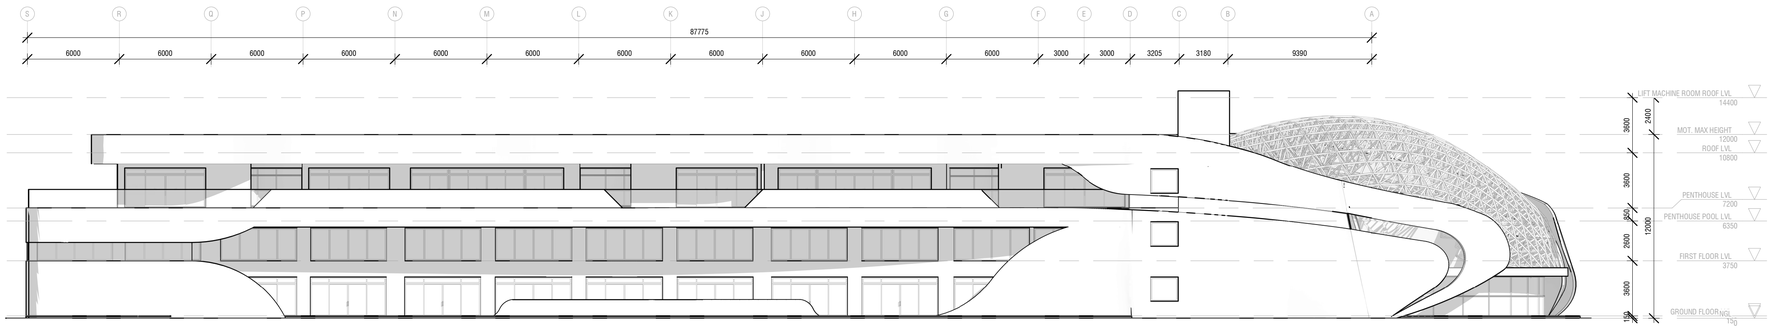

ELEVATION 03

1 : 200

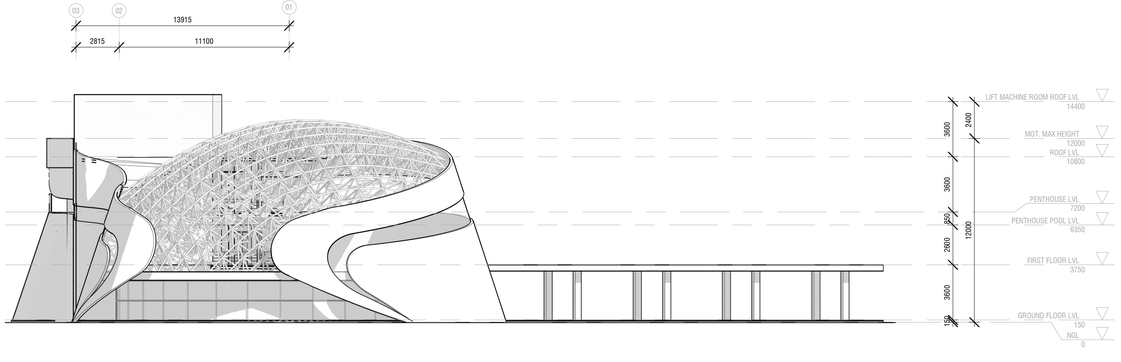

ELEVATION 04

1 : 200

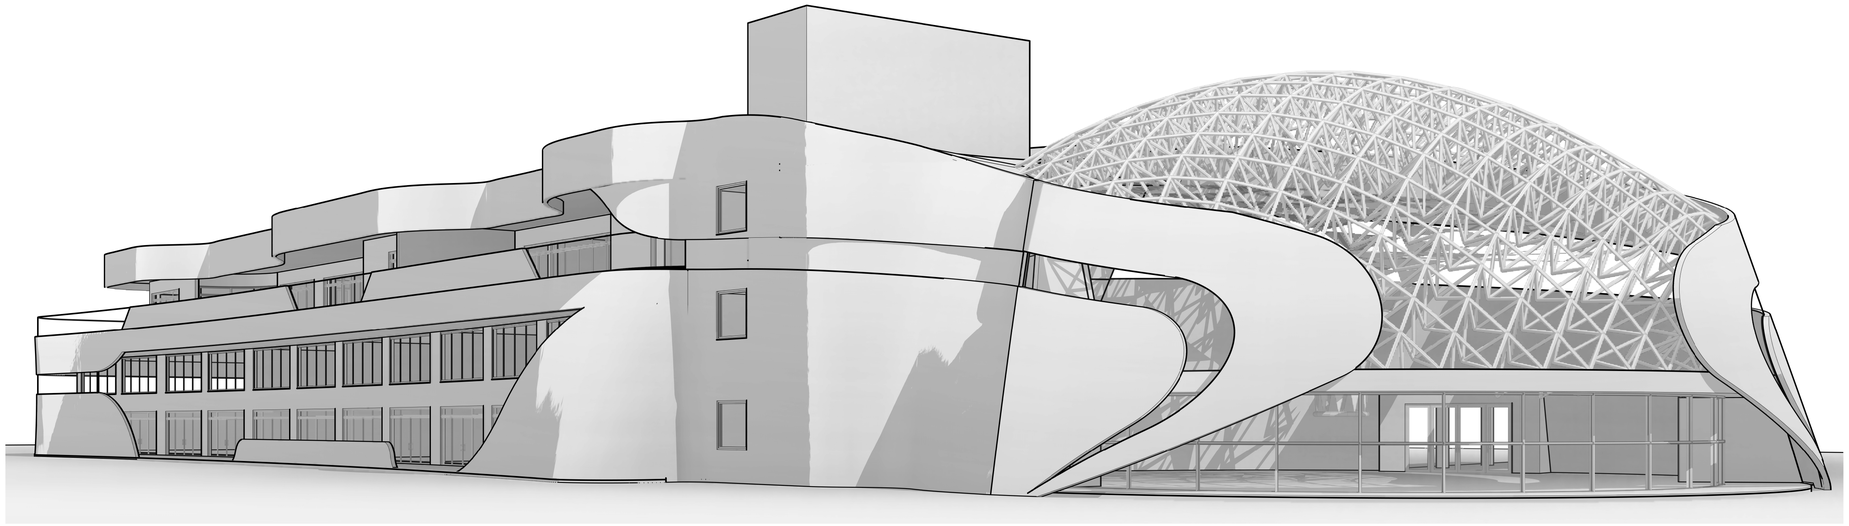

3D VIEW 01

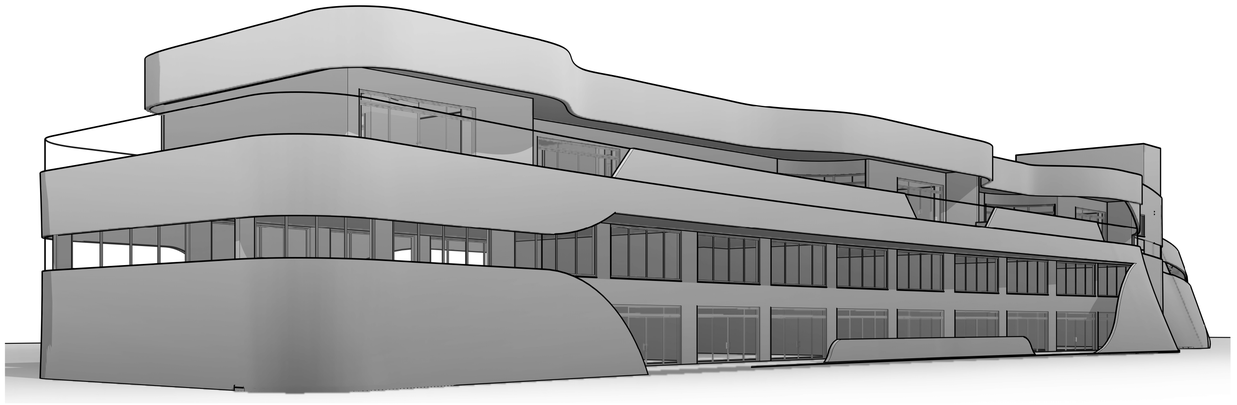

3D VIEW 02

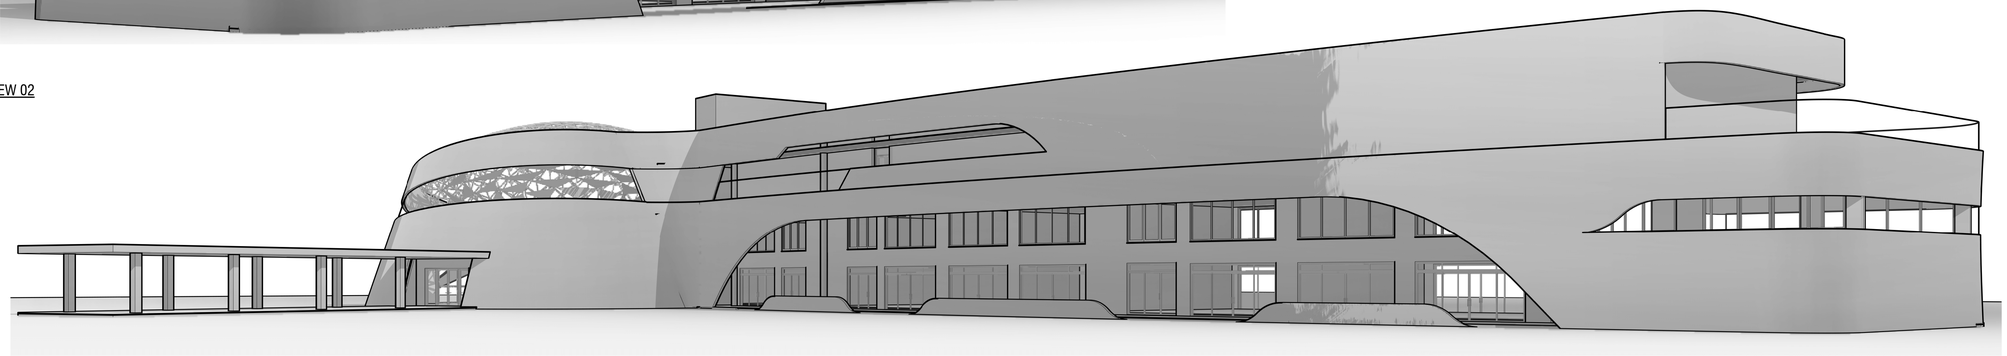

3D VIEW 03

3D VIEW 04

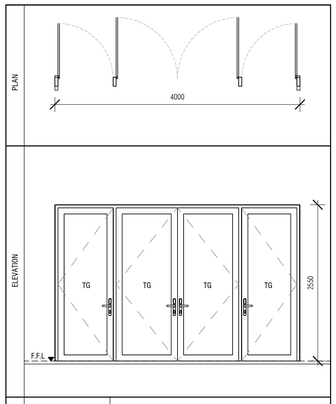

GENERAL	LOCATION	RB01 - RETAIL 01		
	TAG	D1		
	WALL OPENING DIM.	4000x2550mm (W x H)	TYPE	4 PANEL SWING DOOR
	QUANTITY	01 NOS.	OPEN AREA	10.20 Sqm
FRAME	FRAME SIZE	50x150mm	MATERIAL	80 MICRON POWDER COATED ALUMINUM
	FINISH	GRAY - MATTE FINISH		
DOOR PANEL	MATERIAL	80 MICRON POWDER COATED ALUMINUM		
	FINISH	GRAY - MATTE FINISH		
	INTERNAL PANEL TYPE	12 mm THK TEMPERED GLASS		
	FIRE RATING	1HR		
	ACOUSTIC RATING	(N/A)		
IRONMONGERY	HINGES/ SLIDING GEAR	HAFFLE OR EQUIVALENT		
	HANDLE	HAFFLE OR EQUIVALENT		
	LOCK SET	HAFFLE OR EQUIVALENT		
	DOOR VIEWER	(N/A)		
	DOOR CLOSER	YES		
	SOFT CLOSING	YES		
	FLUSH BOLTS	YES		
	DOOR STOPPER	YES		
	RUBBER SEAL	YES		
	KICK PLATE	NO		
	ACCESS CONTROL	KEY		

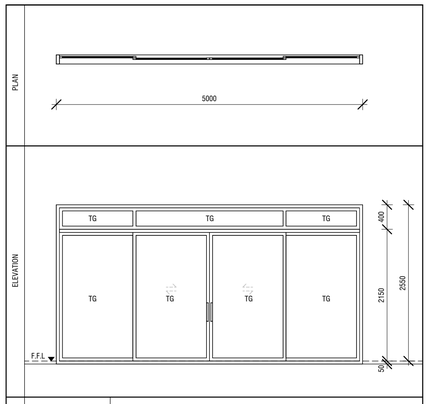

GENERAL	LOCATION	RB01 - RETAIL 02 TOP, RETAIL 03 TOP, RETAIL 04 TOP, RETAIL 05 TOP, WATER SPORTS TOP		
	TAG	D2		
	WALL OPENING DIM.	5000x2550mm (W x H)	TYPE	4 PANEL SLIDING DOOR
	QUANTITY	21 NOS.	OPEN AREA	12.75 Sqm
FRAME	FRAME SIZE	50x150mm	MATERIAL	80 MICRON POWDER COATED ALUMINUM
	FINISH	GRAY - MATTE FINISH		
DOOR PANEL	MATERIAL	80 MICRON POWDER COATED ALUMINUM		
	FINISH	GRAY - MATTE FINISH		
	INTERNAL PANEL TYPE	12 mm THK TEMPERED GLASS		
	FIRE RATING	1HR		
	ACOUSTIC RATING	(N/A)		
IRONMONGERY	HINGES/ SLIDING GEAR	HAFFLE OR EQUIVALENT		
	HANDLE	HAFFLE OR EQUIVALENT		
	LOCK SET	HAFFLE OR EQUIVALENT		
	DOOR VIEWER	(N/A)		
	DOOR CLOSER	NO		
	SOFT CLOSING	NO		
	FLUSH BOLTS	NO		
	DOOR STOPPER	NO		
	RUBBER SEAL	YES		
	KICK PLATE	NO		
	ACCESS CONTROL	KEY		

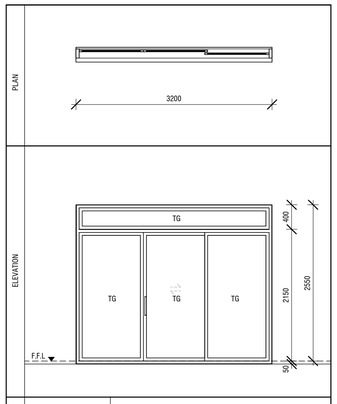

GENERAL	LOCATION	RB01 - RETAIL 02, RETAIL 03, BOH OFFICE, CLASSROOM		
	TAG	D3		
	WALL OPENING DIM.	3200x2550mm (W x H)	TYPE	3 PANEL SLIDING DOOR
	QUANTITY	03 NOS.	OPEN AREA	8.16 Sqm
FRAME	FRAME SIZE	50x150mm	MATERIAL	80 MICRON POWDER COATED ALUMINUM
	FINISH	GRAY - MATTE FINISH		
DOOR PANEL	MATERIAL	80 MICRON POWDER COATED ALUMINUM		
	FINISH	GRAY - MATTE FINISH		
	INTERNAL PANEL TYPE	12 mm THK TEMPERED GLASS		
	FIRE RATING	1HR		
	ACOUSTIC RATING	(N/A)		
IRONMONGERY	HINGES/ SLIDING GEAR	HAFFLE OR EQUIVALENT		
	HANDLE	HAFFLE OR EQUIVALENT		
	LOCK SET	HAFFLE OR EQUIVALENT		
	DOOR VIEWER	(N/A)		
	DOOR CLOSER	NO		
	SOFT CLOSING	NO		
	FLUSH BOLTS	NO		
	DOOR STOPPER	NO		
	RUBBER SEAL	YES		
	KICK PLATE	NO		
	ACCESS CONTROL	KEY		

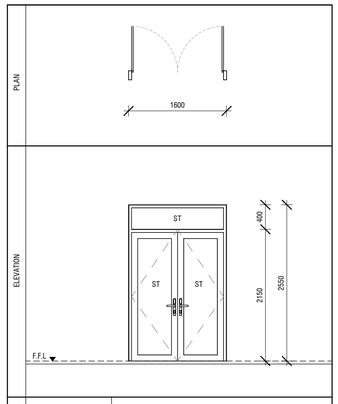

GENERAL	LOCATION	RB01 - DINING & LIVING, FOYER		
	TAG	D4		
	WALL OPENING DIM.	1600x2550mm (W x H)	TYPE	2 PANEL SWING DOOR
	QUANTITY	02 NOS.	OPEN AREA	4.08 Sqm
FRAME	FRAME SIZE	50x150mm	MATERIAL	SOLID TIMBER
	FINISH	TIMBER FINISH		
DOOR PANEL	MATERIAL	SOLID TIMBER		
	FINISH	TIMBER FINISH		
	INTERNAL PANEL TYPE	SOLID TIMBER PANEL		
	FIRE RATING	1HR		
	ACOUSTIC RATING	(N/A)		
IRONMONGERY	HINGES/ SLIDING GEAR	HAFFLE OR EQUIVALENT		
	HANDLE	HAFFLE OR EQUIVALENT		
	LOCK SET	HAFFLE OR EQUIVALENT		
	DOOR VIEWER	NO		
	DOOR CLOSER	YES		
	SOFT CLOSING	YES		
	FLUSH BOLTS	YES		
	DOOR STOPPER	YES		
	RUBBER SEAL	YES		
	KICK PLATE	NO		
	ACCESS CONTROL	KEY		

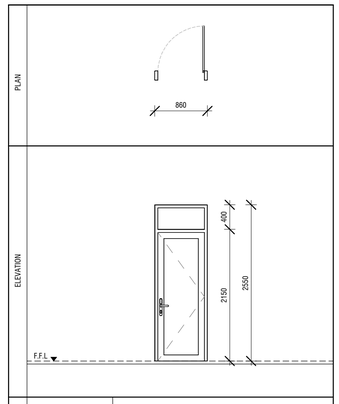

GENERAL	LOCATION	RB01 - MASTER BDRM, GUEST RM, PANTRY, POW RM		
	TAG	D5		
	WALL OPENING DIM.	860x2550mm (W x H)	TYPE	1 PANEL SWING DOOR
	QUANTITY	06 NOS.	OPEN AREA	2.19 Sqm
FRAME	FRAME SIZE	50x150mm	MATERIAL	BY ID CONSULTANT
	FINISH			
DOOR PANEL	MATERIAL			
	FINISH			
	INTERNAL PANEL TYPE			
	FIRE RATING			
	ACOUSTIC RATING			
IRONMONGERY	HINGES/ SLIDING GEAR			
	HANDLE			
	LOCK SET	BY ID CONSULTANT		
	DOOR VIEWER			
	DOOR CLOSER			
	SOFT CLOSING			
	FLUSH BOLTS			
	DOOR STOPPER			
	RUBBER SEAL			
	KICK PLATE			
	ACCESS CONTROL			

DOOR SCHEDULE

No.	DESCRIPTION	WIDTH	HEIGHT	QTY
D1	4 Panel Swing Door - Glass Panel - Aluminum Frame	4000	2550	1
D2	4 Panel Sliding Door - Clear Glass Panel - Aluminum Frame	5000	2550	21
D3	3 Panel Sliding Door - Clear Glass Panel - Aluminum Frame	3200	2550	3
D4	2 Panel Swing Door - Solid Timber Panel - Solid Timber Frame	1600	2550	2
D5	1 Panel Swing Door - Solid Timber Panel - Solid Timber Frame	860	2550	6
D6	1 Panel Swing Door - Solid Timber Panel - Solid Timber Frame	800	2550	3
D7	1 Panel Swing Door - Frosted Glass Panel - Aluminum Frame	2100	2550	5
D8	1 Panel Swing Door - Frosted Glass Panel - Frameless	1200	2150	1
D9	8 Panel Sliding Door - Clear Glass Panel - Aluminum Frame	10000	2550	2
D10	4 Panel Sliding Door - Clear Glass Panel - Aluminum Frame	5300	2550	4
FD1	1 Panel Swing Door -Wired Glass view Panel + Panic bar - Galvenize Frame	1000	2150	7
LD1	1 Panel Swing Door - Solid Timber Panel - Solid Timber Frame	900	2150	3

LEGEND

CG - CLEAR GLASS
FTG - FIXED CLEAR GLASS
FG - FROSTED GLASS
FFG - FIXED FROSTED GLASS
RG - REFLECTED GLASS
FRG - FIXED REFLECTED GLASS
TG - TEMPERED CLEAR GLASS
AL - ALUMINUM LOUVERS
ST - SOLID TIMBER
T - TIMBER
PVC - POLYVINYL CHLORIDE
GS - GALVANIZED STEEL

NOTE

- ALL DOORS & WINDOWS TO BE CHECKED ON SITE BEFORE FABRICATION.
- ALL DOOR & WINDOWS VIEWED FROM EXTERIOR, FOR DOOR SWING, REFER TO FLOOR PLANS.
- INTERNAL DOORS FRAME DEPTH TO BE WIDTH OF THE WALL.
- THE DOORS / WINDOWS WHICH DO NOT TOUCH THE BEAM SHALL HAVE A LINTEL BEAM (LB)
  ABOVE THE DOOR / WINDOW.
- FOR ALL THE WINDOWS PUT A SILL BEAM BELOW THE WINDOW (SB)

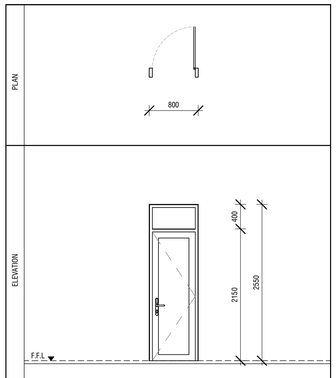

GENERAL	LOCATION	RB01 - STM RM, WIR, WC, MASTER BDRM, POW RM, STUDY, KITCHEN, GUEST RM, WIR, PANTRY		
	TAG	D6		
	WALL OPENING DIM.	800x2550mm (W x H)	TYPE	1 PANEL SWING DOOR
	QUANTITY	03 NOS.	OPEN AREA	2.04 Sqm
FRAME	FRAME SIZE	50x150mm	MATERIAL	BY ID CONSULTANT
	FINISH			
DOOR PANEL	MATERIAL			
	FINISH			
	INTERNAL PANEL TYPE			
	FIRE RATING			
	ACOUSTIC RATING			
IRONMONGERY	HINGES/ SLIDING GEAR			
	HANDLE			
	LOCK SET	BY ID CONSULTANT		
	DOOR VIEWER			
	DOOR CLOSER			
	SOFT CLOSING			
	FLUSH BOLTS			
	DOOR STOPPER			
	RUBBER SEAL			
	KICK PLATE			
	ACCESS CONTROL			

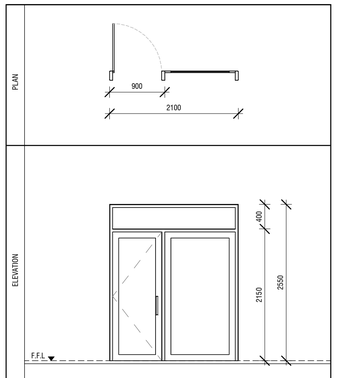

GENERAL	LOCATION	RB01 - BATH, WC		
	TAG	D7		
	WALL OPENING DIM.	2100x2550mm (W x H)	TYPE	1 PANEL SWING DOOR + FIXED PANEL
	QUANTITY	05 NOS.	OPEN AREA	5.36 Sqm
FRAME	FRAME SIZE	50x150mm	MATERIAL	BY ID CONSULTANT
	FINISH			
DOOR PANEL	MATERIAL			
	FINISH			
	INTERNAL PANEL TYPE			
	FIRE RATING			
	ACOUSTIC RATING			
IRONMONGERY	HINGES/ SLIDING GEAR			
	HANDLE			
	LOCK SET	BY ID CONSULTANT		
	DOOR VIEWER			
	DOOR CLOSER			
	SOFT CLOSING			
	FLUSH BOLTS			
	DOOR STOPPER			
	RUBBER SEAL			
	KICK PLATE			
	ACCESS CONTROL			

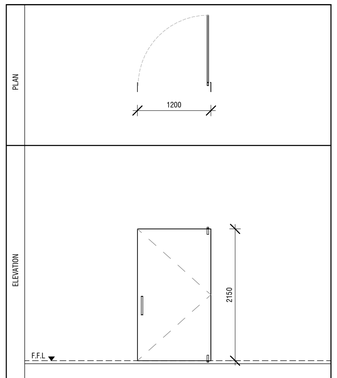

GENERAL	LOCATION	RB01 - WALK IN ROBE, FOYER		
	TAG	D8		
	WALL OPENING DIM.	1200x2150mm (W x H)	TYPE	1 PANEL FRAME LESS SWING DOOR
	QUANTITY	01 NOS.	OPEN AREA	2.58 Sqm
FRAME	FRAME SIZE	-	MATERIAL	BY ID CONSULTANT
	FINISH			
DOOR PANEL	MATERIAL			
	FINISH			
	INTERNAL PANEL TYPE			
	FIRE RATING			
	ACOUSTIC RATING			
IRONMONGERY	HINGES/ SLIDING GEAR			
	HANDLE			
	LOCK SET	BY ID CONSULTANT		
	DOOR VIEWER			
	DOOR CLOSER			
	SOFT CLOSING			
	FLUSH BOLTS			
	DOOR STOPPER			
	RUBBER SEAL			
	KICK PLATE			
	ACCESS CONTROL			

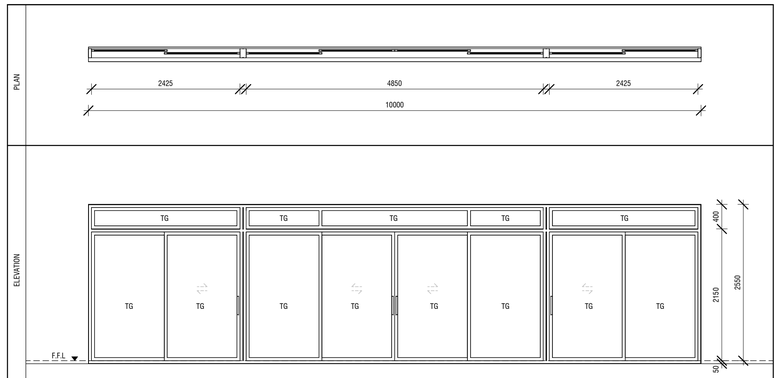

GENERAL	LOCATION	RB01 - DINING, LIVING		
	TAG	D9		
	WALL OPENING DIM.	10000x2550mm (W x H)	TYPE	8 PANEL SLIDING DOOR
	QUANTITY	02 NOS.	OPEN AREA	25.50 Sqm
FRAME	FRAME SIZE	50x150mm	MATERIAL	80 MICRON POWDER COATED ALUMINUM
	FINISH	GRAY - MATTE FINISH		
DOOR PANEL	MATERIAL	80 MICRON POWDER COATED ALUMINUM		
	FINISH	GRAY - MATTE FINISH		
	INTERNAL PANEL TYPE	12 mm THK TEMPERED GLASS		
	FIRE RATING	1HR		
	ACOUSTIC RATING	(N/A)		
IRONMONGERY	HINGES/ SLIDING GEAR	HAFFLE OR EQUIVALENT		
	HANDLE	HAFFLE OR EQUIVALENT		
	LOCK SET	HAFFLE OR EQUIVALENT		
	DOOR VIEWER	(N/A)		
	DOOR CLOSER	NO		
	SOFT CLOSING	NO		
	FLUSH BOLTS	NO		
	DOOR STOPPER	NO		
	RUBBER SEAL	YES		
	KICK PLATE	NO		
	ACCESS CONTROL	KEY		

DOOR SCHEDULE & DETAILS - 01

1 : 50

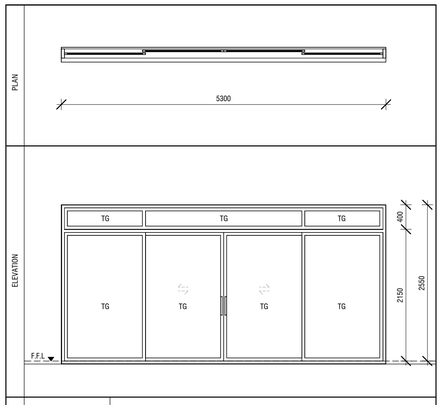

GENERAL	LOCATION	RB01 - ENSUITE, GUEST RM		
	TAG	D10		
	WALL OPENING DIM.	5300x2550mm (W x H)	TYPE	4 PANEL SLIDING DOOR
	QUANTITY	04 NOS.	OPEN AREA	13.52 Sqm
FRAME	FRAME SIZE	50x150mm	MATERIAL	80 MICRON POWDER COATED ALUMINUM
	FINISH	GRAY - MATTE FINISH		
DOOR PANEL	MATERIAL	80 MICRON POWDER COATED ALUMINUM		
	FINISH	GRAY - MATTE FINISH		
	INTERNAL PANEL TYPE	12 mm THK TEMPERED GLASS		
	FIRE RATING	1HR		
	ACOUSTIC RATING	(N/A)		
IRONMONGERY	HINGES/ SLIDING GEAR	HAFFLE OR EQUIVALENT		
	HANDLE	HAFFLE OR EQUIVALENT		
	LOCK SET	HAFFLE OR EQUIVALENT		
	DOOR VIEWER	NO		
	DOOR CLOSER	NO		
	SOFT CLOSING	NO		
	FLUSH BOLTS	NO		
	DOOR STOPPER	NO		
	RUBBER SEAL	YES		
	KICK PLATE	NO		
	ACCESS CONTROL	KEY		

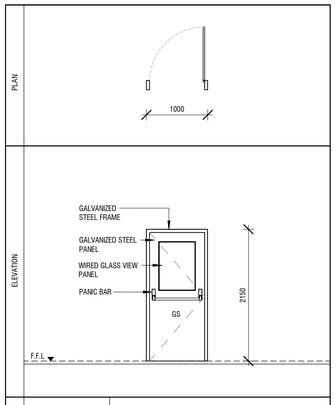

GENERAL	LOCATION	RB01 - STAIRS		
	TAG	FD1		
	WALL OPENING DIM.	1000x2150mm (W x H)	TYPE	1 PANEL SWING DOOR WITH PANIC
	QUANTITY	07 NOS.	OPEN AREA	2.15 Sqm
FRAME	FRAME SIZE	50x150mm	MATERIAL	GALVANIZED STEEL
	FINISH	GRAY - MATTE FINISH		
DOOR PANEL	MATERIAL	GALVANIZED STEEL		
	FINISH	GRAY - MATTE FINISH		
	INTERNAL PANEL TYPE	GALVANIZED STEEL PANEL WITH WIRED GLASS VIEW PANEL WITH PANIC BAR		
	FIRE RATING	1HR		
	ACOUSTIC RATING	(N/A)		
IRONMONGERY	HINGES/ SLIDING GEAR	HAFFLE OR EQUIVALENT		
	HANDLE	HAFFLE OR EQUIVALENT		
	LOCK SET	HAFFLE OR EQUIVALENT		
	DOOR VIEWER	YES		
	DOOR CLOSER	YES		
	SOFT CLOSING	YES		
	FLUSH BOLTS	NO		
	DOOR STOPPER	YES		
	RUBBER SEAL	YES		
	KICK PLATE	YES		
	ACCESS CONTROL	KEY		

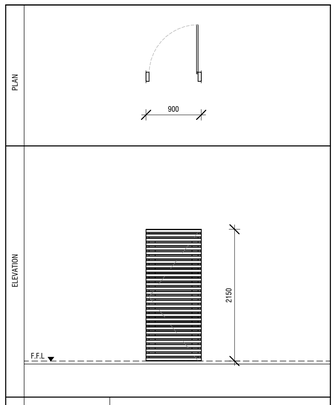

GENERAL	LOCATION	RB01 - ELV		
	TAG	LD1		
	WALL OPENING DIM.	900x2150mm (W x H)	TYPE	1 PANEL SWING DOOR
	QUANTITY	03 NOS.	OPEN AREA	1.94 Sqm
FRAME	FRAME SIZE	-	MATERIAL	BY ID CONSULTANT
	FINISH			
DOOR PANEL	MATERIAL			
	FINISH			
	INTERNAL PANEL TYPE			
	FIRE RATING			
	ACOUSTIC RATING			
IRONMONGERY	HINGES/ SLIDING GEAR			
	HANDLE			
	LOCK SET	BY ID CONSULTANT		
	DOOR VIEWER			
	DOOR CLOSER			
	SOFT CLOSING			
	FLUSH BOLTS			
	DOOR STOPPER			
	RUBBER SEAL			
	KICK PLATE			
	ACCESS CONTROL			

DOOR SCHEDULE

No.	DESCRIPTION	WIDTH	HEIGHT	QTY
D1	4 Panel Swing Door - Glass Panel - Aluminum Frame	4000	2550	1
D2	4 Panel Sliding Door - Clear Glass Panel - Aluminum Frame	5000	2550	21
D3	3 Panel Sliding Door - Clear Glass Panel - Aluminum Frame	3200	2550	3
D4	2 Panel Swing Door - Solid Timber Panel - Solid Timber Frame	1600	2550	2
D5	1 Panel Swing Door - Solid Timber Panel - Solid Timber Frame	860	2550	6
D6	1 Panel Swing Door - Solid Timber Panel - Solid Timber Frame	800	2550	3
D7	1 Panel Swing Door - Frosted Glass Panel - Aluminum Frame	2100	2550	5
D8	1 Panel Swing Door - Frosted Glass Panel - Frameless	1200	2150	1
D9	8 Panel Sliding Door - Clear Glass Panel - Aluminum Frame	10000	2550	2
D10	4 Panel Sliding Door - Clear Glass Panel - Aluminum Frame	5300	2550	4
FD1	1 Panel Swing Door -Wired Glass view Panel+Panic bar - Galvenize Frame	1000	2150	7
LD1	1 Panel Swing Door - Solid Timber Panel - Solid Timber Frame	900	2150	3

LEGEND

CG - CLEAR GLASS
FTG - FIXED CLEAR GLASS
FG - FROSTED GLASS
FFG - FIXED FROSTED GLASS
RG - REFLECTED GLASS
FRG - FIXED REFLECTED GLASS
TG - TEMPERED CLEAR GLASS
AL - ALUMINUM LOUVERS
ST - SOLID TIMBER
T - TIMBER
PVC - POLYVINYL CHLORIDE
GS - GALVANIZED STEEL

NOTE

- ALL DOORS & WINDOWS TO BE CHECKED ON SITE BEFORE FABRICATION.
- ALL DOOR & WINDOWS VIEWED FROM EXTERIOR, FOR DOOR SWING, REFER TO FLOOR PLANS.
- INTERNAL DOORS FRAME DEPTH TO BE WIDTH OF THE WALL.
- THE DOORS / WINDOWS WHICH DO NOT TOUCH THE BEAM SHALL HAVE A LINTEL BEAM (LB) ABOVE THE DOOR / WINDOW.
- FOR ALL THE WINDOWS PUT A SILL BEAM BELOW THE WINDOW (SB)

DOOR SCHEDULE & DETAILS - 02

1 : 50

PLAN

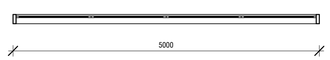

ELEVATION

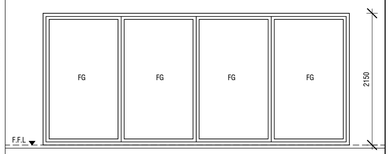

GENERAL	LOCATION	RB01 - RETAIL 02 TOP, RETAIL 03 TOP, RETAIL 04 TOP, RETAIL 05 TOP, WATER SPORTS TOP		
	TAG	FG1		
	WALL OPENING DIM.	5000x2150mm (W x H)	TYPE	4 PANEL FIXED GLASS
	QUANTITY	21 NOS.	OPEN AREA	10.75 Sqm
FRAME	FRAME SIZE	50x150mm	MATERIAL	80 MICRONS ALUMINUM POWDER COATED FRAME
	FINISH	GRAY - MATTE FINISH		
WINDOW PANEL	PANEL FRAME MATERIAL	80 MICRONS ALUMINUM POWDER COATED FRAME		
	PANEL FRAME FINISH	GRAY - MATTE FINISH		
	GLAZING	12mm THICK TEMPERED CLEAR GLASS		
	FIRE RATING	1HR		
	ACOUSTIC RATING	-		
IRONMONGERY	HINGES/ SLIDING GEAR	HAFFLE OR EQUIVALENT		
	HANDLE	HAFFLE OR EQUIVALENT		
	LOCK	HAFFLE OR EQUIVALENT		
	FLUSH BOLTS	HAFFLE OR EQUIVALENT		

PLAN

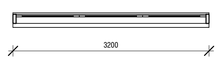

ELEVATION

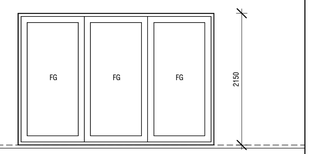

GENERAL	LOCATION	RB01 - RETAIL 02 TOP, RETAIL 03 TOP, RETAIL 04 TOP, RETAIL 05 TOP		
	TAG	FG2		
	WALL OPENING DIM.	3200x2150mm (W x H)	TYPE	3 PANEL FIXED GLASS
	QUANTITY	03 NOS.	OPEN AREA	6.88 Sqm
FRAME	FRAME SIZE	50x150mm	MATERIAL	80 MICRONS ALUMINUM POWDER COATED FRAME
	FINISH	GRAY - MATTE FINISH		
WINDOW PANEL	PANEL FRAME MATERIAL	80 MICRONS ALUMINUM POWDER COATED FRAME		
	PANEL FRAME FINISH	GRAY - MATTE FINISH		
	GLAZING	12mm THICK TEMPERED CLEAR GLASS		
	FIRE RATING	1HR		
	ACOUSTIC RATING	-		
IRONMONGERY	HINGES/ SLIDING GEAR	HAFFLE OR EQUIVALENT		
	HANDLE	HAFFLE OR EQUIVALENT		
	LOCK	HAFFLE OR EQUIVALENT		
	FLUSH BOLTS	HAFFLE OR EQUIVALENT		

PLAN

ELEVATION

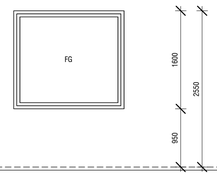

GENERAL	LOCATION	RB01 - LIFT LOBBY		
	TAG	FG3		
	WALL OPENING DIM.	1800x1600mm (W x H)	TYPE	1 PANEL FIXED GLASS
	QUANTITY	03 NOS.	OPEN AREA	2.88 Sqm
FRAME	FRAME SIZE	50x100mm	MATERIAL	80 MICRONS ALUMINUM POWDER COATED FRAME
	FINISH	GRAY - MATTE FINISH		
WINDOW PANEL	PANEL FRAME MATERIAL	80 MICRONS ALUMINUM POWDER COATED FRAME		
	PANEL FRAME FINISH	GRAY - MATTE FINISH		
	GLAZING	12mm THICK TEMPERED CLEAR GLASS		
	FIRE RATING	1HR		
	ACOUSTIC RATING	-		
IRONMONGERY	HINGES/ SLIDING GEAR	HAFFLE OR EQUIVALENT		
	HANDLE	HAFFLE OR EQUIVALENT		
	LOCK	HAFFLE OR EQUIVALENT		
	FLUSH BOLTS	HAFFLE OR EQUIVALENT		

PLAN

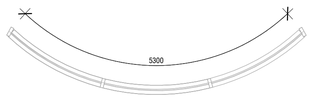

ELEVATION

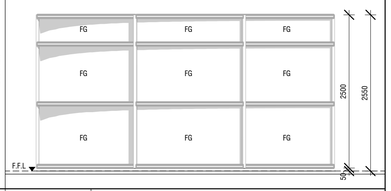

GENERAL	LOCATION	RB01 - LIFT LOBBY		
	TAG	FG4		
	WALL OPENING DIM.	5325x3050mm (W x H)	TYPE	1 PANEL FIXED GLASS
	QUANTITY	03 NOS.	OPEN AREA	16.24 Sqm
FRAME	FRAME SIZE	50x100mm	MATERIAL	80 MICRONS ALUMINUM POWDER COATED FRAME
	FINISH	GRAY - MATTE FINISH		
WINDOW PANEL	PANEL FRAME MATERIAL	80 MICRONS ALUMINUM POWDER COATED FRAME		
	PANEL FRAME FINISH	GRAY - MATTE FINISH		
	GLAZING	12mm THICK TEMPERED CLEAR GLASS		
	FIRE RATING	1HR		
	ACOUSTIC RATING	-		
IRONMONGERY	HINGES/ SLIDING GEAR	HAFFLE OR EQUIVALENT		
	HANDLE	HAFFLE OR EQUIVALENT		
	LOCK	HAFFLE OR EQUIVALENT		
	FLUSH BOLTS	HAFFLE OR EQUIVALENT		

WINDOW SCHEDULE & DETAILS

1 : 50

WINDOW SCHEDULE

NO	DESCRIPTION	WIDTH	HEIGHT	QTY
FG1	4 Panel Sliding Door - Clear Glass Panel - Aluminum Frame	5000	2150	21
FG2	3 Panel Sliding Door - Clear Glass Panel - Aluminum Frame	3200	2150	3
FG3	1 Panel Window - No Panel - Aluminum Frame	1800	1600	3

LEGEND

CG - CLEAR GLASS
FTG - FIXED CLEAR GLASS
FG - FROSTED GLASS
FFG - FIXED FROSTED GLASS
RG - REFLECTED GLASS
FRG - FIXED REFLECTED GLASS
TG - TEMPERED CLEAR GLASS
AL - ALUMINUM LOUVERS
ST - SOLID TIMBER
T - TIMBER
PVC - POLYVINYL CHLORIDE
GS - GALVANIZED STEEL

NOTE

- ALL DOORS & WINDOWS TO BE CHECKED ON SITE BEFORE FABRICATION.
- ALL DOOR & WINDOWS VIEWED FROM EXTERIOR, FOR DOOR SWING, REFER TO FLOOR PLANS.
- INTERNAL DOORS FRAME DEPTH TO BE WIDTH OF THE WALL.
- THE DOORS / WINDOWS WHICH DO NOT TOUCH THE BEAM SHALL HAVE A LINTEL BEAM (LB)
  ABOVE THE DOOR / WINDOW.
- FOR ALL THE WINDOWS PUT A SILL BEAM BELOW THE WINDOW (SB)

LEGEND

CT-01 9MM THICK MOISTURE RESISTANT GYPSUM CEILING WITH ALUMINIUM FRAMING CHANNELS. GROUND SMOOTH AND COMPLETE WITH SELECTED PAINT FINISH.

CT-02 6MM THICK CEMENT BOARD CEILING WITH ALUMINIUM FRAMING CHANNEL. GROUND SMOOTH AND COMPLETE WITH SELECTED PAINT FINISH.

CT-XX / X.XX m — CEILING TYPE / CEILING LEVEL

NOTE: ANY UNIDENTIFIED AREAS TO HAVE EXPOSED SLAB SOFFIT (B-CF-C00) TO BE GROUND SMOOTH IN SELECT PAINT FINISH (ONE COAT OF PUTTY FOLLOWED BY SEALER AND 2 COATS OF PAINT)

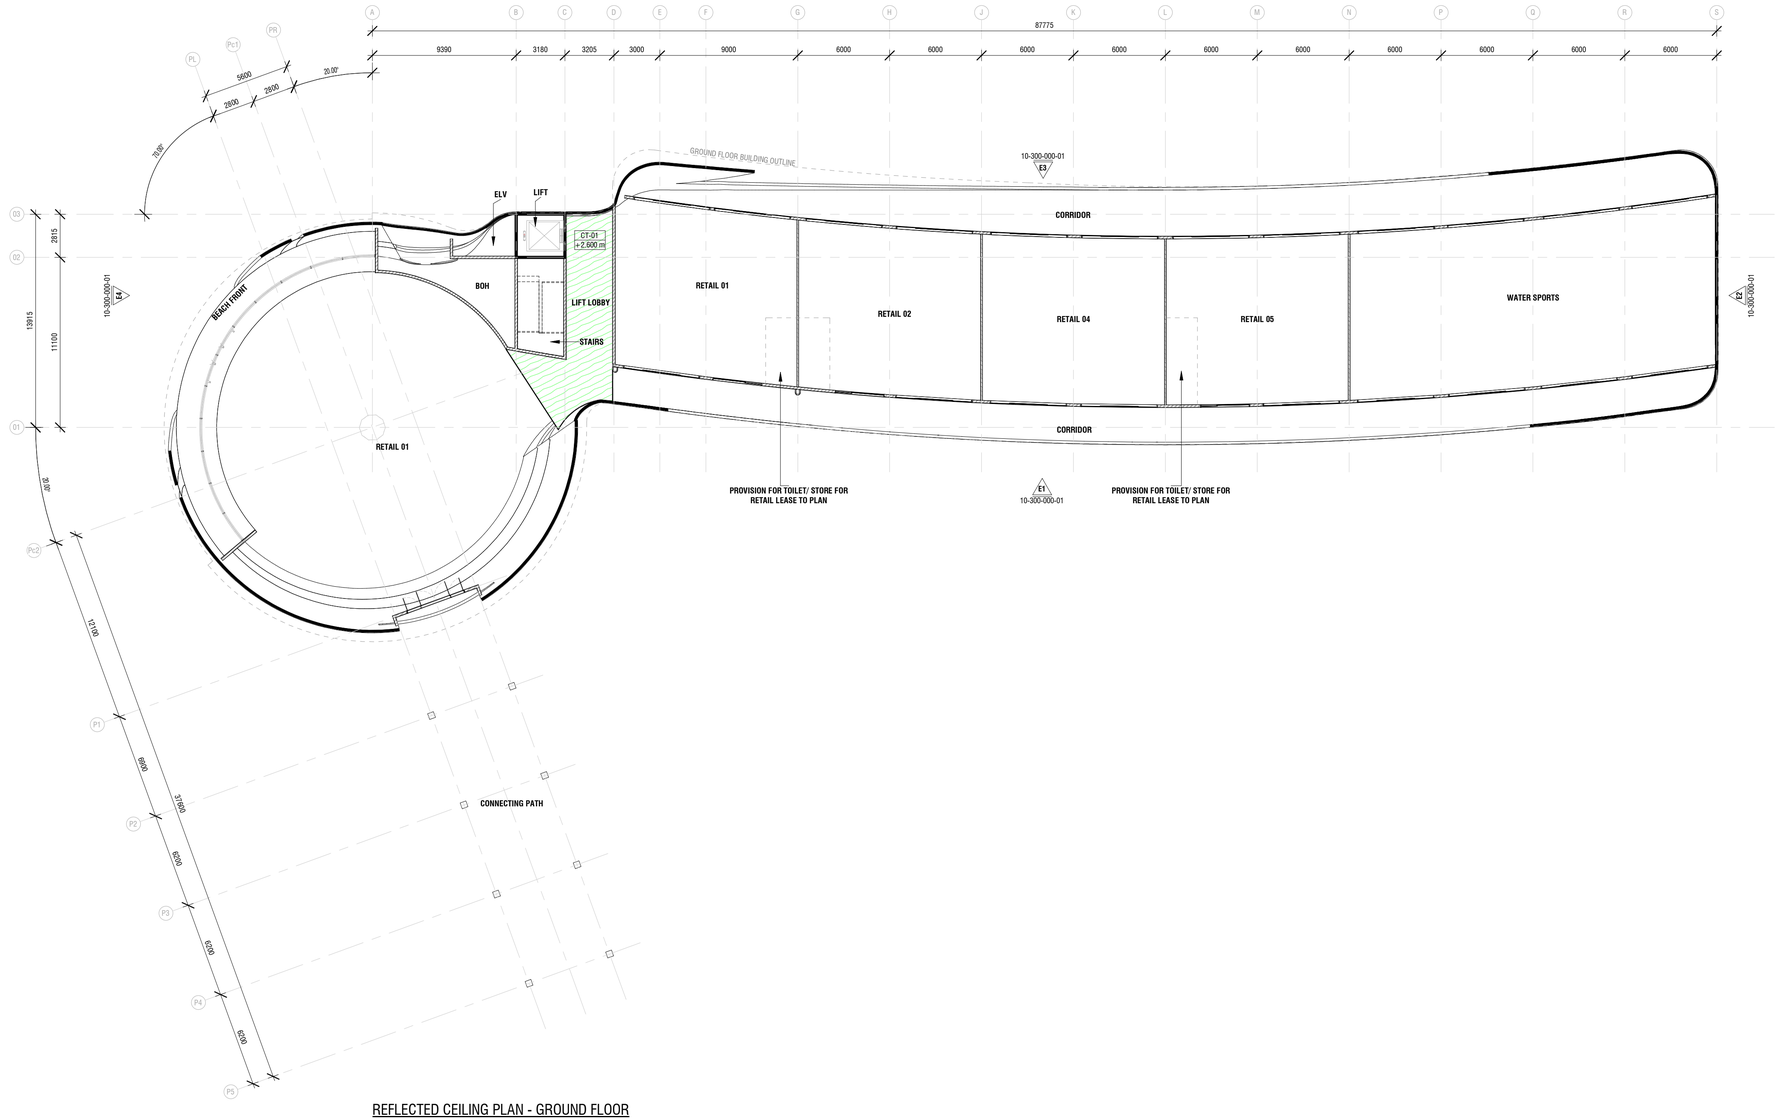

REFLECTED CEILING PLAN - GROUND FLOOR

1 : 200

LEGEND

CT-01 9MM THICK MOISTURE RESISTANT GYPSUM CEILING WITH ALUMINIUM FRAMING CHANNELS. GROUND SMOOTH AND COMPLETE WITH SELECTED PAINT FINISH.

CT-02 6MM THICK CEMENT BOARD CEILING WITH ALUMINIUM FRAMING CHANNEL. GROUND SMOOTH AND COMPLETE WITH SELECTED PAINT FINISH.

CT-XX / X.XX m — CEILING TYPE / CEILING LEVEL

NOTE: ANY UNIDENTIFIED AREAS TO HAVE EXPOSED SLAB SOFFIT (B-CF-C00) TO BE GROUND SMOOTH IN SELECT PAINT FINISH (ONE COAT OF PUTTY FOLLOWED BY SEALER AND 2 COATS OF PAINT)

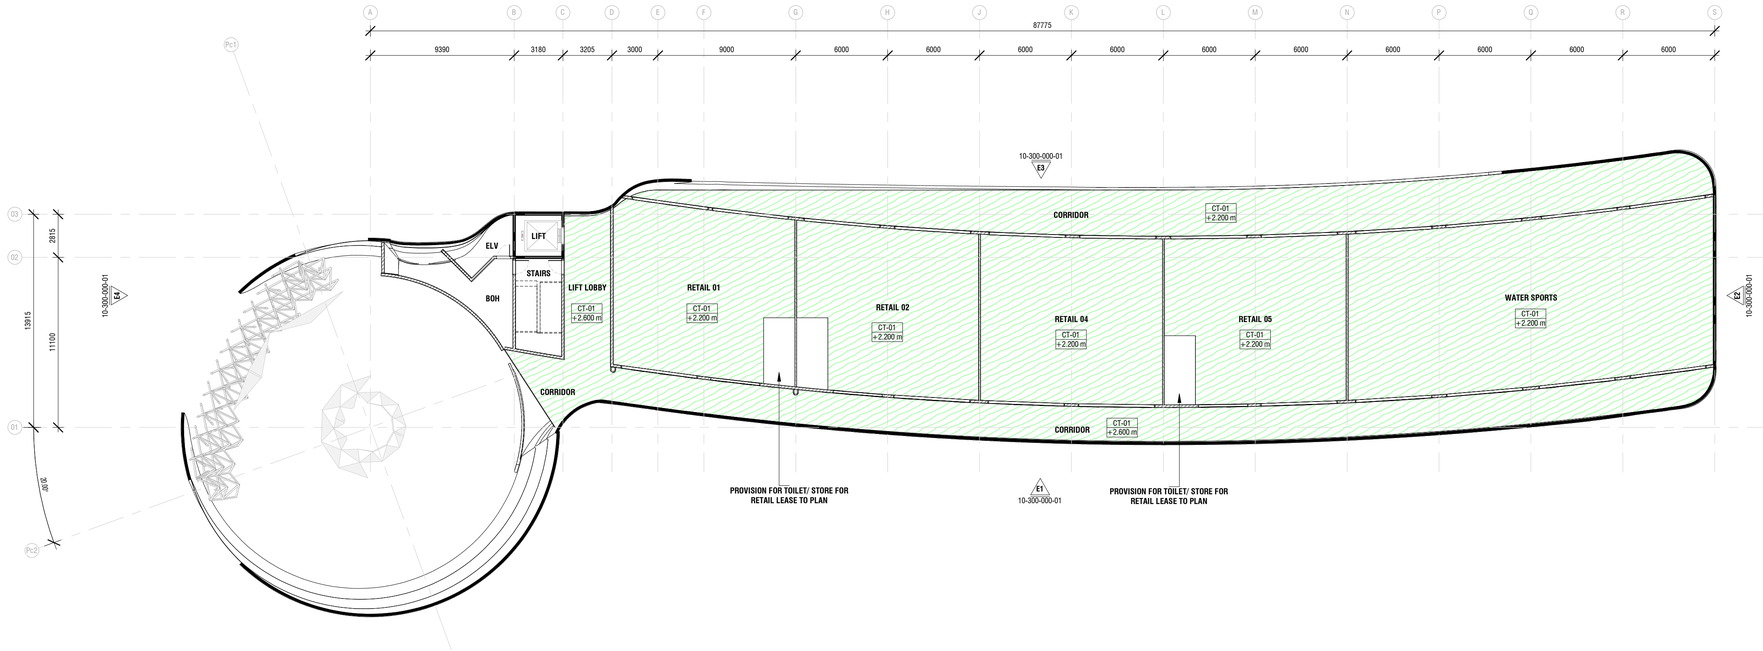

REFLECTED CEILING PLAN - FIRST FLOOR

1 : 200

LEGEND

CT-01		9MM THICK MOISTURE RESISTANT GYPSUM CEILING WITH ALUMINIUM FRAMING CHANNELS. GROUND SMOOTH AND COMPLETE WITH SELECTED PAINT FINISH.
CT-02		6MM THICK CEMENT BOARD CEILING WITH ALUMINIUM FRAMING CHANNEL. GROUND SMOOTH AND COMPLETE WITH SELECTED PAINT FINISH.

CT-XX / X.XX m — CEILING TYPE / CEILING LEVEL

NOTE: ANY UNIDENTIFIED AREAS TO HAVE EXPOSED SLAB SOFFIT (8-CF-C00) TO BE GROUND SMOOTH IN SELECT PAINT FINISH (ONE COAT OF PUTTY FOLLOWED BY SEALER AND 2 COATS OF PAINT)

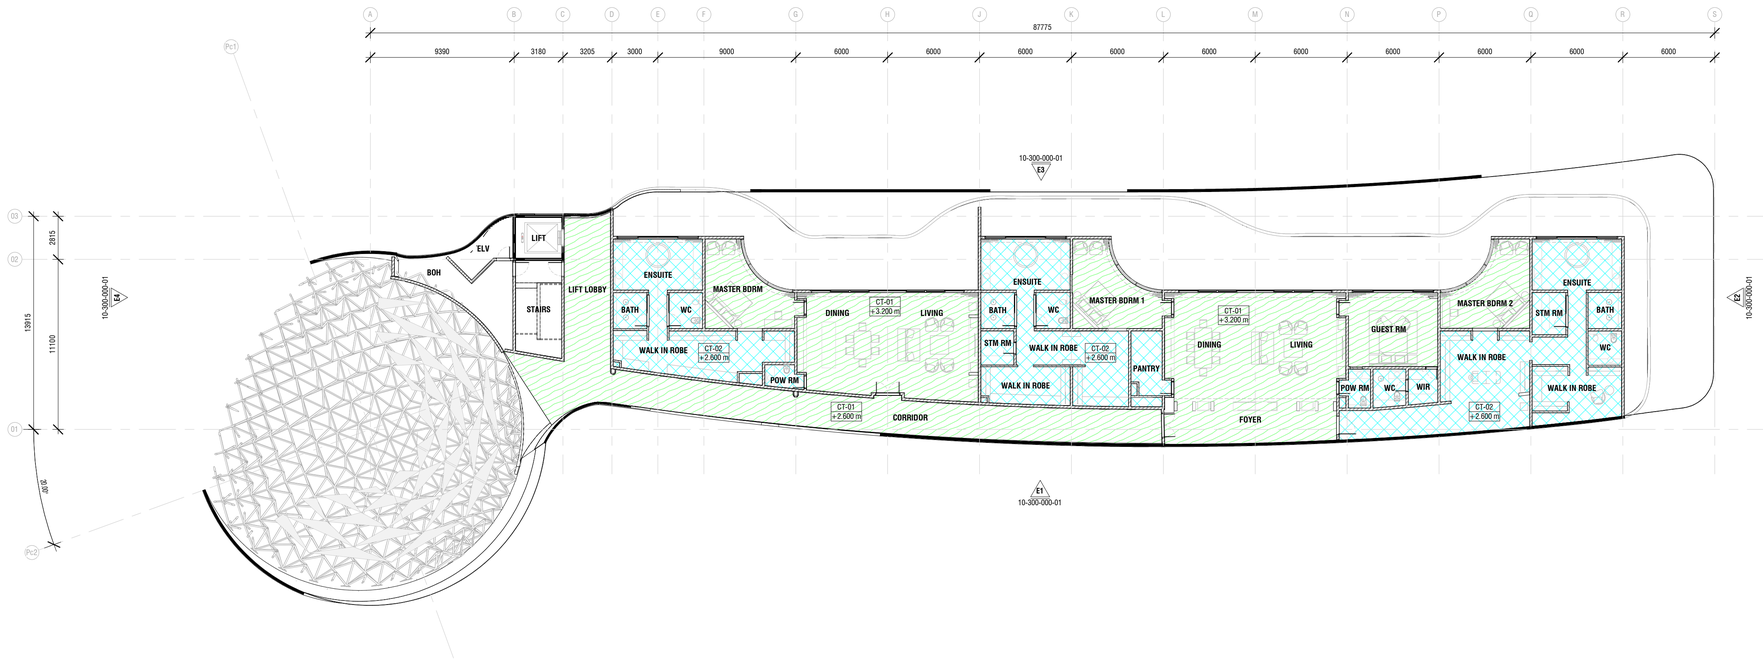

REFLECTED CEILING PLAN - PENTHOUSE FLOOR

1 : 200

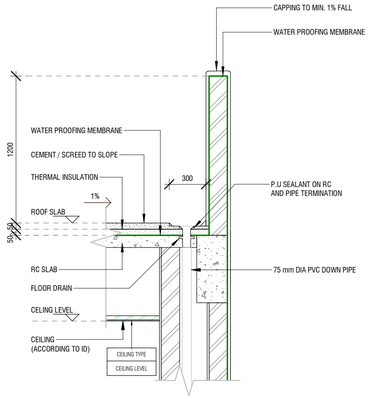

TYPICAL ROOF & FLOOR DRAIN DETAIL - 02

1 : 25

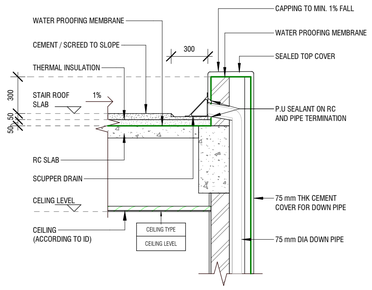

STAIR ROOF SCUPPER DRAIN DETAIL - 03

1 : 25

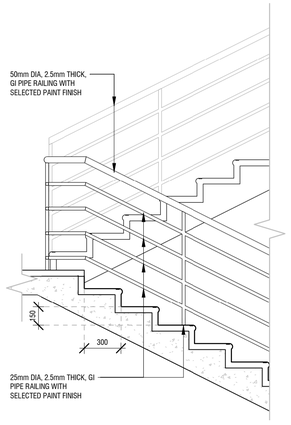

TYPICAL STAIR & HANDRAIL DETAIL - 04

1 : 25

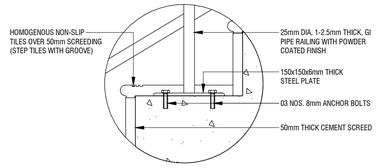

TYPICAL STAIRCASE DETAIL

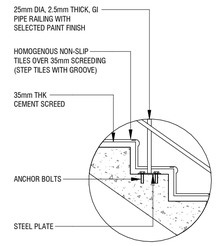

TYPICAL STAIRCASE STEP DETAIL

1 : 20

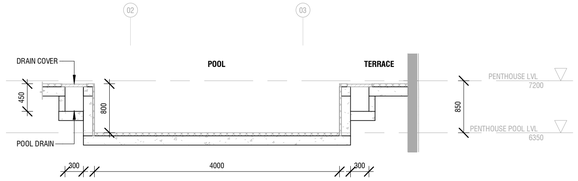

SECTION P2

1 : 50

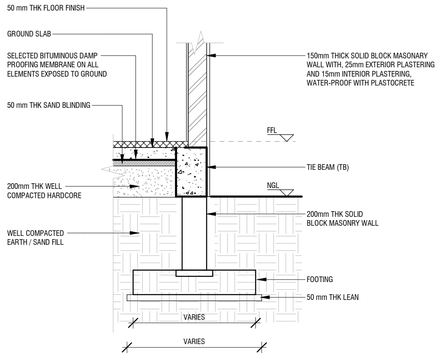

TYPICAL FLOOR TO WALL DETAIL - 01

1 : 25

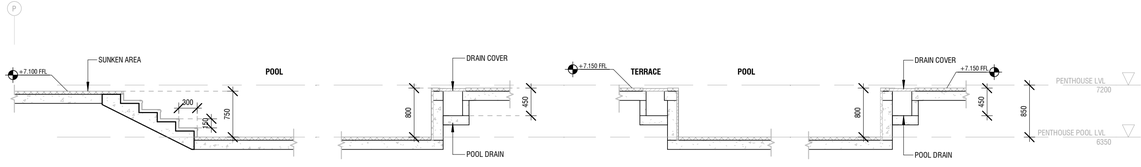

SECTION P1

1 : 50

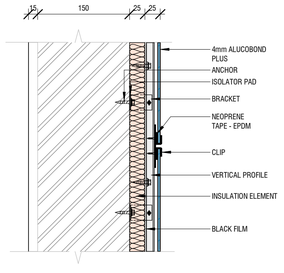

HORIZONTAL CLADDING DETAIL 01

1 : 5

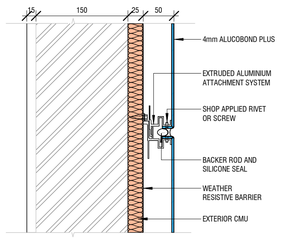

HORIZONTAL CLADDING DETAIL 02

1 : 5

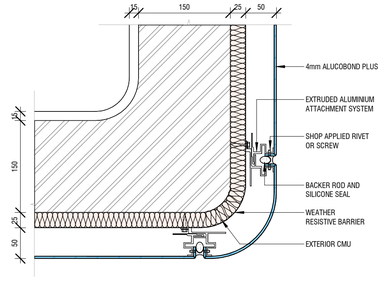

CURVED CLADDING DETAIL

1 : 5